
PLANTA BRIQUETADORA / CONFIGURADOR 3D


R18 / RECORRIDO Y TRANSFERENCIAS / DISPOSICION 1:100

PLANTA BRIQUETADORA · R18 | 2026-10-19 | A1 horizontal - milimetros

LATERAL / NPT +0

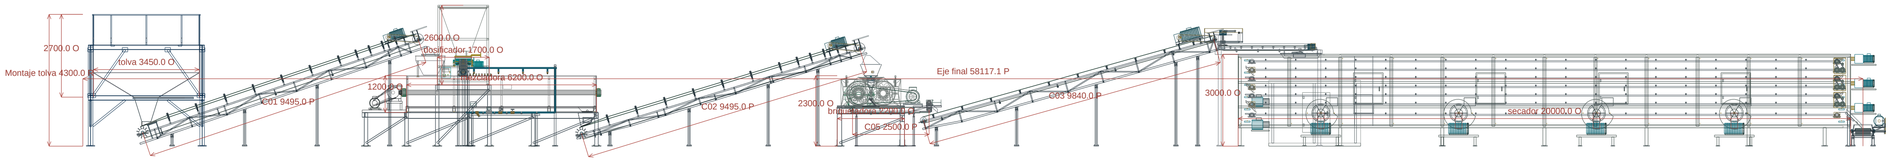

SUPERIOR

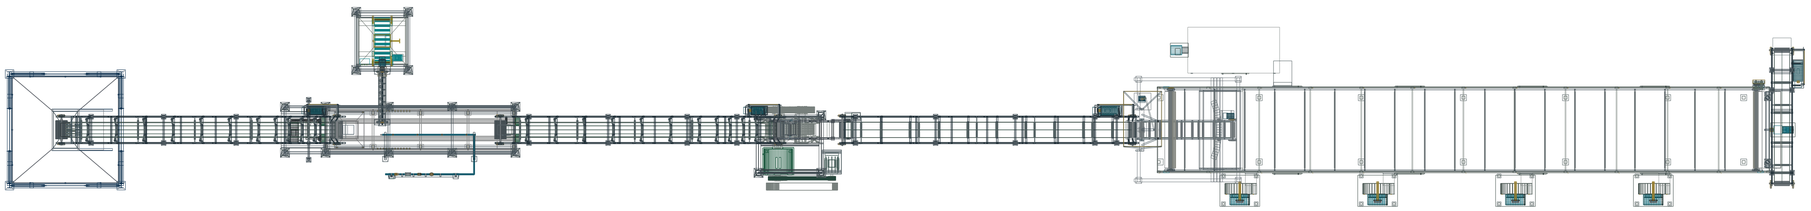

TRANSPORTADORES / ENTRE EJES Y ALTURAS DESDE NPT

ID	Servicio	Entre ejes mm	Pendiente	Cola Z	Cabeza Z	Banda mm
C01	Carbon / mezcladora	9495.0	18.67°	450.0	3490.1	500.0 P
C02	Mezcla / prensa	9495.0	16.99°	420.0	3195.1	500.0 P
C05	Colectora briquetas	2500.0	0.00°	1182.0	1182.0	500.0 P
C03	Elevacion / repartidor	9840.0	15.62°	850.0	3500.0	500.0 P
C04	Salida secador	4350.0	0.00°	500.0	500.0	500.0 R

Envolvente mecanica 58855.1 mm / con accesos 61117.1 mm / reserva 72000.0 / limite 75000.0 mm. Fajas principales: 35680.0 mm entre ejes.


Criterios adoptados para geometria P: carbon fino humedo 0,85 t/m3; reposo 45-50 grados; paredes de chutes de carbon minimo 60 grados. Los cuerpos documentados se conservan; nuevos mecanismos, bancadas y conexiones son propuestas P.

PLANTA BRIQUETADORA / CONFIGURADOR 3D

R18 / TOLVA DE CARBÓN / VISTAS 1:25


PLANTA BRIQUETADORA · R18 | 2026-10-19 | A1 horizontal - milímetros

LATERAL / 1:25

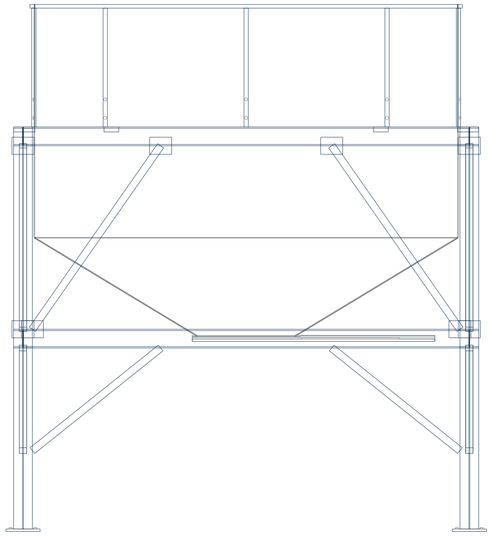


3923.0 envolvente P/R

SUPERIOR / 1:25

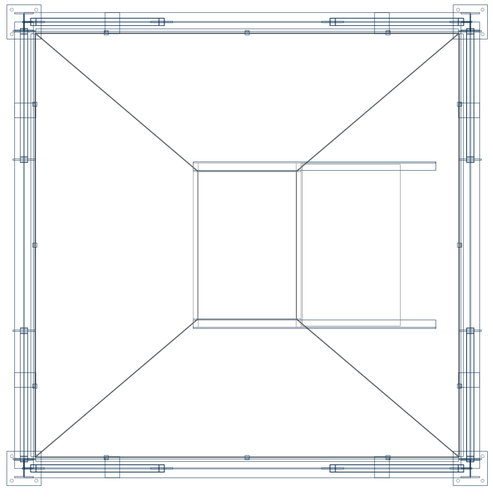

FRONTAL / 1:25

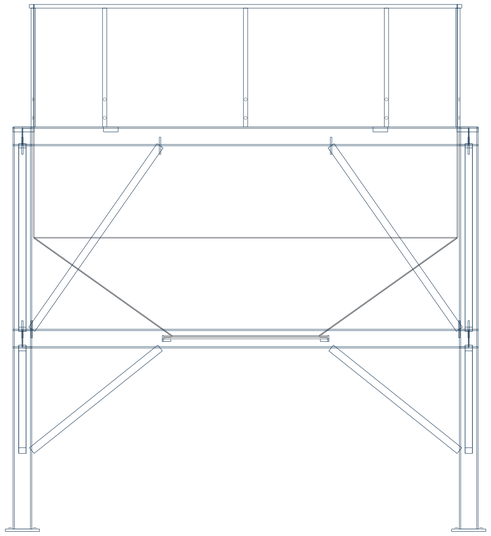

3923.0 envolvente P/R

Cuerpo nominal 3450.0 x 3450.0 x 2700.0 mm O. Apoyo de equipo +0.0 mm P. Posicion X/Y: 0.0 / 0.0 mm.

Tolva fabricada sin pedestal. Boca3450x3450 y salida1200x800 conservadas. C01 bajo compuerta sustituye solo el alimentador P04 adaptado.


O: documentado P: propuesto R: referencial / pendiente de fabricante. Geometría de implantación; no apta para fabricación sin validación.

PLANTA BRIQUETADORA / CONFIGURADOR 3D


R18 / DOSIFICADOR DE AGLOMERANTE / VISTAS 1:20

PLANTA BRIQUETADORA · R18 | 2026-10-19 | A1 horizontal - milímetros


LATERAL / 1:20

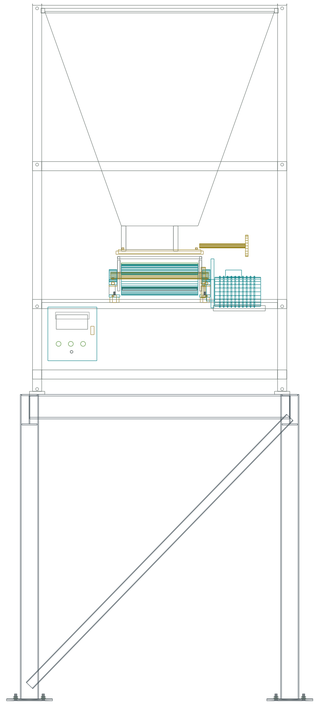

FRONTAL / 1:20

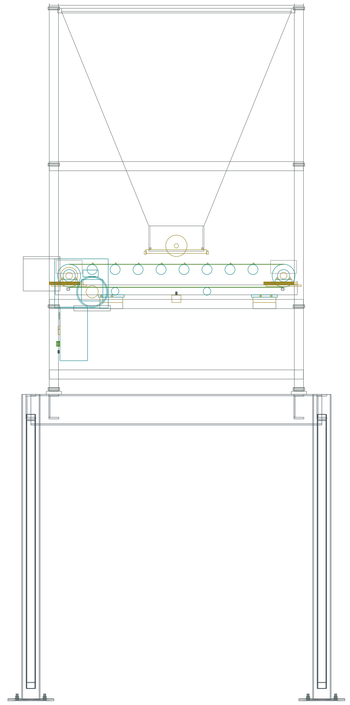

SUPERIOR / 1:20

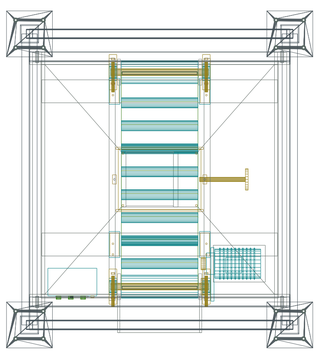

Cuerpo nominal 1700.0 x 1700.0 x 2600.0 mm O. Apoyo de equipo +2000.0 mm P. Posicion X/Y: 12419.5 / 2900.0 mm.

Aglomerante directo a mezcladora por transferencia solida o sistema liquido independiente. Conexiones separadas del pesaje.


O: documentado P: propuesto R: referencial / pendiente de fabricante. Geometría de implantación; no apta para fabricación sin validación.

PLANTA BRIQUETADORA / CONFIGURADOR 3D


R18 / MEZCLADORA DE DOBLE EJE / VISTAS 1:20

PLANTA BRIQUETADORA · R18 | 2026-10-19 | A1 horizontal - milímetros


LATERAL / 1:20

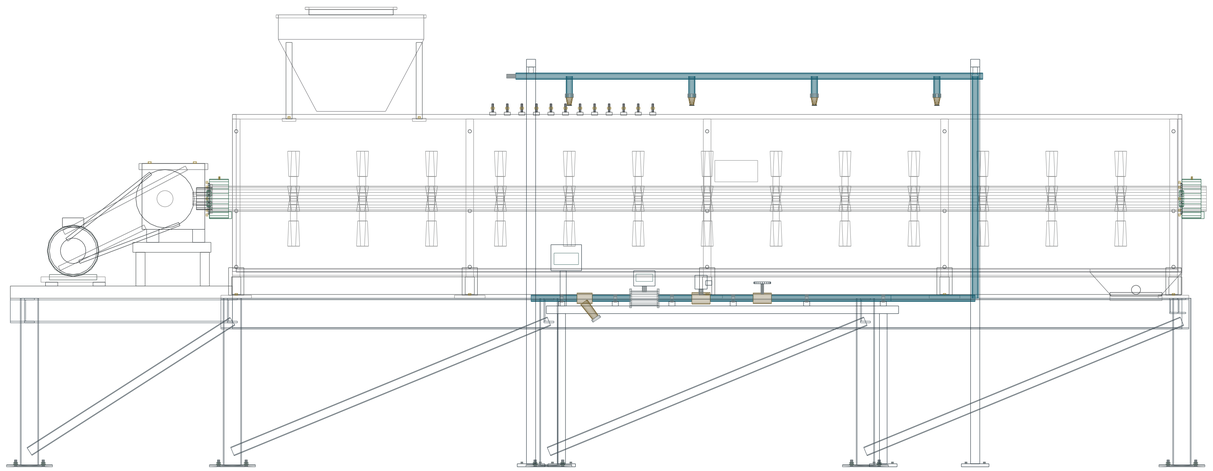

FRONTAL / 1:20

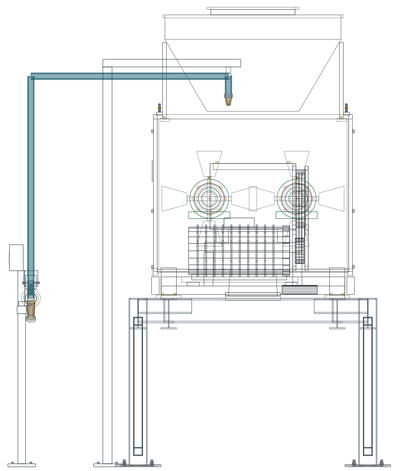

SUPERIOR / 1:20

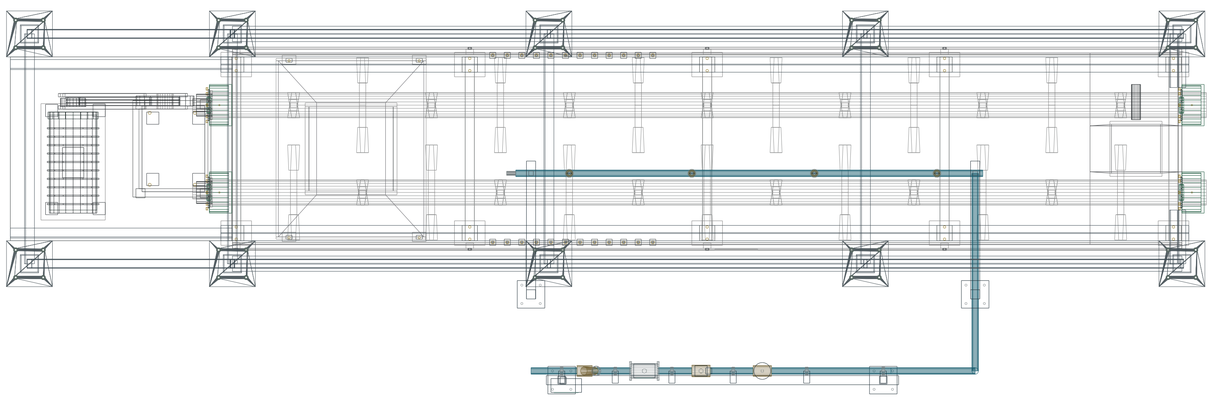

Cuerpo nominal 6200.0 x 1300.0 x 1200.0 mm O. Apoyo de equipo +1100.0 mm P. Posicion X/Y: 10569.5 / 0.0 mm.

Entrada de agua y aglomerante directa al cuerpo. Filtro Y, medicion, solenoide NC y regulacion manual. Descarga con registro y faldones a C02.


O: documentado P: propuesto R: referencial / pendiente de fabricante. Geometría de implantación; no apta para fabricación sin validación.

PLANTA BRIQUETADORA / CONFIGURADOR 3D

R18 / BRIQUETADORA / VISTAS 1:20


PLANTA BRIQUETADORA · R18 | 2026-10-19 | A1 horizontal - milímetros

LATERAL / 1:20

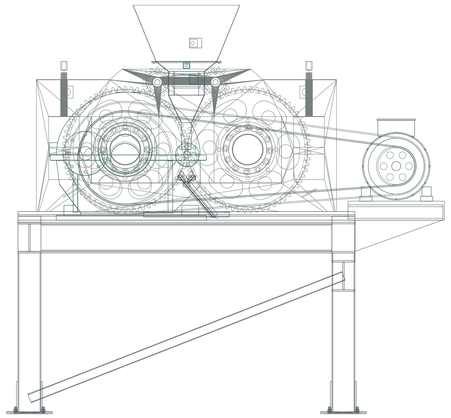


2860.0 envolvente P/R

FRONTAL / 1:20

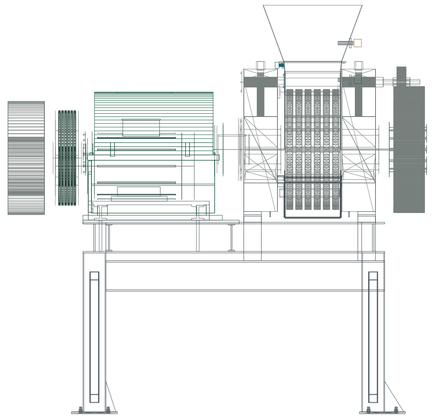

2734.0 envolvente P/R

SUPERIOR / 1:20

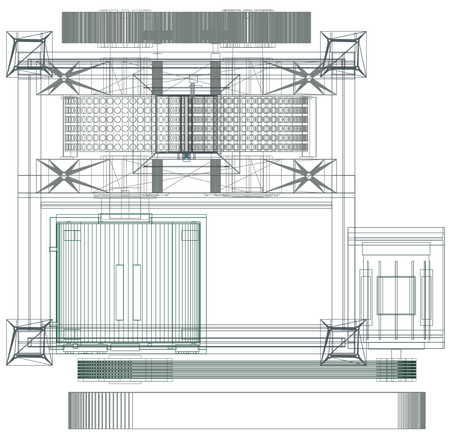

Cuerpo nominal 2200.0 x 1970.0 x 2300.0 mm O. Apoyo de equipo +0.0 mm P. Posicion X/Y: 24628.2 / -495.0 mm.

Cuello repartidor entre adaptador y rodillos, sensor de nivel y registro. Recepcion revestida y cassette B500 conservan componentes rigidos; adaptaciones inferiores P.


O: documentado P: propuesto R: referencial / pendiente de fabricante. Geometría de implantación; no apta para fabricación sin validación.

PLANTA BRIQUETADORA / CONFIGURADOR 3D


R18 / SECADOR DE SEIS NIVELES / VISTAS 1:50

PLANTA BRIQUETADORA · R18 | 2026-10-19 | A1 horizontal - milímetros


LATERAL / 1:50

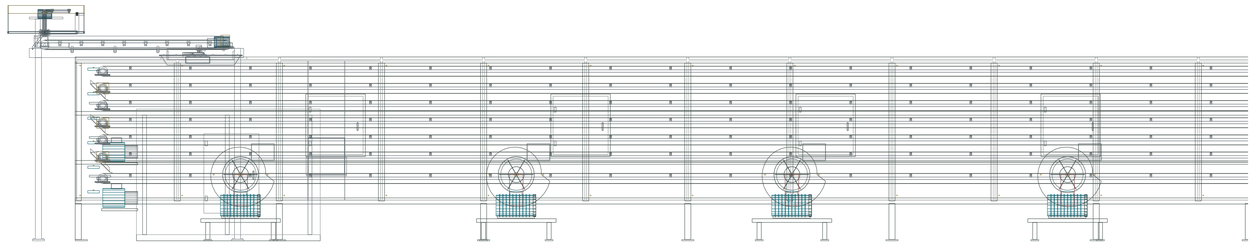

FRONTAL / 1:50

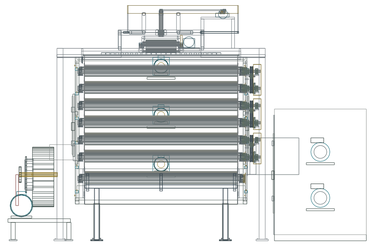

SUPERIOR / 1:50

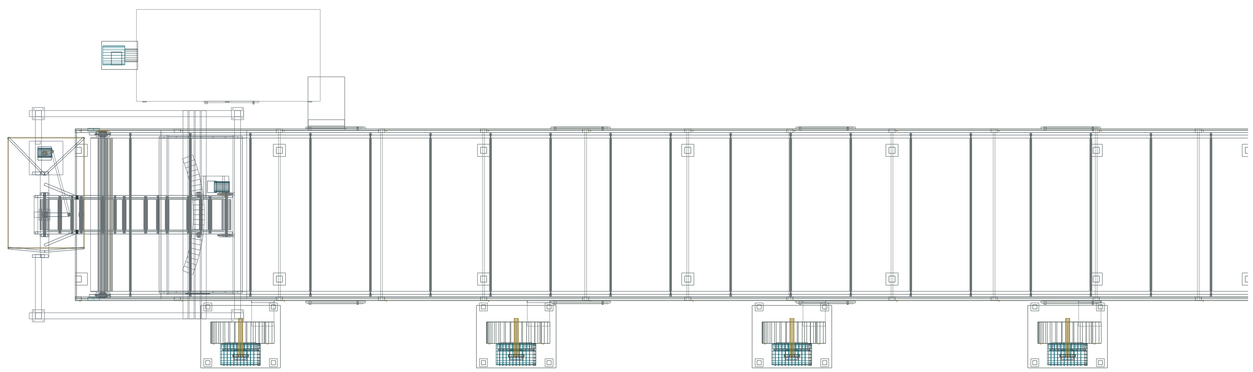

Cuerpo nominal 20000.0 x 2800.0 x 3000.0 mm O. Apoyo de equipo +0.0 mm P. Posicion X/Y: 37717.1 / 0.0 mm.

Cuerpo20000x2800x3000 apoyado al piso. Repartidor y ventiladores acotados aparte. Chuta ancha2500 hacia C04 transversal; sin embudo profundo.


O: documentado P: propuesto R: referencial / pendiente de fabricante. Geometría de implantación; no apta para fabricación sin validación.

PLANTA BRIQUETADORA / CONFIGURADOR 3D


R18 / CARBÓN · COMPUERTA / ALIMENTADOR C01 / DETALLE 1:20

PLANTA BRIQUETADORA · R18 | 2026-10-19 | A1 horizontal - milímetros

LATERAL / 1:20

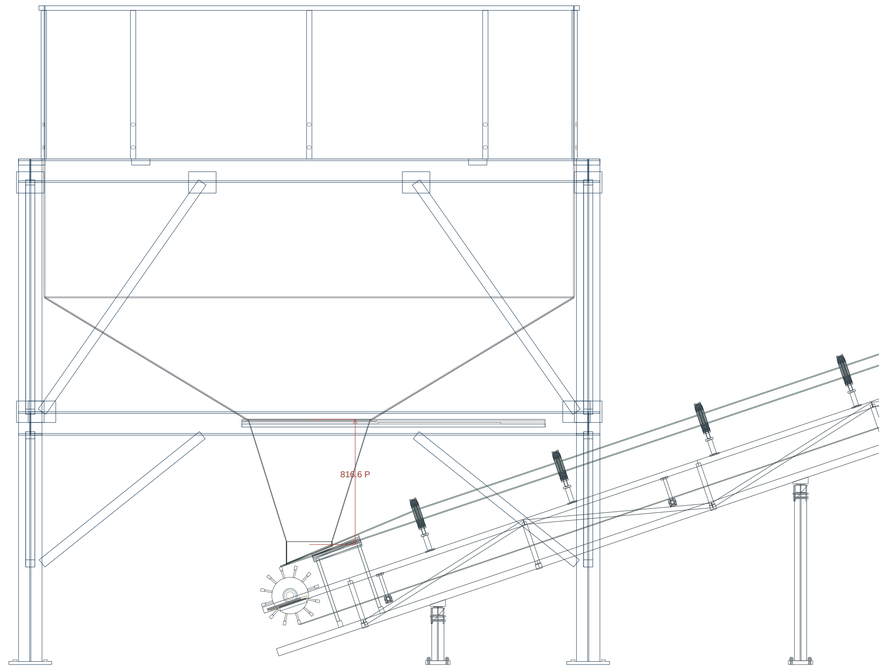

SUPERIOR / 1:20

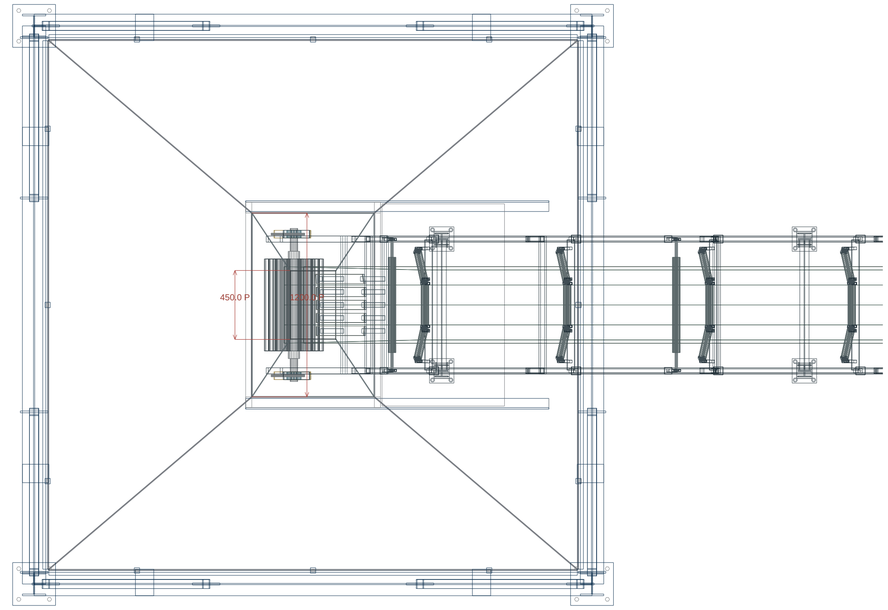

Origen desde NPT +1600.0 mm / recepcion +783.4 mm. Desnivel entre referencias 816.6 mm. Desplazamiento horizontal 0.0 mm.

Abertura de origen 800.0 x 1200.0 mm / receptora 300.0 x 450.0 mm P. Centros, caras de banda y bocas se acotan de manera independiente.

Tolva fabricada sin pedestal. C01 alimenta bajo compuerta; campana 1200 a 450 mm, cama de impacto y faldones. Accionamiento sujeto a carga bajo tolva; no equivale automáticamente al servicio anterior.


O: documentado P: propuesto R: referencial / pendiente de fabricante. Geometría de implantación; no apta para fabricación sin validación.

PLANTA BRIQUETADORA / CONFIGURADOR 3D


R18 / AGLOMERANTE DIRECTO A MEZCLADORA / DETALLE 1:20

PLANTA BRIQUETADORA · R18 | 2026-10-19 | A1 horizontal - milímetros

LATERAL / 1:20

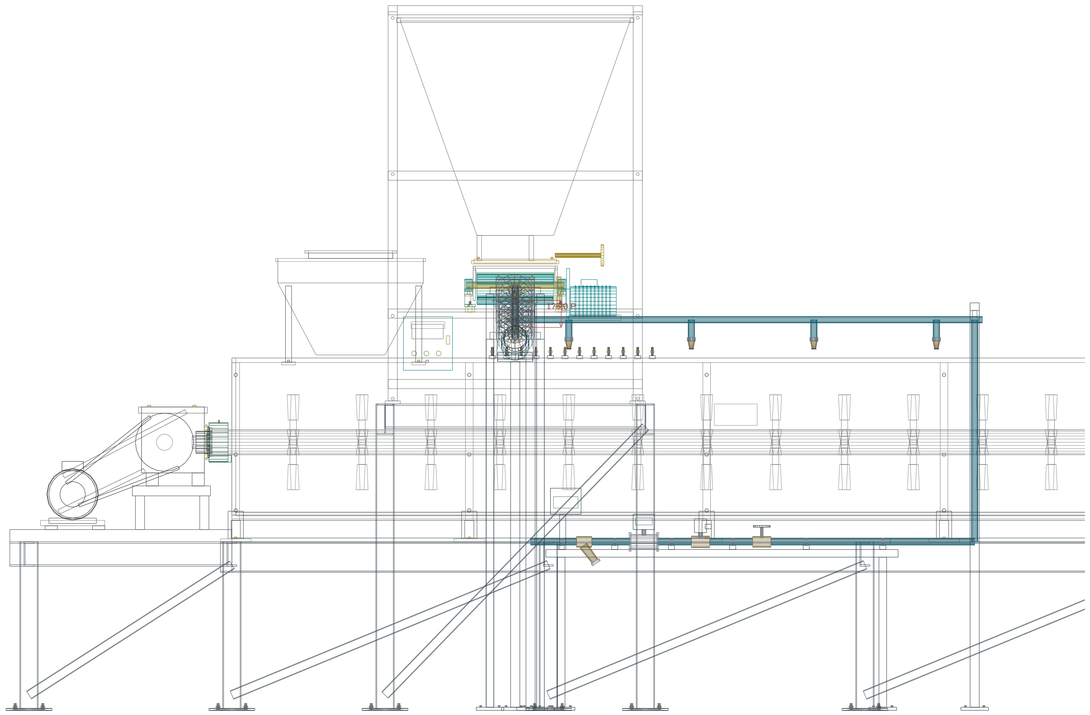

SUPERIOR / 1:20

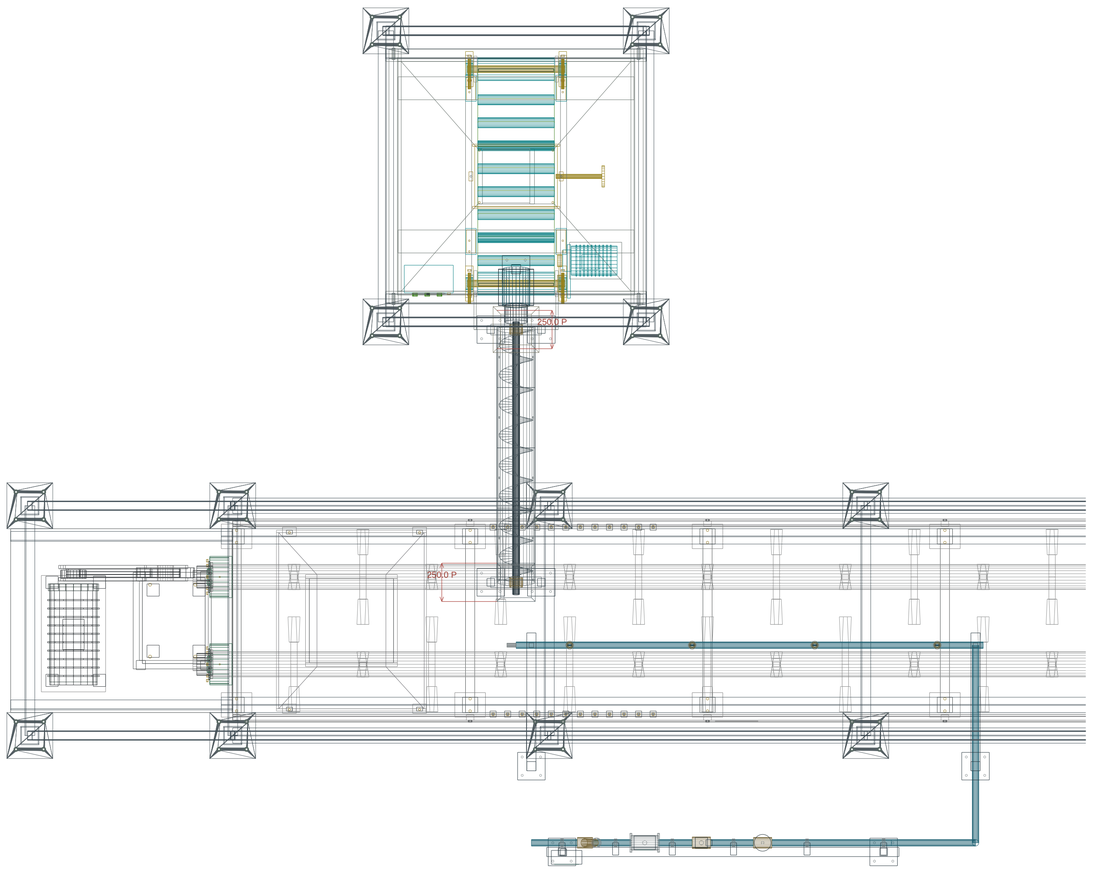

Origen desde NPT +2675.0 mm / recepcion +2500.0 mm. Desnivel entre referencias 175.0 mm. Desplazamiento horizontal 1650.0 mm.

Abertura de origen 250.0 x 250.0 mm / receptora 250.0 x 250.0 mm P. Centros, caras de banda y bocas se acotan de manera independiente.


Solucion mecanica propuesta P; medidas generadas de la geometria compartida del visor.

PLANTA BRIQUETADORA / CONFIGURADOR 3D


R18 / MEZCLADORA / C02 / DETALLE 1:20

PLANTA BRIQUETADORA · R18 | 2026-10-19 | A1 horizontal - milímetros

LATERAL / 1:20

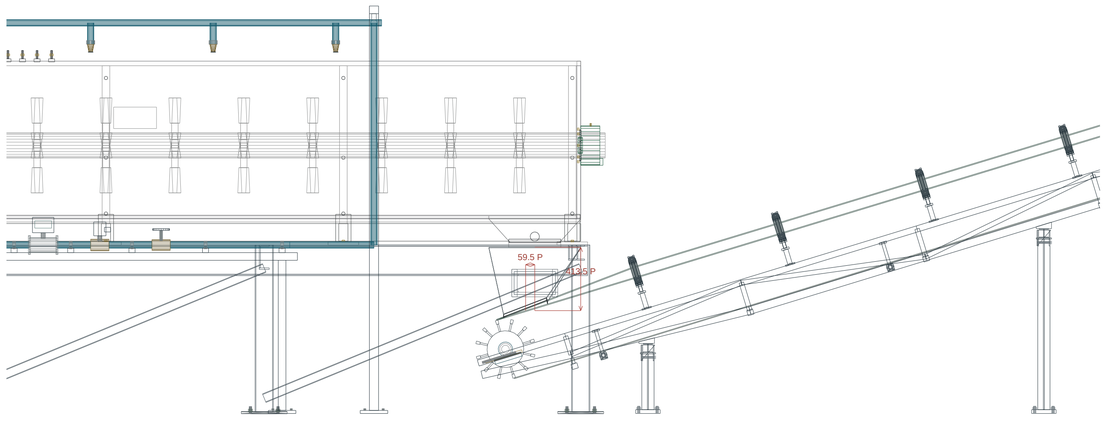

SUPERIOR / 1:20

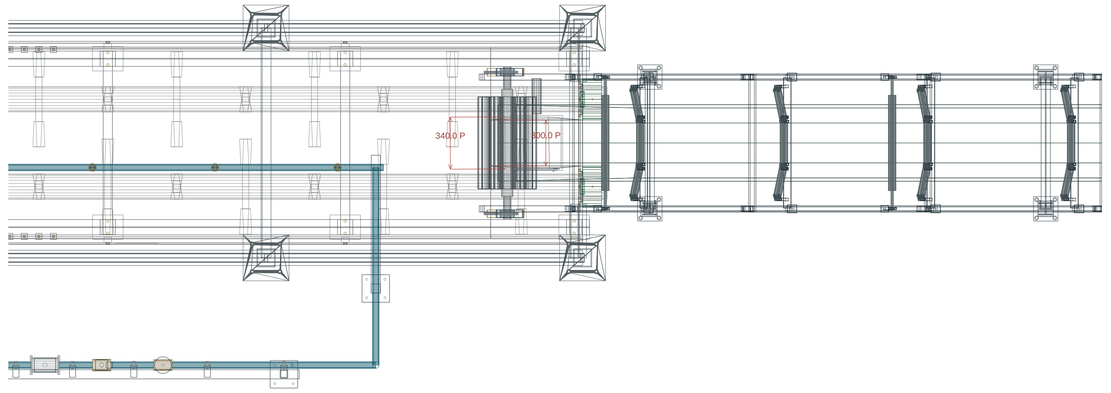

Origen desde NPT +1085.0 mm / recepcion +671.5 mm. Desnivel entre referencias 413.5 mm. Desplazamiento horizontal 59.5 mm.

Abertura de origen 600.0 x 300.0 mm / receptora 300.0 x 340.0 mm P. Centros, caras de banda y bocas se acotan de manera independiente.


Chute P con registro y faldones; altura libre mayor de300mm.

PLANTA BRIQUETADORA / CONFIGURADOR 3D


R18 / C02 / BRIQUETADORA / DETALLE 1:20

PLANTA BRIQUETADORA · R18 | 2026-10-19 | A1 horizontal - milímetros

LATERAL / 1:20

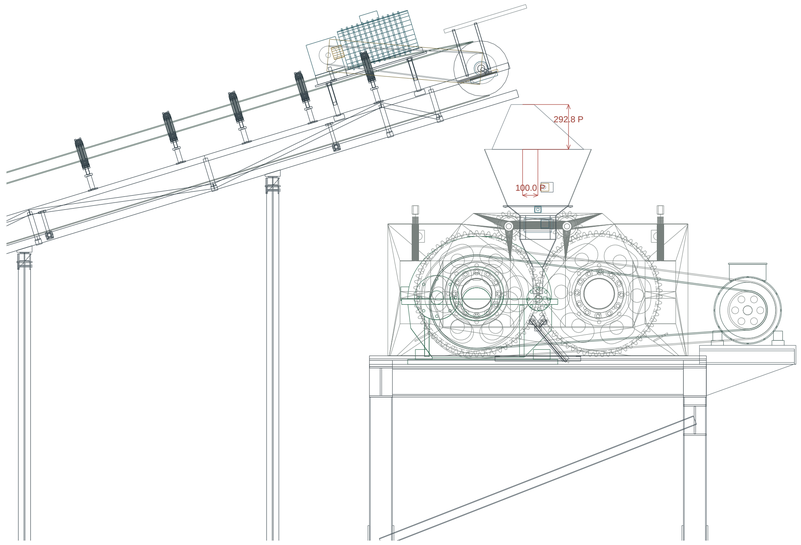

SUPERIOR / 1:20

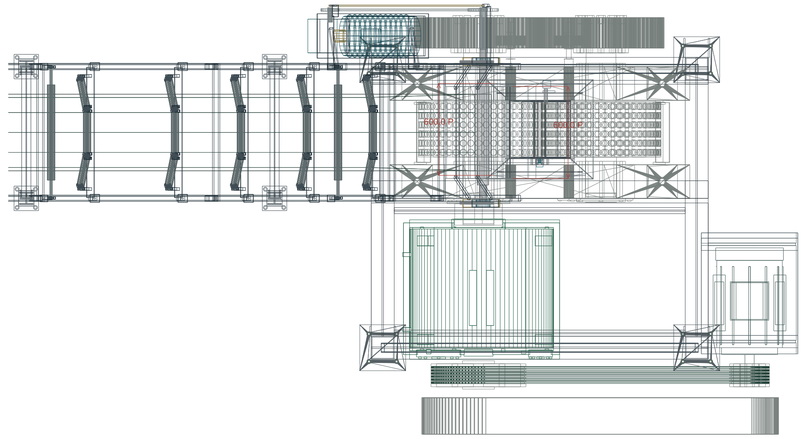

Origen desde NPT +2960.1 mm / recepcion +2667.3 mm. Desnivel entre referencias 292.8 mm. Desplazamiento horizontal 102.0 mm.

Abertura de origen 150.0 x 600.0 mm / receptora 600.0 x 600.0 mm P. Centros, caras de banda y bocas se acotan de manera independiente.

Cuello575mm P con transición conformada400mm y aproximación abierta175mm, sensor y registro.


O: documentado P: propuesto R: referencial / pendiente de fabricante. Geometría de implantación; no apta para fabricación sin validación.

PLANTA BRIQUETADORA / CONFIGURADOR 3D


R18 / BRIQUETADORA / C05 · CASSETTE PRÓXIMO P / DETALLE 1:20

PLANTA BRIQUETADORA · R18 | 2026-10-19 | A1 horizontal - milímetros

LATERAL / 1:20

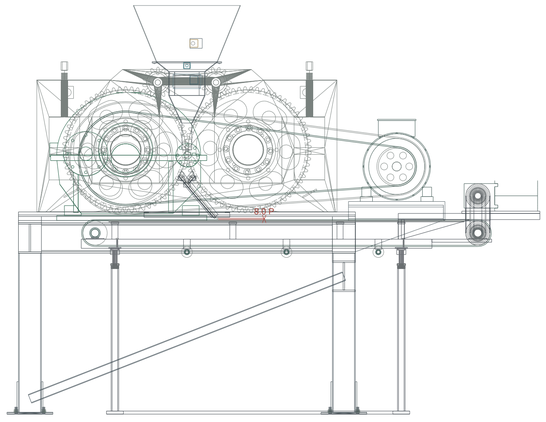

SUPERIOR / 1:20

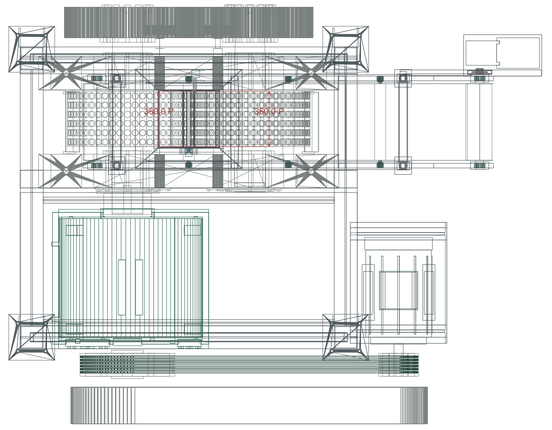

Origen desde NPT +1278.0 mm / recepcion +1270.0 mm. Desnivel entre referencias 8.0 mm. Desplazamiento horizontal 0.0 mm.

Abertura de origen 80.0 x 360.0 mm / receptora 80.0 x 360.0 mm P. Centros, caras de banda y bocas se acotan de manera independiente.

P: tangente de desprendimiento15° adoptada; dos labios50° y canal común50°, goma10/UHMW8, salida8sobrebanda.


O: documentado P: propuesto R: referencial / pendiente de fabricante. Geometría de implantación; no apta para fabricación sin validación.

PLANTA BRIQUETADORA / CONFIGURADOR 3D


R18 / C05 / C03 · TRANSFERENCIA TRANSVERSAL PROPUESTA 500 MM / DETALLE 1:20

PLANTA BRIQUETADORA · R18 | 2026-10-19 | A1 horizontal - milímetros

LATERAL / 1:20

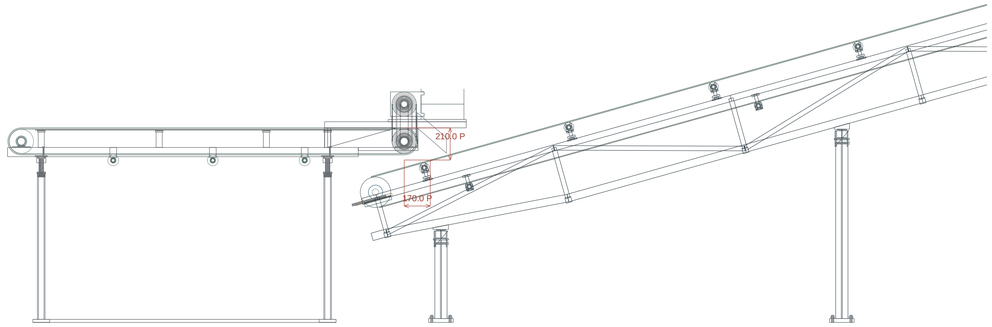

SUPERIOR / 1:20

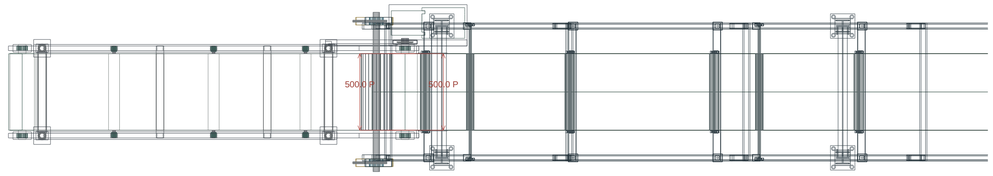

Origen desde NPT +1270.0 mm / recepcion +1060.0 mm. Desnivel entre referencias 210.0 mm. Desplazamiento horizontal 170.0 mm.

Abertura de origen 220.0 x 500.0 mm / receptora 220.0 x 500.0 mm P. Centros, caras de banda y bocas se acotan de manera independiente.


Cola C03 a +850 mm P y recepción 170 mm después de la cabeza C05; longitud y cabeza conservadas. Guías laterales abiertas, sin fondo ni placas transversales. Trayectoria, tamaño y resistencia de briqueta pendientes de ensayo.

PLANTA BRIQUETADORA / CONFIGURADOR 3D


R18 / C03 / COLA FIJA REPARTIDOR / DETALLE 1:20

PLANTA BRIQUETADORA · R18 | 2026-10-19 | A1 horizontal - milímetros

LATERAL / 1:20

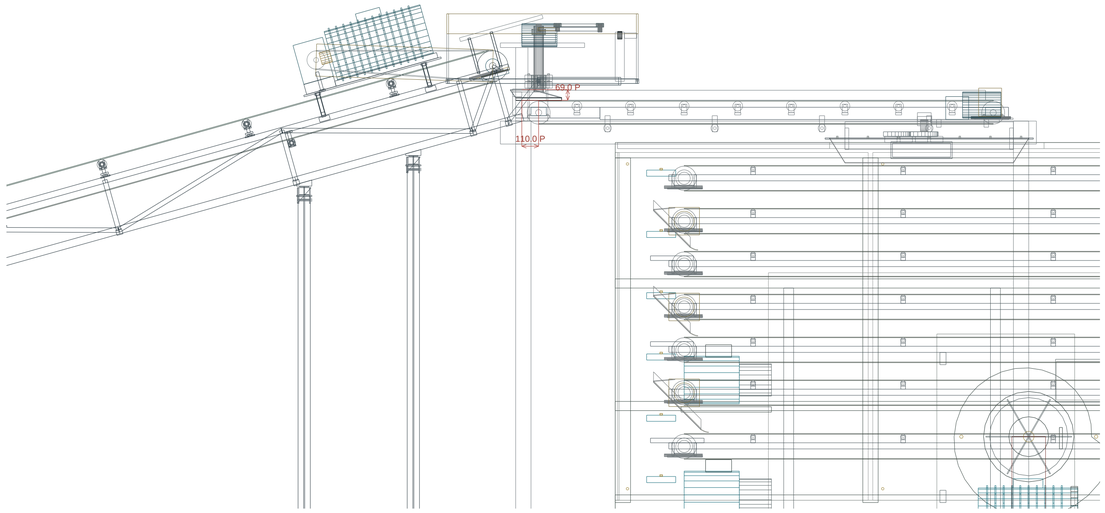

SUPERIOR / 1:20

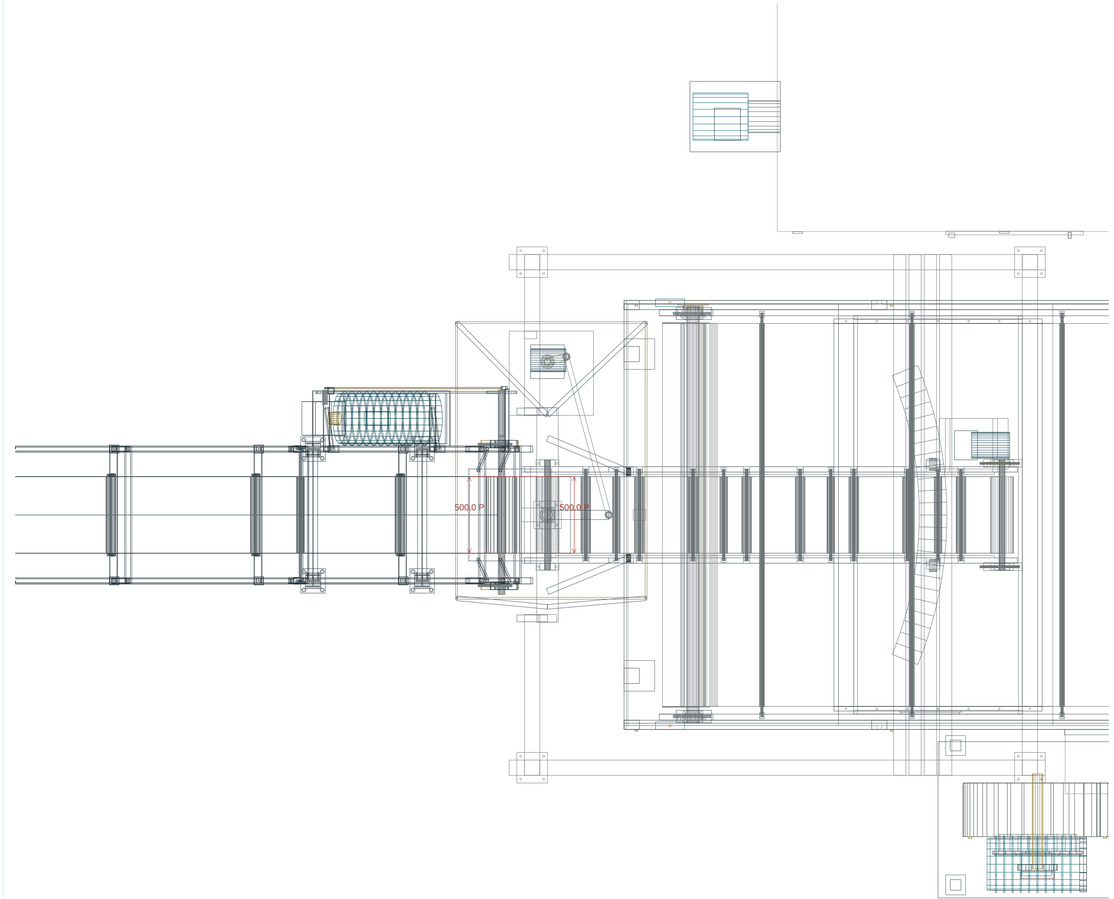

Origen desde NPT +3345.0 mm / recepcion +3276.0 mm. Desnivel entre referencias 69.0 mm. Desplazamiento horizontal 110.0 mm.

Abertura de origen 150.0 x 500.0 mm / receptora 300.0 x 500.0 mm P. Centros, caras de banda y bocas se acotan de manera independiente.

Solucion mecanica propuesta P; medidas generadas de la geometria compartida del visor.


O: documentado P: propuesto R: referencial / pendiente de fabricante. Geometría de implantación; no apta para fabricación sin validación.

PLANTA BRIQUETADORA / CONFIGURADOR 3D


R18 / REPARTIDOR OSCILANTE / SECADOR / DETALLE 1:20

PLANTA BRIQUETADORA · R18 | 2026-10-19 | A1 horizontal - milímetros

LATERAL / 1:20

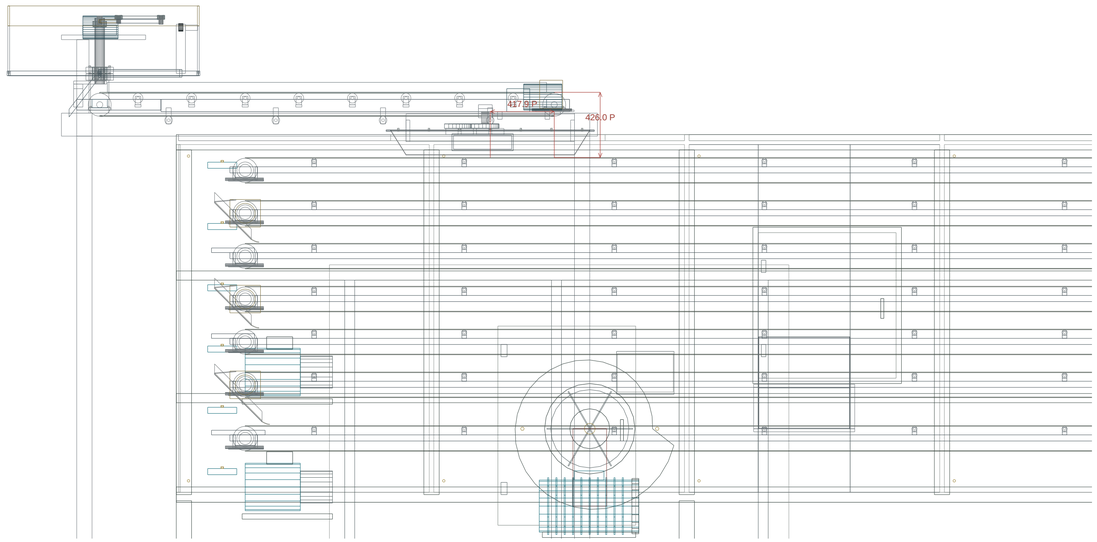

SUPERIOR / 1:20

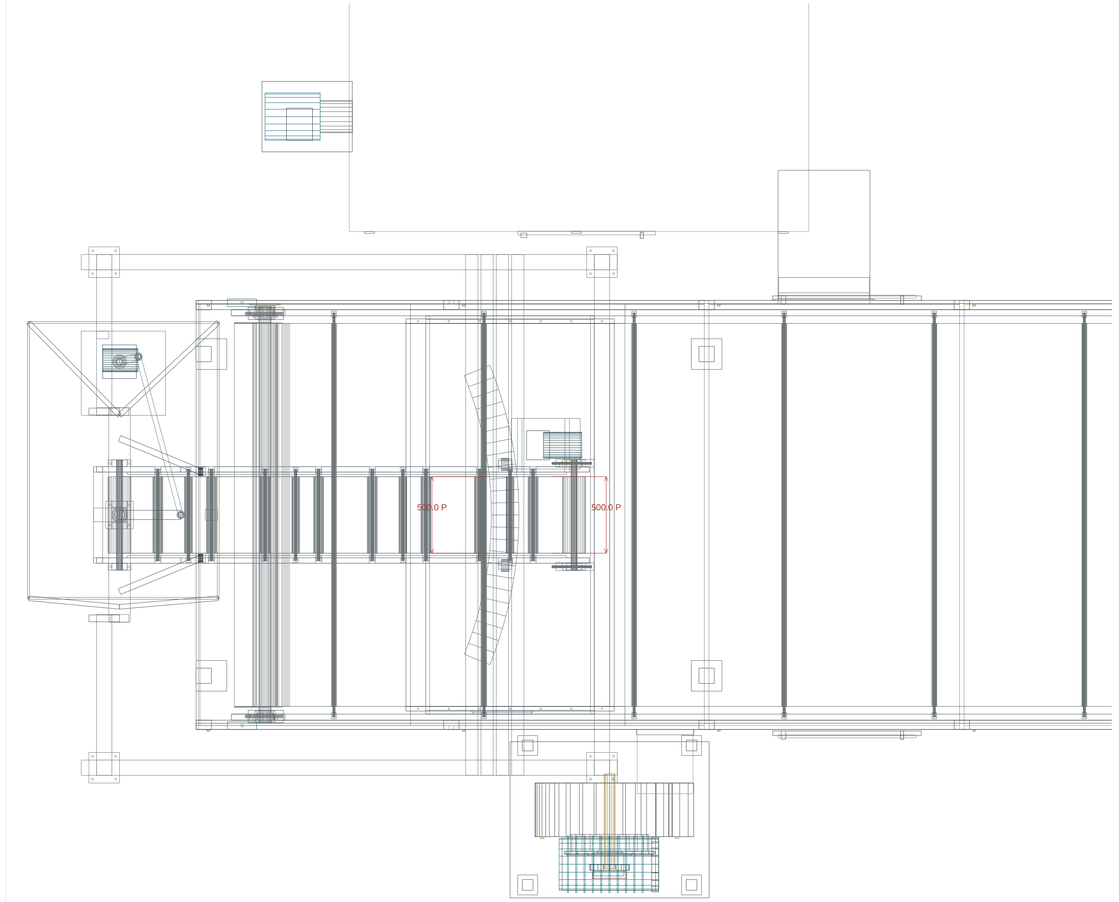

Origen desde NPT +3276.0 mm / recepcion +2850.0 mm. Desnivel entre referencias 426.0 mm. Desplazamiento horizontal 417.9 mm.

Abertura de origen 300.0 x 500.0 mm / receptora 300.0 x 500.0 mm P. Centros, caras de banda y bocas se acotan de manera independiente.

P: cuello de acople con brida y registro al nivel1; repartidor±20°.


O: documentado P: propuesto R: referencial / pendiente de fabricante. Geometría de implantación; no apta para fabricación sin validación.

PLANTA BRIQUETADORA / CONFIGURADOR 3D


R18 / C06 / CHUTA2500 / COLECTORA TRANSVERSAL C04 / DETALLE 1:20

PLANTA BRIQUETADORA · R18 | 2026-10-19 | A1 horizontal - milímetros

LATERAL / 1:20

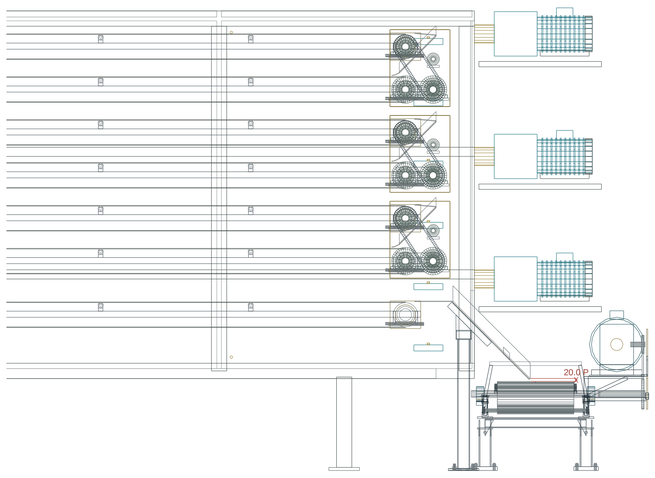

SUPERIOR / 1:20

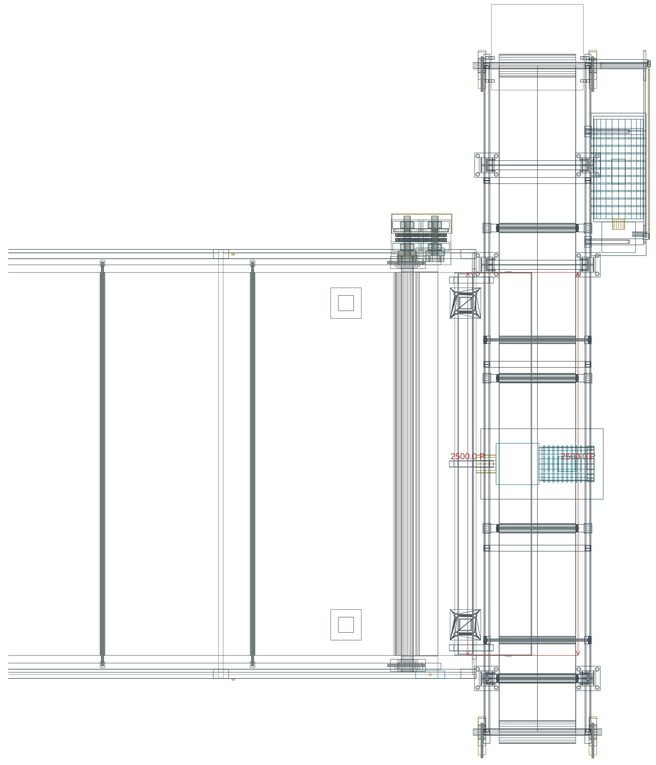

Origen desde NPT +601.0 mm / recepcion +581.0 mm. Desnivel entre referencias 20.0 mm. Desplazamiento horizontal 0.0 mm.

Abertura de origen 120.0 x 2500.0 mm / receptora 120.0 x 2500.0 mm P. Centros, caras de banda y bocas se acotan de manera independiente.


Chuta45° ancha; material conserva posición transversal. C04 recibe u500–3000; no reducción a garganta200 ni foso.

O: documentado P: propuesto R: referencial / pendiente de fabricante. Geometría de implantación; no apta para fabricación sin validación.

PLANTA BRIQUETADORA / CONFIGURADOR 3D

R18 / AGUA, AGLOMERANTE Y CONTROL DE RECORRIDO

SUMINISTRO DIRECTO A MEZCLADORA / DOS CIRCUITOS INDEPENDIENTES

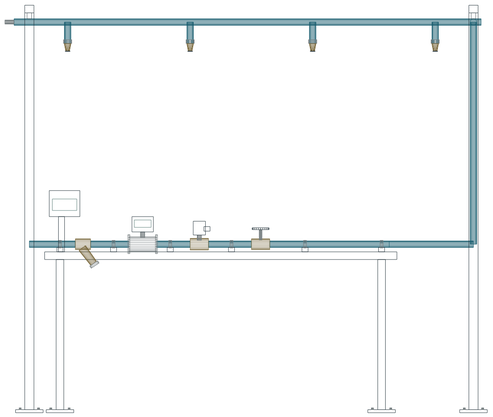

Agua: filtro Y / caudalimetro totalizador / solenoide normalmente cerrada / valvula reguladora manual / manifold con boquillas en abanico.

Aglomerante: alimentacion directa por boca propia para solido o colector independiente para liquido. El agua de proceso y el aglomerante no se mezclan dentro de las tuberias.

Por cargas: volumen acumulado en litros y cierre al alcanzar consigna. En continuo: caudal en L/min medido y ajuste manual. La aplicacion conserva consignas; no acciona valvulas reales.

Recepcion de briquetas: recorrido continuo C05-C03 en el sentido del transporte, sin retroceso ni elevacion artificial. Repartidor transversal representado como mecanismo P.


Adaptaciones mecanicas P. Perfiles, espesores y revestimientos son decisiones geometricas; el modelo no incorpora calculo de resistencia ni certificacion de fabricante.

PLANTA BRIQUETADORA / CONFIGURADOR 3D

R15 / SECADOR / SEIS PISOS UTILES Y TRANSFERENCIAS ALTERNADAS P

PLANTA BRIQUETADORA · R18 | 2026-10-19 | A1 horizontal - milímetros

LATERAL INTERIOR / 1:50 / CARCASA EXCLUIDA PARA MOSTRAR EL RECORRIDO

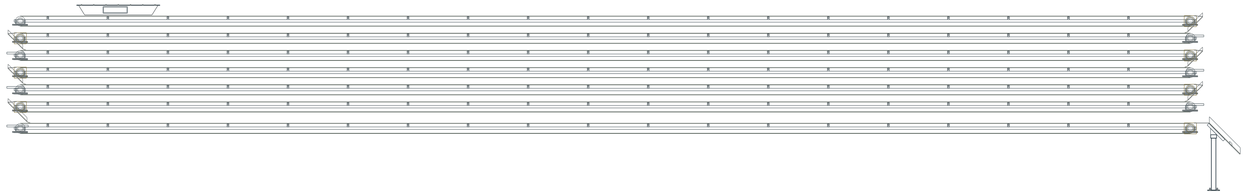





N1 / Z local +2850.0
N2 / Z local +2570.0
N3 / Z local +2290.0
N4 / Z local +2010.0
N5 / Z local +1730.0
N6 / Z local +1450.0

Seis pisos de secado: paso vertical de 280 mm entre superficies utiles. Cinco chutas de cambio a 45 grados y pestañas deflectoras revestidas. El cuello superior registrado acopla la recepcion exterior al primer piso.

EXTREMO DE TRANSFERENCIA / 1:10

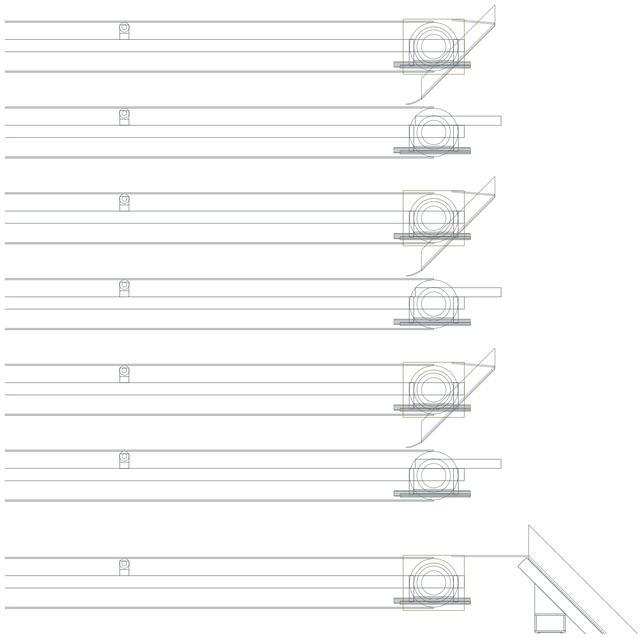

CONVERGENCIA Y COLECTORA C06 / 1:20

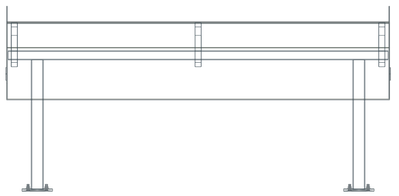


C06 evacua el sexto piso hacia chuta ancha2500 a45 grados. C04B500 recibe transversalmente sin garganta200 ni foso. Secador apoyado al piso; C06 no es un septimo piso de secado.

PLANTA BRIQUETADORA / CONFIGURADOR 3D


R15 / PRENSA A C05 / DESPRENDIMIENTO ADOPTADO Y ZAPATAS REVESTIDAS P

PLANTA BRIQUETADORA · R18 | 2026-10-19 | A1 horizontal - milímetros

RODILLOS Y RECEPCION / LATERAL 1:5

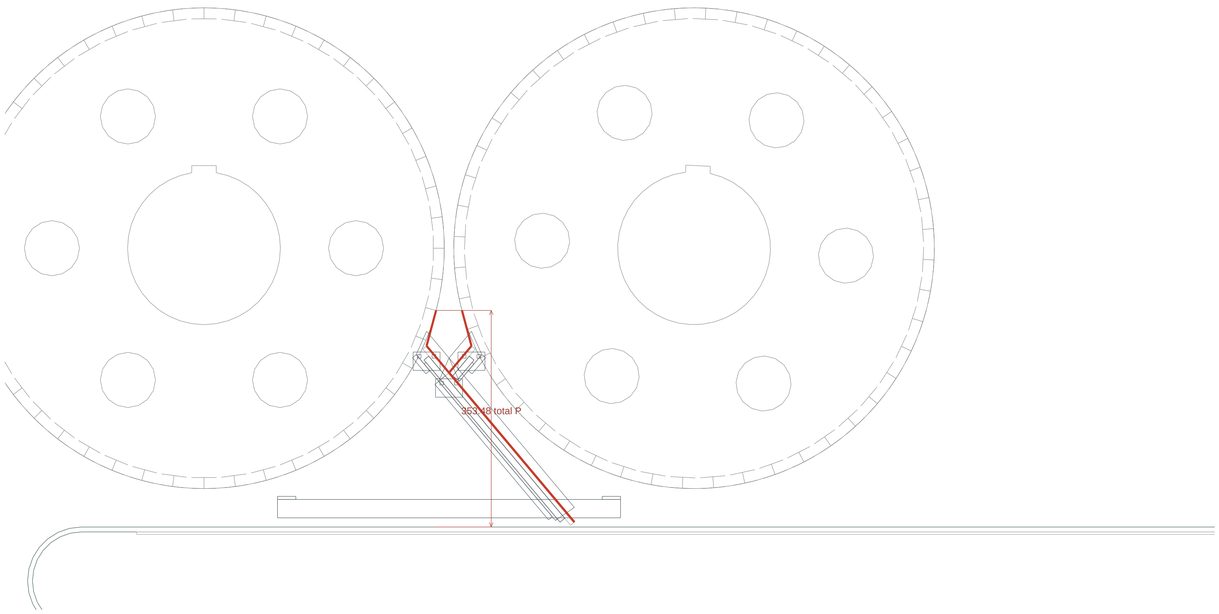

CAPTURA Y CANAL COMUN / LATERAL 1:2

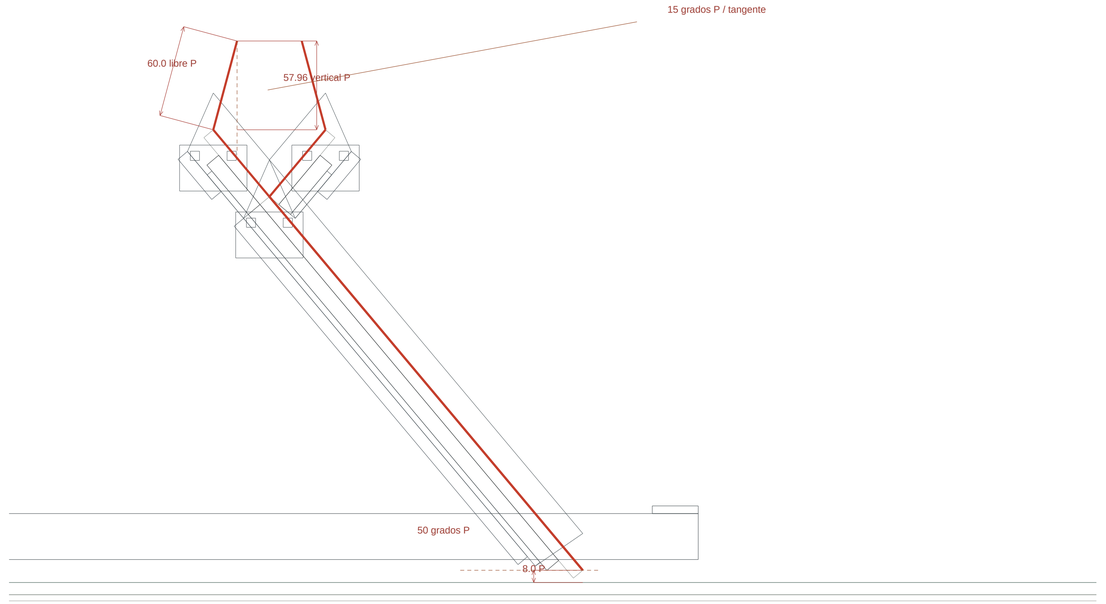

Recorrido adoptado P

Tangente descendente adoptada P: 15 grados de la vertical; posicion radial a 75 grados. Tramo libre sobre la tangente 60.0 mm / descenso vertical 57.96 mm. Desnivel TOTAL hasta C05 353.48 mm: incluye el recorrido guiado, no es caida libre.

Dos labios de captura a 50.0 grados confluyen en un canal comun a 50.0 grados. UHMWPE 8 mm / goma 10 mm / acero 4 mm. Salida 8.0 mm sobre C05; placas, soportes y tornillos independientes.

C05 conserva tambores, motor, ancho y longitud. El angulo de desprendimiento es un criterio geometrico P adoptado para esta revision; no es una medicion del producto.


O: documentado P: propuesto R: referencial / pendiente de fabricante. Geometría de implantación; no apta para fabricación sin validación.

PLANTA BRIQUETADORA / CONFIGURADOR 3D


R15 / REPARTIDOR OSCILANTE B500 / PIVOTE Y BIELA-MANIVELA P

PLANTA BRIQUETADORA · R18 | 2026-10-19 | A1 horizontal - milímetros

PLANTA DEL MECANISMO / 1:15

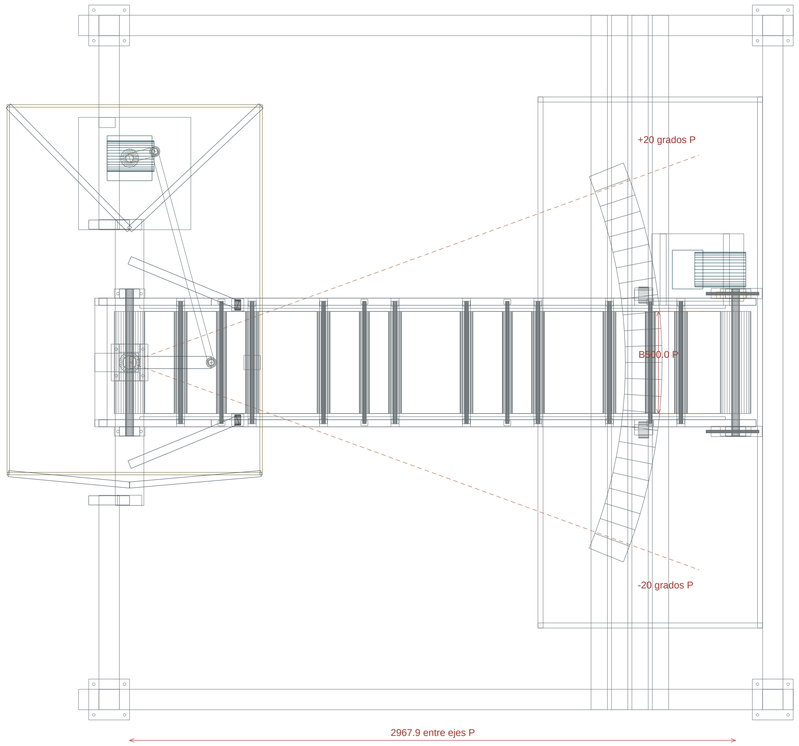

LATERAL Y APOYOS / 1:20

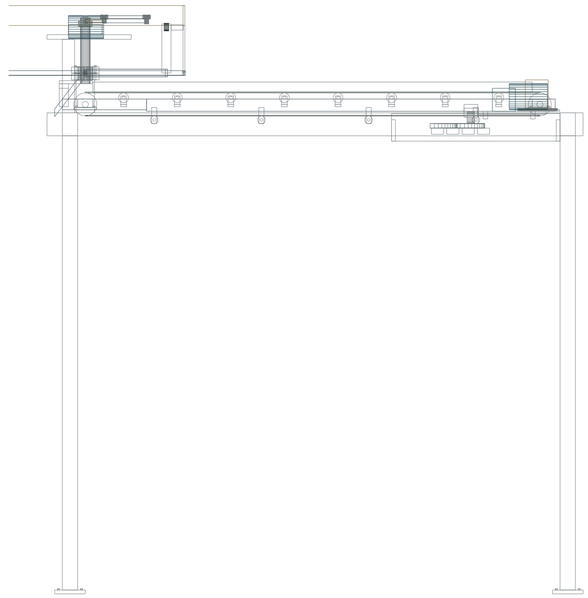

Banda 500 mm; entre ejes 2967.9 mm; barrido angular simetrico +/-20 grados. El pivote superior se apoya en dos alojamientos y un pasador vertical. Tensores, rodamientos, guardas laterales y topes se conservan como piezas rigidas.

Biela-manivela: radio 127.93 mm / biela 1069.41 mm / balancin 400.0 mm / distancia entre pivotes 1000.0 mm. Motorreductor ilustrativo 3.75 rpm. La animacion resuelve el mecanismo cerrado, no deforma las bielas.

Barrido del borde de banda sobre ancho util de 2500 mm. Posicion central representada en CAD; los extremos de carrera se identifican con topes mecanicos. Geometria y mecanismos nuevos clase P.

SESUVECA | PLANTA BRIQUETADORA | R18

01 | Comparacion R17 / R18 y restricciones de altura

Equipo	Base R17	Base R18	Posicion X R18	Criterio
tolva	900.0	0.0	0.000	Altura fija / datum bloqueado
dosificador	2000.0	2000.0	12419.529	Bancada ajustable
mezcladora	1100.0	1100.0	10569.529	Bancada ajustable
briquetadora	0.0	0.0	24628.187	Altura fija / datum bloqueado
secador	2200.0	0.0	37717.116	Altura fija / datum bloqueado

Cinta	L entre ejes	Pendiente	Giro planta	Cola Z	Cabeza Z	Clase
C01	9495.0	18.673470	0.0	450.000	3490.056	P
C02	9495.0	16.993636	0.0	420.000	3195.061	P
C05	2500.0	0.000000	0.0	1182.000	1182.000	P
C03	9840.0	15.623149	0.0	850.000	3500.000	P
C04	4350.0	0.000000	90.0	500.000	500.000	R


Suma de cinco cintas externas: 40.580 -> 35.680 m. Envolvente mecanica: 58.855 m. Envolvente con accesos: 61.117 x 7.850 m. Limite longitudinal: 75 m.

Las cotas geometricas y cantidades proceden de un mismo modelo R18. Las piezas fabricadas de tolva/prensa y el cuerpo del secador no se elevan para acomodar transportadores. C01 cambia de servicio: seleccion de carga y par pendiente antes de compra.

SESUVECA | PLANTA BRIQUETADORA | R18

02 | Tolva fabricada al piso y alimentador C01 directo

ALZADO LOCAL 1:10 / NPT z=0

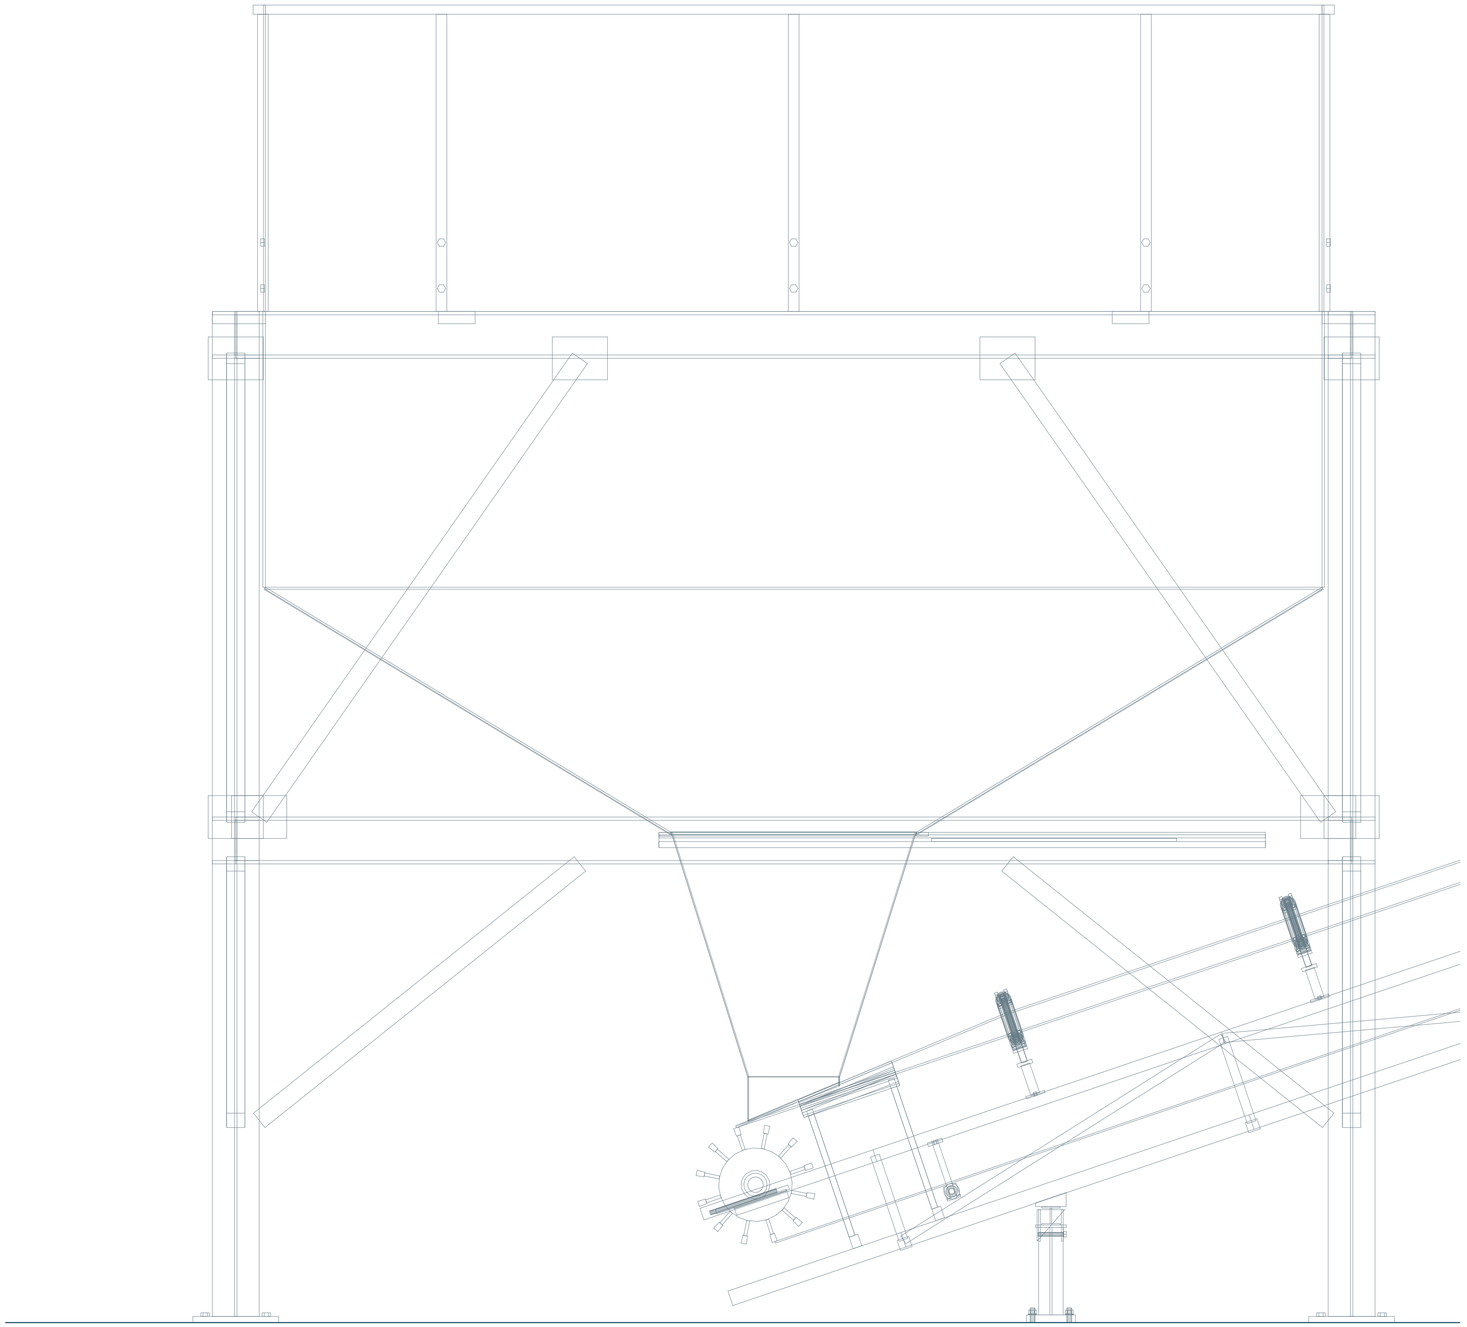

CRITERIOS DE LA ADAPTACION P

Se retira el alimentador P04 adaptado y su elevacion adicional900. La tolva fabricada conserva cuerpo, patas, boca3450x3450, salida1200x800 y altura montada interpretada4300 R.

C01 recibe bajo la compuerta de regulacion. Campana transversal1200 ->450, paredes aproximadamente65 grados, cama de impacto y faldones. Las caras del chute se generan hasta la superficie real de recepcion.


Paso regular de polines980 y bastidor1200 mas remate. Ejes, tambores, motor y rodamientos conservan dimensiones individuales. Se verifica separacion a patas y al piso incluyendo faldones.

El VFD ya previsto se conserva como arquitectura. La antigua potencia3kW es referencia P: el esfuerzo bajo columna de material y el arranque cargado requieren seleccion especifica del alimentador.

SESUVECA | PLANTA BRIQUETADORA | R18

03 | Prensa fija, recepcion proxima C05 y encuentro con C03

ALZADO LOCAL 1:10

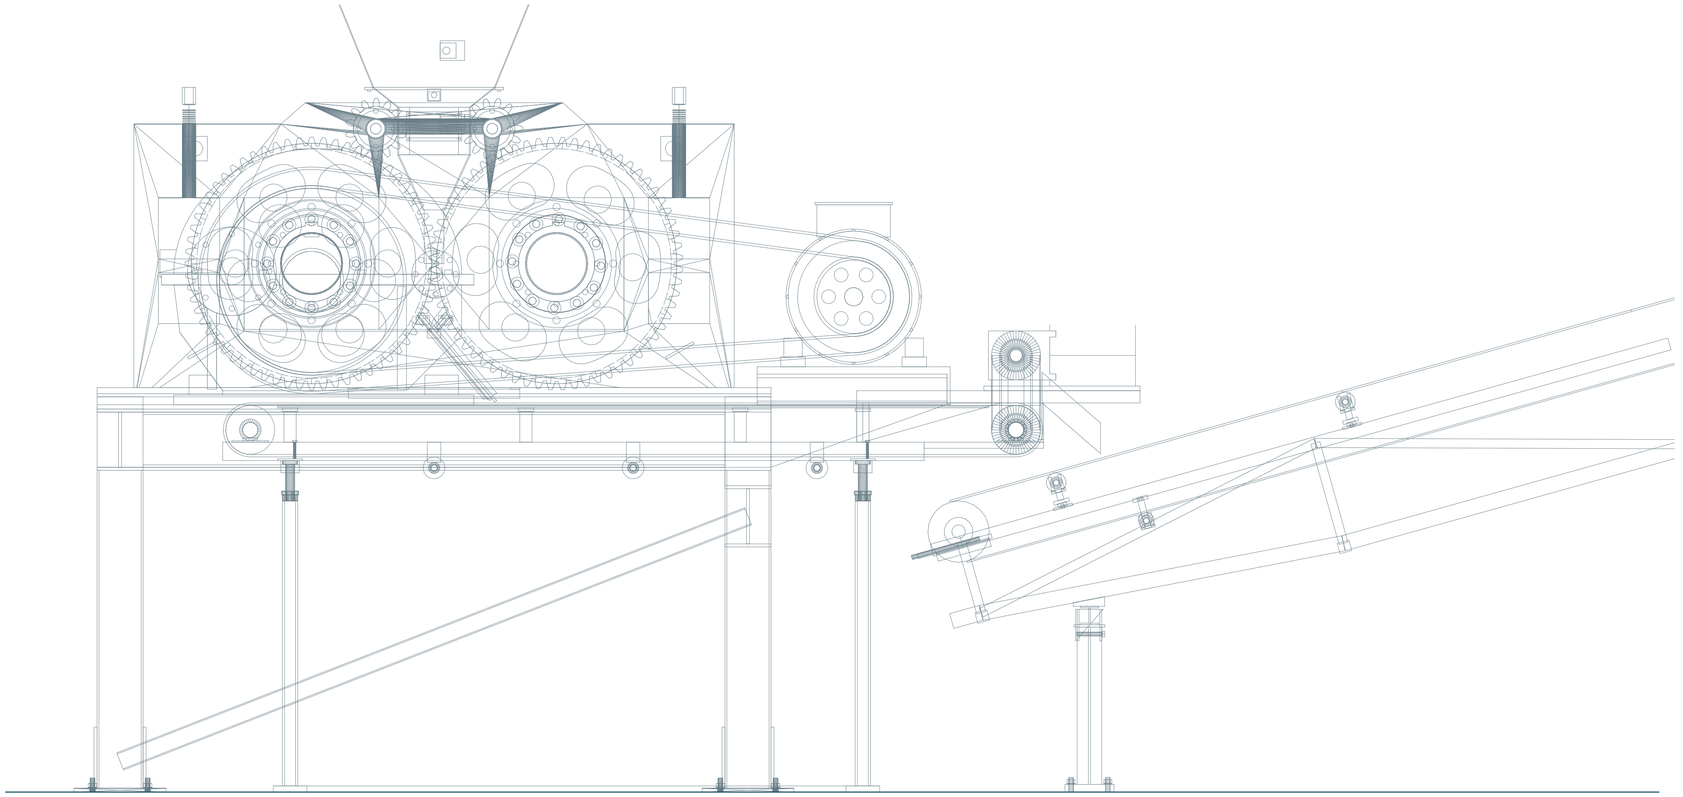

RECEPCION SIN ELEVAR PRENSA

Se conserva la posicion real de los rodillos, su altura y la trayectoria de desprendimiento15 grados. Chute50 grados con amortiguacion y salida a8mm de la banda C05.

C05: eje1182 y superficie1270 desde piso. Su conjunto rigido conserva motor, tambores y soporte propio; no se incrementa la caida de briqueta fresca.

C03 acortada a9840 entre ejes. Recepcion calculada sobre su banda inclinada: aproximadamente1060 desde piso. La bajante C05-C03 desciende aproximadamente210.


Interfaz	Salida Z	Recepcion Z	Caida entre referencias	Desfase horizontal
mix-C02	1085.000	671.498	413.502	59.493
C02-briq	2960.061	2667.250	292.811	101.980
briq-C05	1278.000	1270.000	8.000	0.000
C05-C03	1270.000	1060.044	209.956	170.000

Los valores de transferencia se refieren a los anclajes de material indicados, no sustituyen la holgura local8 de la salida del chute a C05. Las superficies se modelan y acotan por separado.


SESUVECA | PLANTA BRIQUETADORA | R18

04 | Secador al piso, seis niveles y salida transversal C04

SALIDA / ALZADO 1:10

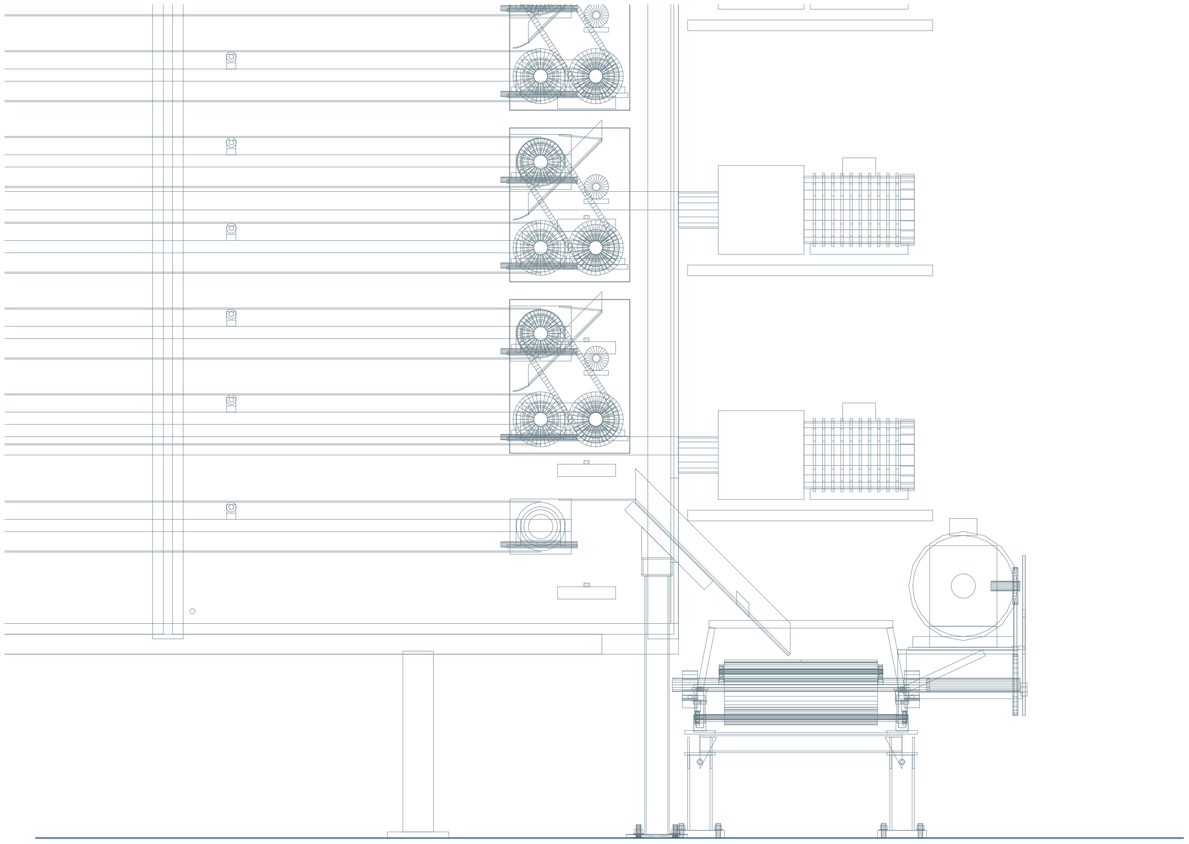

PLANTA LOCAL 1:20 / C04 A90 GRADOS

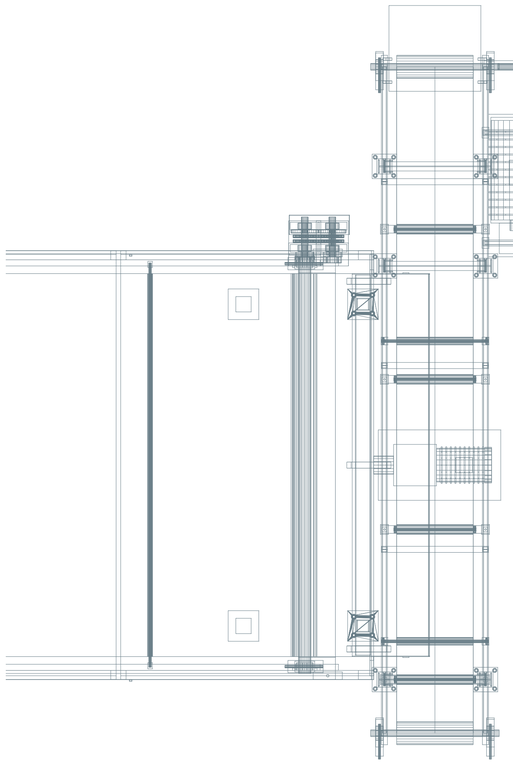

CONJUNTO AL PISO / ADAPTACION P

Cuerpo20000x2800x3000 con apoyo al NPT. Se conservan seis pisos utiles a paso280 y la colectora interna C06. El calentador vuelve al piso y el conducto se adapta a la nueva altura.

Se elimina el embudo profundo2500 ->200. Una chuta ancha45 grados lleva el flujo de C06 a la banda transversal B500 sin foso. C04 conserva4350 entre ejes, eje500 y componentes rigidos.

Los perfiles y placas retirados con la bancada elevada no se mantienen en la compra R18. Ver BOM y corte actualizado; las interfaces sin cota de fabricante conservan P/R.