
SESUVECA / PLANTA BRIQUETADORA


DISPOSICION GENERAL / APOYOS H / SEPARACION Y RETORNO

R33 / Propuesta geometrica / mm / A1 horizontal

ALZADO LONGITUDINAL / 1:100

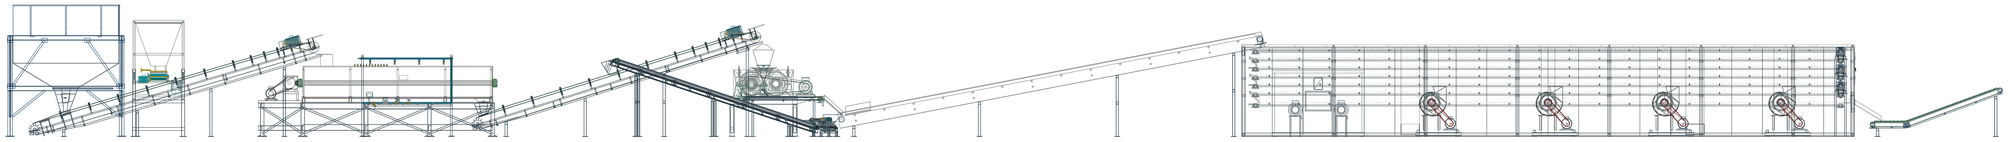

PLANTA / 1:100

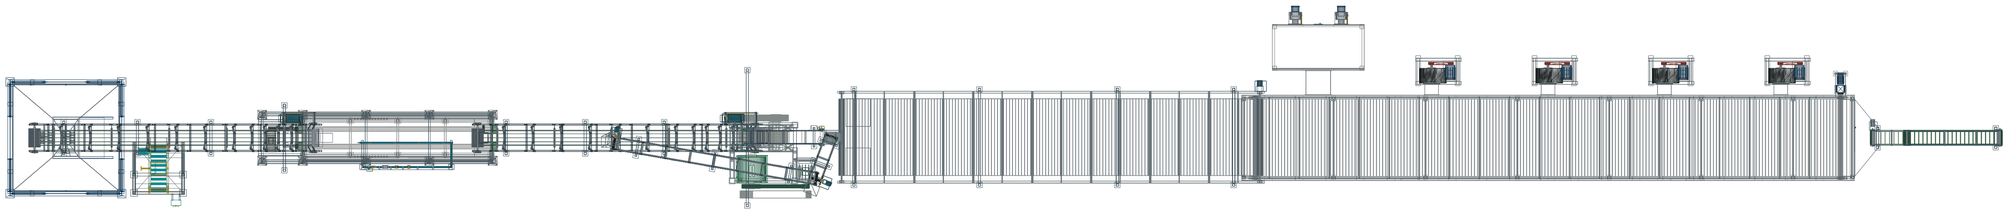

Cinta	Banda / exterior	Entre ejes	Pendiente	Cola Z	Cabeza Z
C01	500.0 / 900.0	9495.0	16.395 deg	240.0	2920.0
C02	500.0 / 900.0	9495.0	17.341 deg	420.0	3250.0
C05	400.0 / 460.0	2500.0	0.000 deg	1241.0	1241.0
C03	2500.0 / 3000.0	13900.0	10.860 deg	561.0	3179.9
C04	450.0 / 500.0	4302.2	14.983 deg	400.0	1512.3
C06	350.0 / 420.0	1461.2	9.852 deg	291.0	541.0
C07	350.0 / 420.0	7007.1	18.120 deg	291.0	2470.3

Apoyos H: 21 conjuntos. Columnas verticales globales; placas 180 x 180 x 12 en Z=0.

Envolvente con accesos: 67492.1 mm. Limite: 75000.0 mm.

Cruces C07 / C02 y C07 / base de prensa: se conservan los nodos prescritos del retorno.


O: documentado / P: propuesto / R: referencial. No aprobado para fabricacion.

SESUVECA / PLANTA BRIQUETADORA


GRIZZLY Y BANDEJA RECEPTORA EN COLA DE C03

R33 / Propuesta geometrica / mm / A1 horizontal

ALZADO DEL CONJUNTO / 1:10

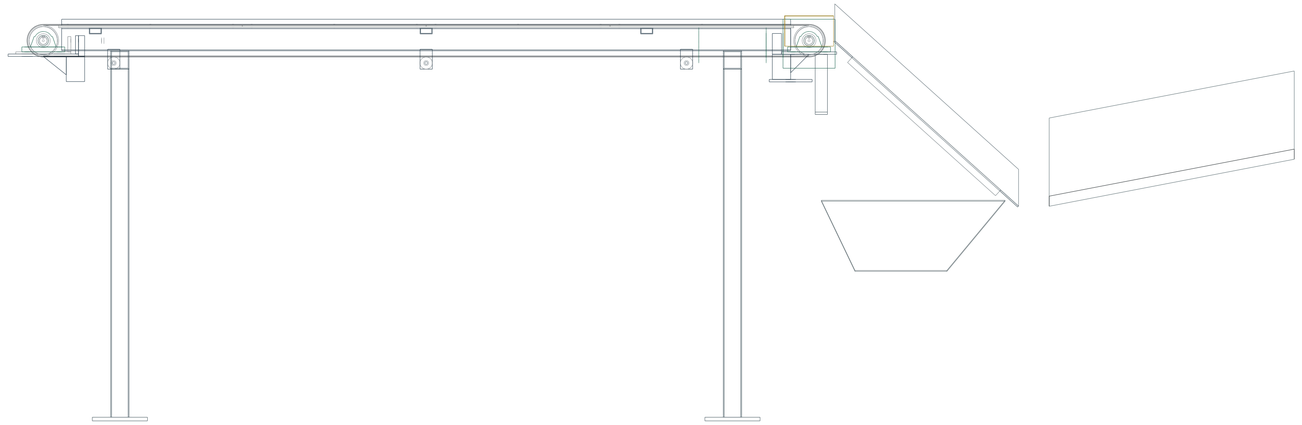

PLANTA DEL CONJUNTO / 1:25

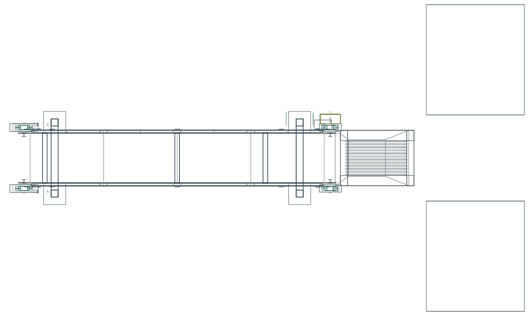

Referencia R33	Valor geometrico actual
Canal separador / recorrido horizontal / descenso	807.2 / 600.0 / 540.0 mm
Pletinas longitudinales	12 x 650 mm / abertura 15 mm
Labio separador / entrada receptora	Separacion horizontal 100.0 mm
Salida de finos X / Y / Z	27050.1 / 20.0 / 491.0 mm
Recepcion C03 X / Y / Z	27534.1 / 20.0 / 688.5 mm


Bandeja: boca superior 700 mm; base 2500 mm sobre C03 existente. Abertura ensanchada; separacion sin validar.

SESUVECA / PLANTA BRIQUETADORA


FINOS C06 / C07 / RETORNO AL CENTRO DE C02

R33 / Propuesta geometrica / mm / A1 horizontal

PLANTA DEL RETORNO / 1:40

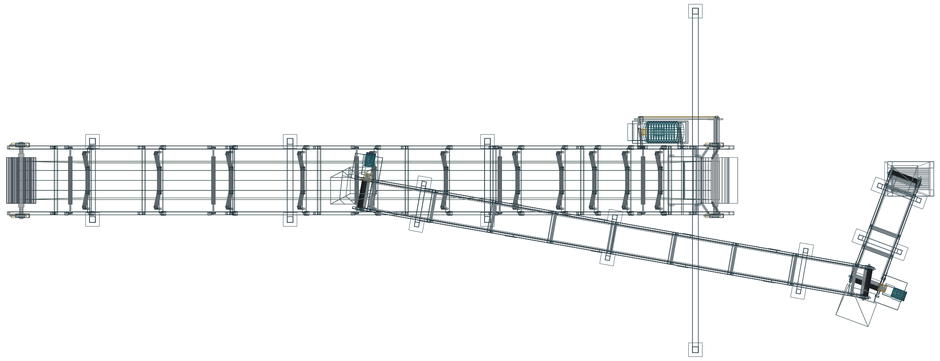

ALZADO DEL RETORNO / 1:35

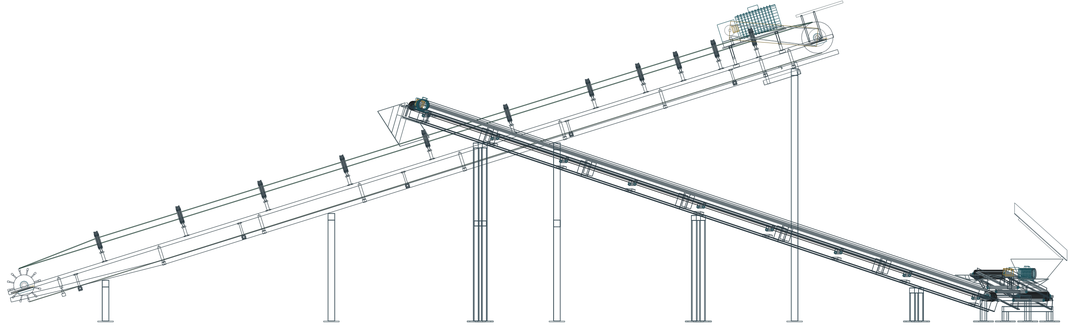

Nodo actual	X	Y	Z
Salida embudo	27050.1	20.0	491.0
C06 cola	27050.1	20.0	291.0
C06 cabeza	26550.1	-1330.0	541.0
C07 cola	26550.1	-1330.0	291.0
C07 cabeza	19990.5	-180.0	2470.3
Centro receptor C02	19990.5	0.0	2020.3

C07 cruza C02 y la base de prensa con los nodos prescritos; corregir el trazado antes del montaje.

Retorno ilustrativo de finos: no acredita capacidad, resistencia, separacion ni continuidad productiva.