SESUVECA

PLANTA BRIQUETADORA


DISPOSICIÓN GENERAL / C01 COMPARTIDA Y SECADOR INDEPENDIENTE

Medidas en mm / dimensiones de instalación / R24

VISTA LATERAL / 1:100



PLANTA / 1:100

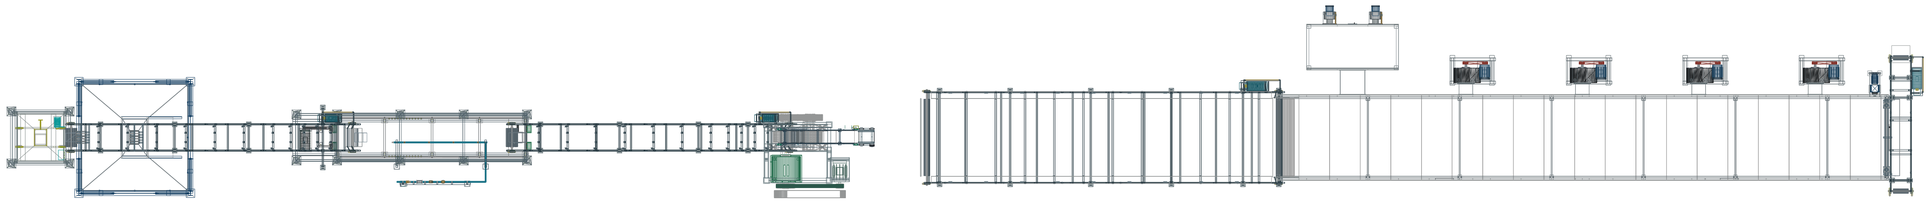

Cinta	Entre ejes	Exterior geométrico	Pendiente	Cola Z	Cabeza Z
C01	9495.0	9871.2	14.6°	400.0	2800.0
C02	9495.0	9871.2	17.3°	420.0	3250.0
C05	2500.0	2600.0	0.0°	1241.0	1241.0
C03	11800.0	12000.0	13.0°	850.0	3500.0
C04	4350.0	4500.0	0.0°	500.0	500.0

Envolvente mecánica: 62.6 m / con accesos: 63.8 m / límite: 75 m.

C03: ficha 12 000 mm exteriores; 11 800 mm entre tambores; proyección 11498.6 mm.

Adaptaciones de alimentación y montaje: propuesta geométrica. Cuerpos y componentes rígidos conservados.


SESUVECA

PLANTA BRIQUETADORA


CONJUNTOS MODIFICADOS / ALTURAS DESDE EL PISO

Medidas en mm / dimensiones de instalación / R24

BRIQUETADORA Y COLECTORA / LATERAL / 1:20

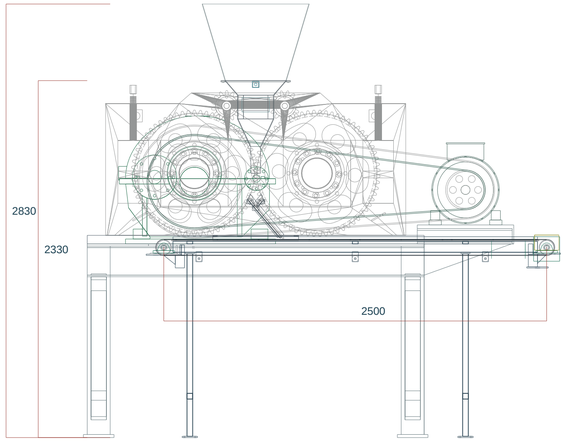

COLECTORA PLANA / PLANTA / 1:10

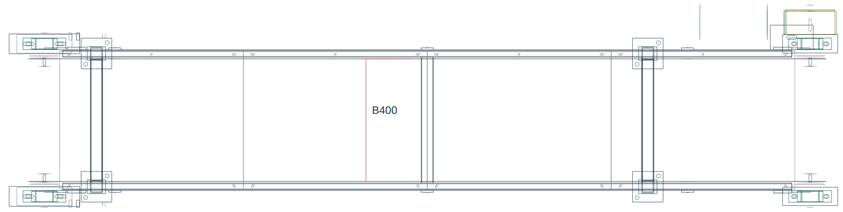


Tambores Ø100 / banda plana de 3 mm.

Superficie de carga: 1294.0 mm.

Labio de recepción: 1302.0 mm / separación: 8 mm.

Sólidos del conjunto de taller; soportes independientes.

MEZCLADORA / FRENTE / 1:20

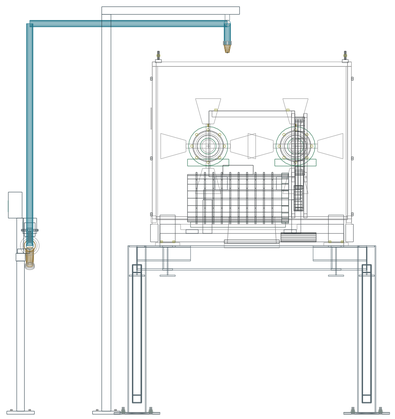

Mezcladora: cuerpo 6200 × 1300 × 1200 mm.

Bancada mezcladora: 1100 mm; entrada directa.

Se retiran la tolva añadida y sus apoyos.

Dosificador: bancada 800 mm / altura total 3400 mm.

Aglomerante sobre C01 antes del carbón.

Agua conectada al cuerpo de mezcla.

Adaptaciones de alimentación y montaje: propuesta geométrica. Cuerpos y componentes rígidos conservados.


SESUVECA

PLANTA BRIQUETADORA


BAJANTE MÓVIL / SECADOR INDEPENDIENTE

Medidas en mm / dimensiones de instalación / R24

LATERAL / 1:5

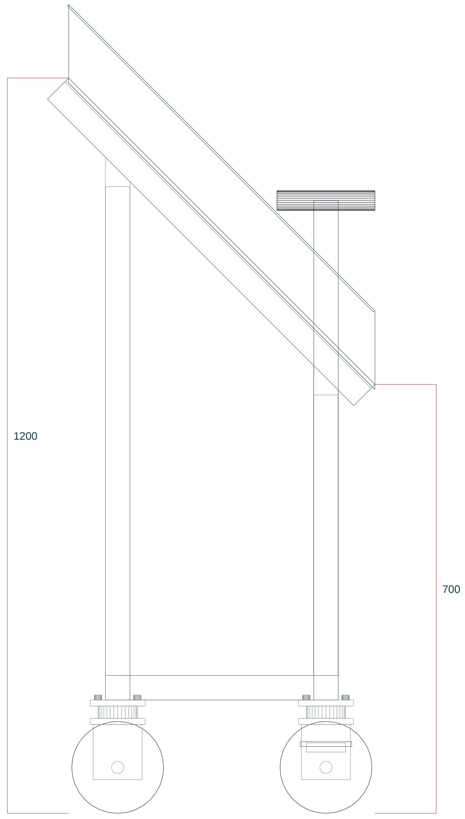

FRENTE / 1:5

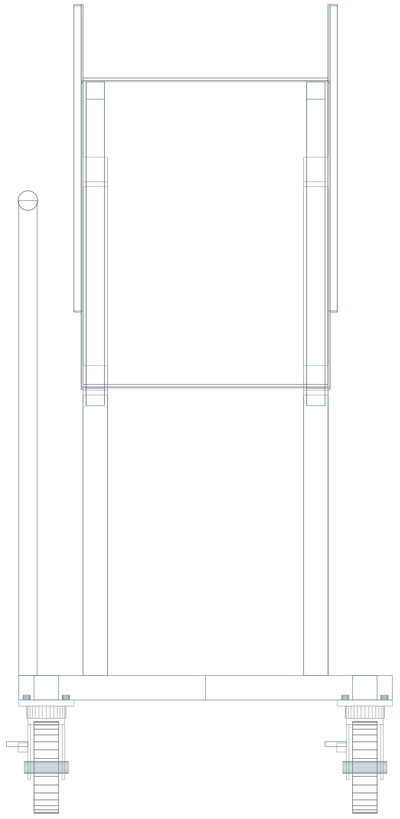

Canal útil: 400 mm / plano de deslizamiento: 45 grados.

Chapa 3 mm + revestimiento UHMW 6 mm.

Cuatro ruedas de 150 mm; dos con freno.

El conjunto se retira o desplaza independientemente.

No existe unión directa entre C05 y el alimentador del secador.

Adaptaciones de alimentación y montaje: propuesta geométrica. Cuerpos y componentes rígidos conservados.