
PLANTA BRIQUETADORA / R21


01 / CONJUNTO Y ALTURAS DE TRANSPORTADORES

Milímetros / alturas desde NPT. O: documentado; P: propuesto; R: reconstruido. Equipos a sus alturas originales.

DISPOSICIÓN LATERAL / 1:100

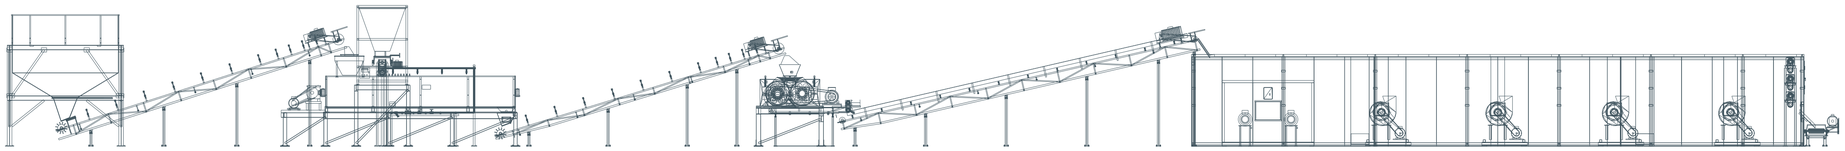

PLANTA / 1:100

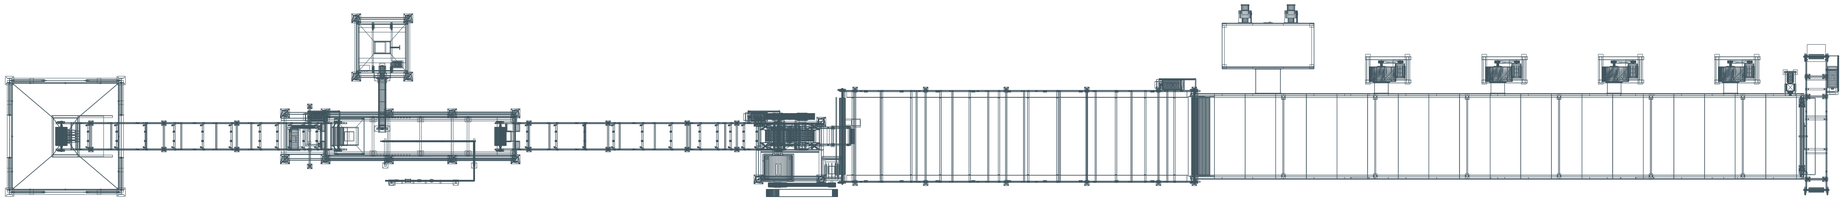

Cinta	L entre ejes	Pendiente °	Cola Z	Cabeza Z	Ancho útil
C01	9495.00	17.72	600.00	3490.06	500.00
C02	9495.00	16.99	420.00	3195.06	500.00
C05	2500.00	0.00	1182.00	1182.00	500.00
C03	11800.00	12.98	850.00	3500.00	2500.00
C04	4350.00	0.00	500.00	500.00	500.00

Envolvente 59.98 m / con accesos 62.24 m / suma de cintas 37.64 m / límite75 m.


Tolva +0 / prensa +0 / secador +0 mm: sin elevar cuerpos ni modificar patas. Mezcladora y dosificador conservan sus bases.

PLANTA BRIQUETADORA / R21


02 / TOLVA A C01 Y RECEPCIÓN DE MEZCLADORA

Milímetros / alturas desde NPT. O: documentado; P: propuesto; R: reconstruido. Equipos a sus alturas originales.

TOLVA Y ALIMENTACIÓN / 1:20 / DETALLE DE LA COLA

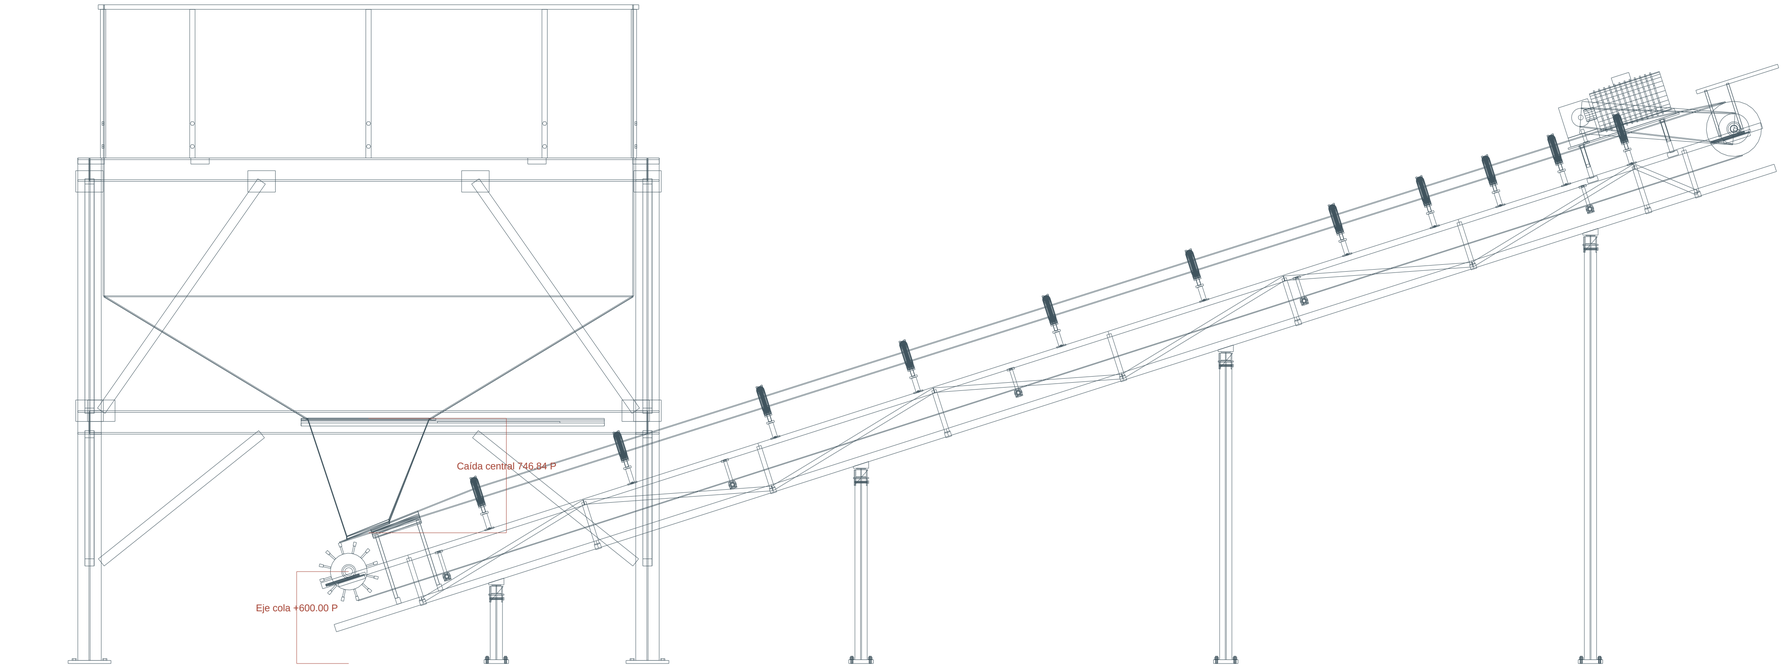

CAMPANA / PLANTA 1:10

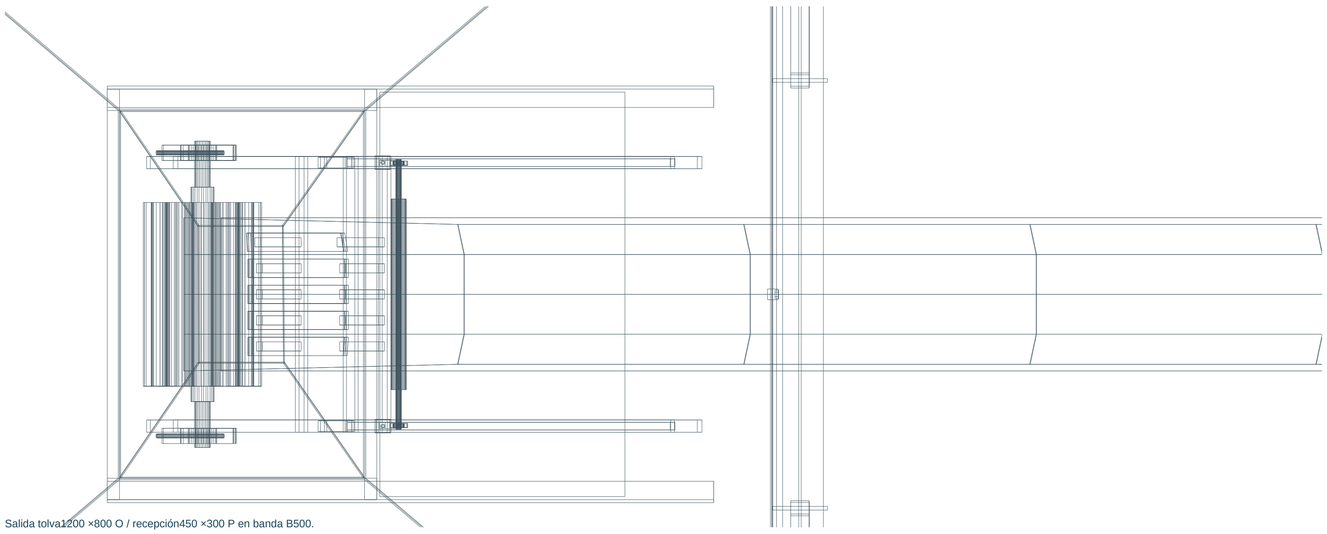

Salida tolva1200 ×800 O / recepción450 ×300 P en banda B500.

Parámetro	R20	R21
Cola C01 / eje	450.00	600.00
Pendiente C01	18.67347	17.72066
Entre ejes	9495.00	9495.00
Cabeza C01 Z	3490.06	3490.06
Recepción centrada X	2074.20	2074.20

Pared lateral mínima 60.38° / acero18 mm sobre banda; faldón flexible a2 mm.

Al subir más la cola se aplanan las paredes; se adopta600 mm.

PLANTA BRIQUETADORA / R21

03 / RECORRIDO Y TRANSFERENCIAS CALCULADAS

Milímetros / alturas desde NPT. O: documentado; P: propuesto; R: reconstruido. Equipos a sus alturas originales.

Conexión	Origen Z	Banda / boca Z	Desnivel	Delta X	Ángulo central
tolva-C01	1600.00	853.16	746.84	0.00	90.00°
C01-mix	3255.06	3000.00	255.06	84.92	71.59°
adapter-mix	3000.00	2950.00	50.00	0.00	90.00°
mix-C02	1085.00	689.57	395.43	0.00	90.00°
C02-briq	2960.06	2667.25	292.81	100.00	70.80°
briq-C05	1278.00	1270.00	8.00	0.00	90.00°
C05-C03	1270.00	1055.00	215.00	230.00	43.07°
dry-C04	601.00	581.00	20.00	0.00	90.00°
dos-mix	2675.00	2500.00	175.00	0.00	6.05°
C03-dry	3603.29	2850.00	753.29	523.81	55.19°

El desnivel total de una conexión no equivale al vuelo libre ni al ángulo de cada pared.

Punto del recorrido	Resultado geométrico
Tolva / C01	Centro bajo compuerta; paredes laterales >=60°; paso de polines980mm conservado
C01 / mezcladora	Cabeza mantiene Z; cuello más vertical, sin mover cuerpo de mezcladora
Mezcladora / C02	DeltaX 0.00 / caída 395.43 / mínimo entre bordes 325.05mm
Rodillos / C05	Se conserva recepción próxima; labio / banda 8.00mm P
C05 / C03	Banda a banda 215.00mm; guía revestida conservada
C03 / secador	Guía directa desde banda, sin torre ficticia; vuelos69,24 /40mm P
Secador / C04	Salida transversal a45°; labio20mm sobre banda; cuerpo del secador al piso

Agua y aglomerante permanecen conectados al mezclador. Giros, superficies receptoras y simulación usan el mismo proyecto.