SESUVECA

PLANTA BRIQUETADORA


DISPOSICIÓN GENERAL / DOSIFICACIÓN LATERAL Y RETORNO DE FINOS

R28 / Medidas en mm / Formato A1 horizontal

VISTA LATERAL / 1:100



PLANTA / 1:100

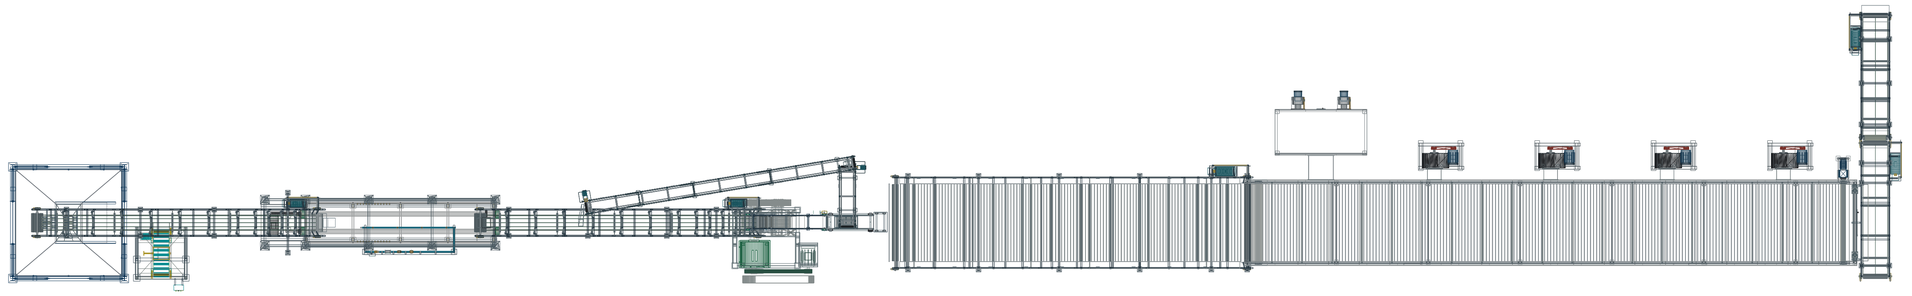

Cinta	Banda	Entre ejes	Exterior	Pendiente	Cola Z	Cabeza Z
C01	B500	9,495.0	9,871.2	15.641°	240.0	2,800.0
C02	B500	9,495.0	9,871.2	17.341°	420.0	3,250.0
C05	B400	2,500.0	2,600.0	0.000°	1,241.0	1,241.0
C03	B2500	11,800.0	12,000.0	12.978°	850.0	3,500.0
C04	B800	4,350.0	4,500.0	0.000°	500.0	500.0
C08	B800	4,143.6	4,293.6	16.000°	380.0	1,522.1
C09	B400	1,910.5	2,010.5	6.009°	400.0	600.0
C10	B300	9,055.1	9,155.1	13.085°	200.0	2,250.0

Envolvente: 61.924 m / con accesos: 63.734 m / límite: 75 m.

Retorno C09 + C10: 10.966 m. Secador independiente del grupo prensa.

Geometría de montaje propuesta. O: documentado / P: propuesto / R: referencial.


SESUVECA

PLANTA BRIQUETADORA


TOLVA ABIERTA Y DOSIFICADOR LATERAL / DESCARGA DIRECTA

R28 / Medidas en mm / Formato A1 horizontal

ALZADO LONGITUDINAL / 1:25

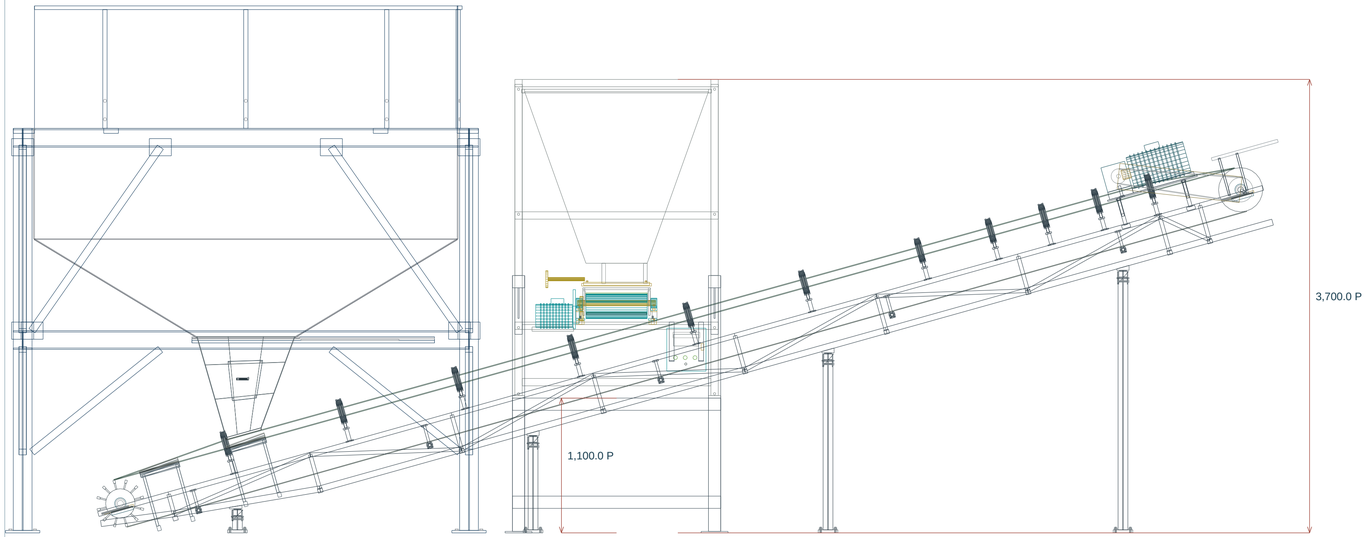

ALZADO TRANSVERSAL / 1:20

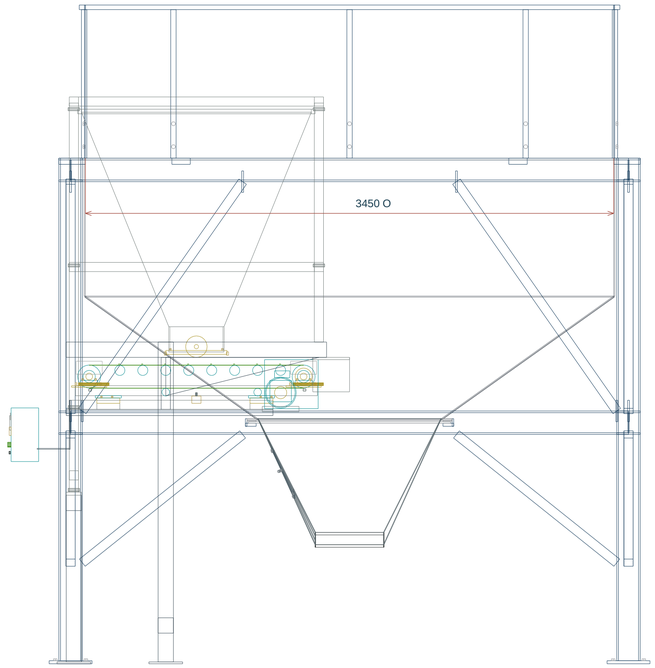

Dosificador: X = 5,100.0 / Y = -1,000.0 / giro 180°.

Bancada lateral con ménsulas y cartelas. Los apoyos delanteros inferiores se adaptan para liberar C01.

Se conservan tolva, banda, accionamiento y células de pesaje. Tablero completo reubicado hacia el exterior.

Salida propia: +1,775.0 / superficie C01: +1,576.4 / desnivel: 198.6 mm.

Descarga transversal directa. No se añade otra cinta ni una transición rígida entre equipos.

Tolva: boca 3450 x 3450 mm; salida y estructura de R26 conservadas.

Apertura superior de 1000 mm en el lado -X, contrario al avance de C01.

Remate de borde abierto: +3300 mm. Las otras tres paredes superiores llegan a +4300 mm.

Retirar panel, rigidizadores y tornillería asociados únicamente al lado abierto.

Mantener acceso exterior al tablero y a la regulación del dosificador.

SESUVECA

PLANTA BRIQUETADORA


PANEL RANURADO DESMONTABLE / CAPTACIÓN BAJO EL BAJANTE

R28 / Medidas en mm / Formato A1 horizontal

VISTA NORMAL AL PANEL / 1:2



BAJANTE Y CAPTACIÓN / LATERAL / 1:5

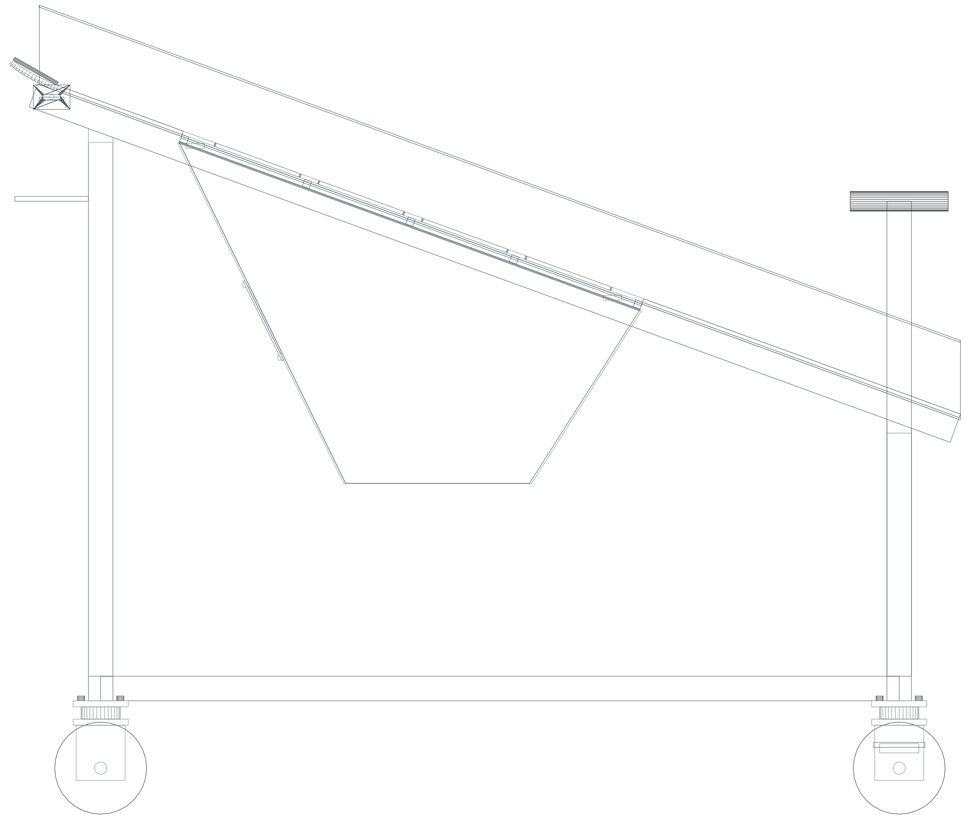

1. Panel de acero inoxidable 304, espesor 6 mm.
2. 96 ranuras longitudinales de 5 x 150 mm; extremos R2,5.
3. 24 columnas, separación libre de 10 mm; cuatro tramos con puentes de 30 mm.
4. Márgenes: 25 mm laterales y 55 mm en los extremos.
5. Bordes desbarbados y superficie enrasada. Fijación desmontable fuera del paso de producto.

El panel ocupa los tramos 250 a 1050 mm del bajante, medidos sobre el plano de 20°.

La nariz curva y los tramos lisos de entrada y salida permanecen.

Captación abierta bajo las ranuras: retirar chapa y revestimiento ciegos en esa zona.

Salida inferior: 300 x 200 mm, a +540 mm. Acople desmontable hacia C09.

Panel pasivo, sin vibrador. Abertura propuesta; no implica separación completa garantizada.

Geometría de montaje propuesta. O: documentado / P: propuesto / R: referencial.


SESUVECA

PLANTA BRIQUETADORA


RETORNO DE FINOS / C09 TRANSVERSAL Y C10 HACIA C02

R28 / Medidas en mm / Formato A1 horizontal

PLANTA DE IMPLANTACIÓN / 1:25

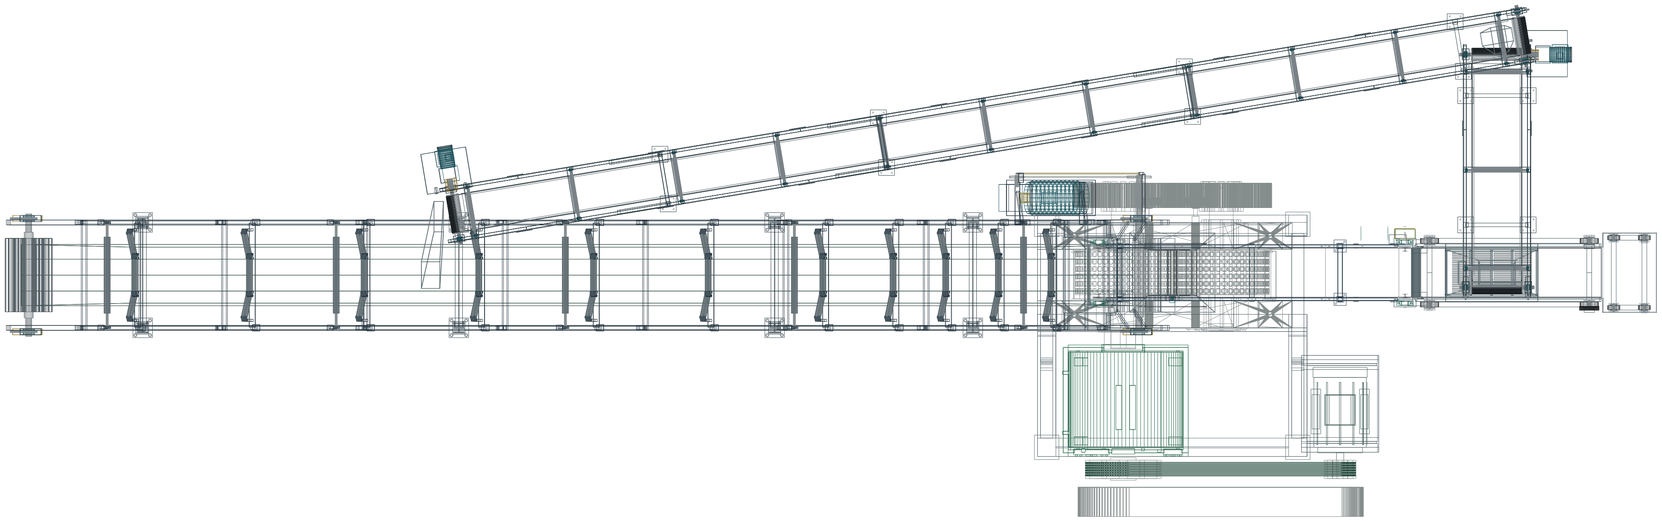

ALZADO LONGITUDINAL / 1:25

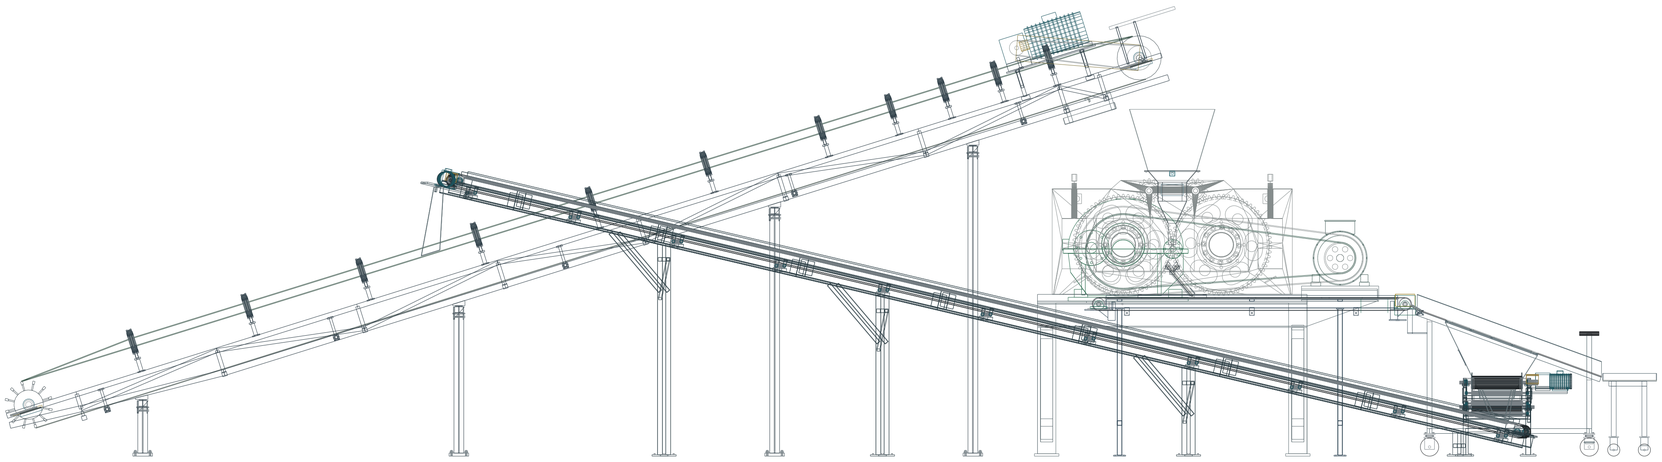

Cinta	Ancho banda / estructura	Entre ejes	Pendiente	Ejes desde piso
C09	400 / 550	1,910.5	6.009°	400.0 > 600.0
C10	300 / 450	9,055.1	13.085°	200.0 > 2,250.0

C10 rodea la prensa y entrega a C02 después de la mezcladora; las briquetas continúan hacia la bandeja de retirada.

TRANSFERENCIAS Y OPERACIÓN / REFERENCIAS DE MONTAJE

R28 / Medidas en mm / Formato A1 horizontal

Encuentro	Referencia geométrica
Salida dosificador / C01	1,775.0 > 1,576.4 / descenso 198.6 mm
Captación / C09	74.7 mm de descenso
C09 / C10	334.3 mm de descenso
C10 / C02	635.7 mm de descenso
Bajante	20° / recorrido 1600 mm / panel 800 x 400 x 6 mm
C01 y C02	9495 mm entre ejes, longitudes conservadas

RECETA SOBRE CARBÓN NUEVO

Carbón de referencia: 15.000 t/h. Aglomerante: 450.0 kg/h. Agua: 10.0 L/min.

Los finos recuperados vuelven a C02 sin dosificación automática adicional de agua ni aglomerante.

ARRANQUE DEL RETORNO

Con C02 disponible: arrancar C10 y después C09. Una parada del retorno bloquea la alimentación que genera nuevos finos.

La simulación muestra una fracción ilustrativa de finos cruzando las ranuras y regresando a la prensa. No representa un rendimiento de separación ni una capacidad de producción medida.

Se conservan las alternativas anteriores; los valores de esta carpeta corresponden a la geometría R28.