
SESUVECA

PLANTA BRIQUETADORA


DISPOSICIÓN GENERAL / DOSIFICACIÓN LATERAL Y RETORNO DE FINOS

R31 / Medidas en mm / Formato A1 horizontal

VISTA LATERAL / 1:100

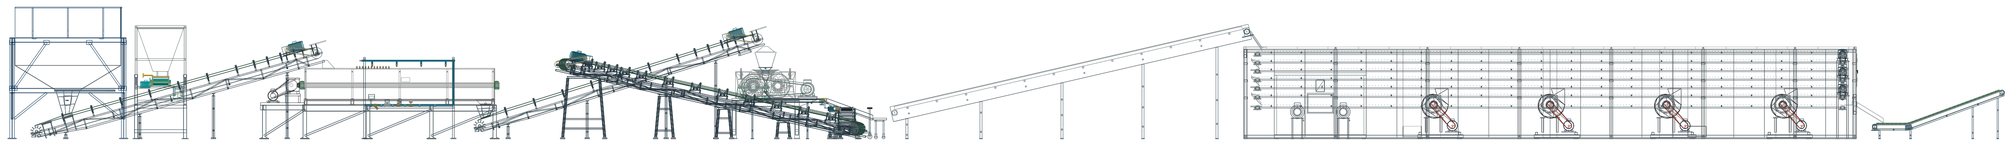

PLANTA / 1:100

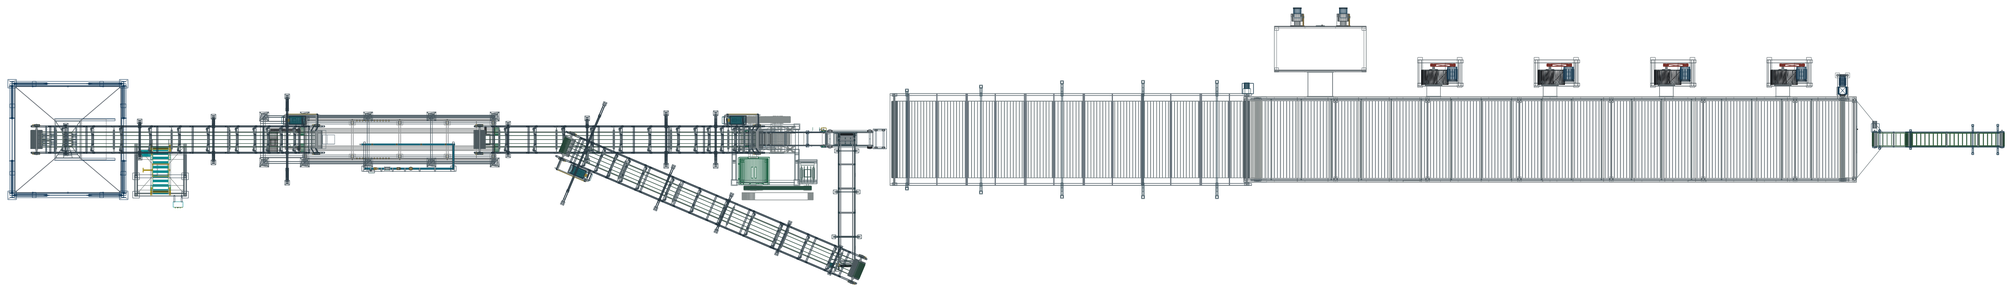

Cinta	Banda	Entre ejes	Exterior	Pendiente	Cola Z	Cabeza Z
C01	B500	9,495.0	9,871.2	15.641°	240.0	2,800.0
C02	B500	9,495.0	9,871.2	17.341°	420.0	3,250.0
C05	B400	2,500.0	2,600.0	0.000°	1,241.0	1,241.0
C03	B2500	11,800.0	12,000.0	12.978°	850.0	3,500.0
C04	B450	4,302.2	4,500.0	14.983°	400.0	1,512.3
C09	B400	4,278.1	4,378.1	7.657°	400.0	970.0
C10	B500	10,475.0	10,851.2	11.565°	330.0	2,430.0

Envolvente: 65.298 m / con accesos: 67.492 m / límite: 75 m.

Retorno de finos: 14.753 m. Secador independiente del grupo prensa.


SESUVECA

PLANTA BRIQUETADORA


TOLVA ABIERTA Y DOSIFICADOR LATERAL / DESCARGA DIRECTA

R31 / Medidas en mm / Formato A1 horizontal

ALZADO LONGITUDINAL / 1:30

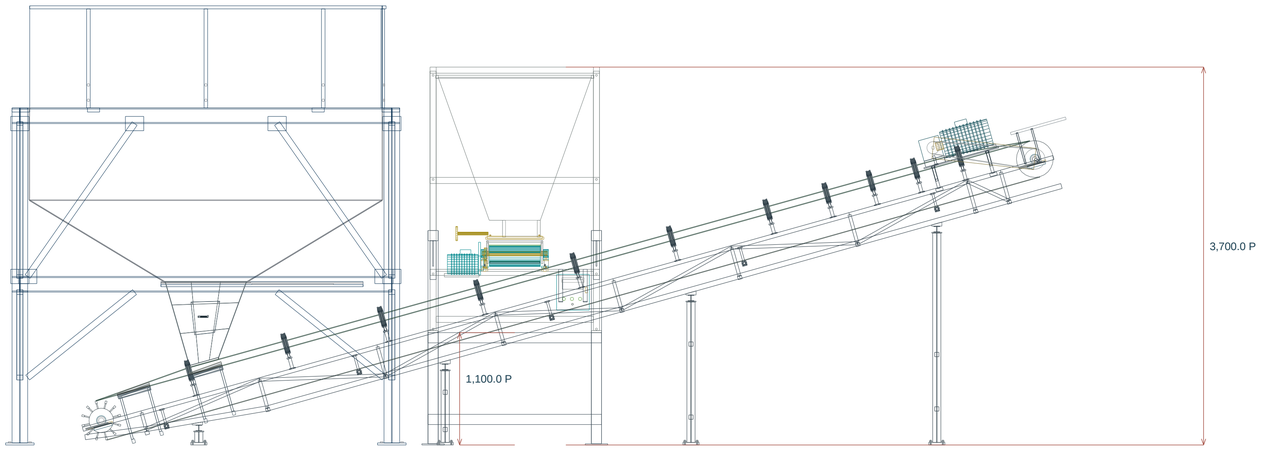

ALZADO TRANSVERSAL / 1:20

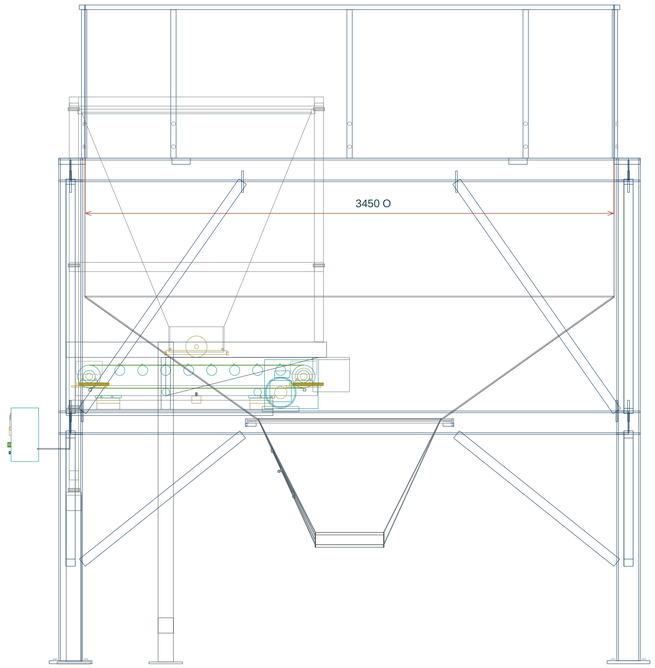

Dosificador: X = 5,100.0 / Y = -1,000.0 / giro 180°.

Bancada lateral con ménsulas y cartelas. Los apoyos delanteros inferiores se adaptan para liberar C01.

Se conservan tolva, banda, accionamiento y células de pesaje. Tablero completo reubicado hacia el exterior.

Salida propia: +1,775.0 / superficie C01: +1,576.4 / desnivel: 198.6 mm.

Descarga transversal directa. No se añade otra cinta ni una transición rígida entre equipos.

Tolva: boca 3450 x 3450 mm; salida y estructura de R26 conservadas.

Apertura superior de 1000 mm en el lado -X, contrario al avance de C01.

Remate de borde abierto: +3300 mm. Las otras tres paredes superiores llegan a +4300 mm.

Retirar panel, rigidizadores y tornillería asociados únicamente al lado abierto.

Mantener acceso exterior al tablero y a la regulación del dosificador.

SESUVECA

PLANTA BRIQUETADORA


PANEL RANURADO DESMONTABLE / CAPTACIÓN BAJO EL BAJANTE

R31 / Medidas en mm / Formato A1 horizontal

VISTA NORMAL AL PANEL / 1:2



BAJANTE Y CAPTACIÓN / LATERAL / 1:5

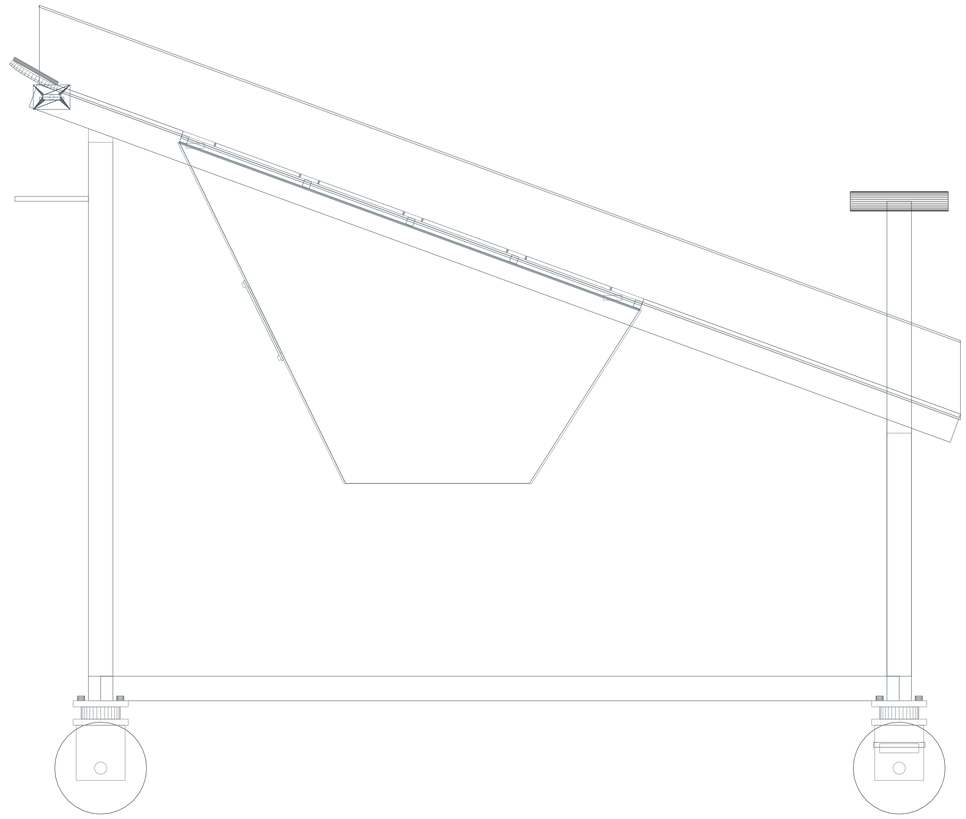

1. Panel de acero inoxidable 304, espesor 6 mm.
2. 96 ranuras longitudinales de 5 x 150 mm; extremos R2,5.
3. 24 columnas, separación libre de 10 mm; cuatro tramos con puentes de 30 mm.
4. Márgenes: 25 mm laterales y 55 mm en los extremos.
5. Bordes desbarbados y superficie enrasada. Fijación desmontable fuera del paso de producto.

El panel ocupa los tramos 250 a 1050 mm del bajante, medidos sobre el plano de 20°.

La nariz curva y los tramos lisos de entrada y salida permanecen.

Captación abierta bajo las ranuras: retirar chapa y revestimiento ciegos en esa zona.

Salida inferior: 300 x 200 mm, a +540 mm. Acople desmontable hacia C09.

Panel pasivo, sin vibrador. Abertura propuesta; no implica separación completa garantizada.


SESUVECA

PLANTA BRIQUETADORA


RETORNO DE FINOS / C09 TRANSVERSAL Y C10 HACIA C02

R31 / Medidas en mm / Formato A1 horizontal

PLANTA DE IMPLANTACIÓN / 1:25

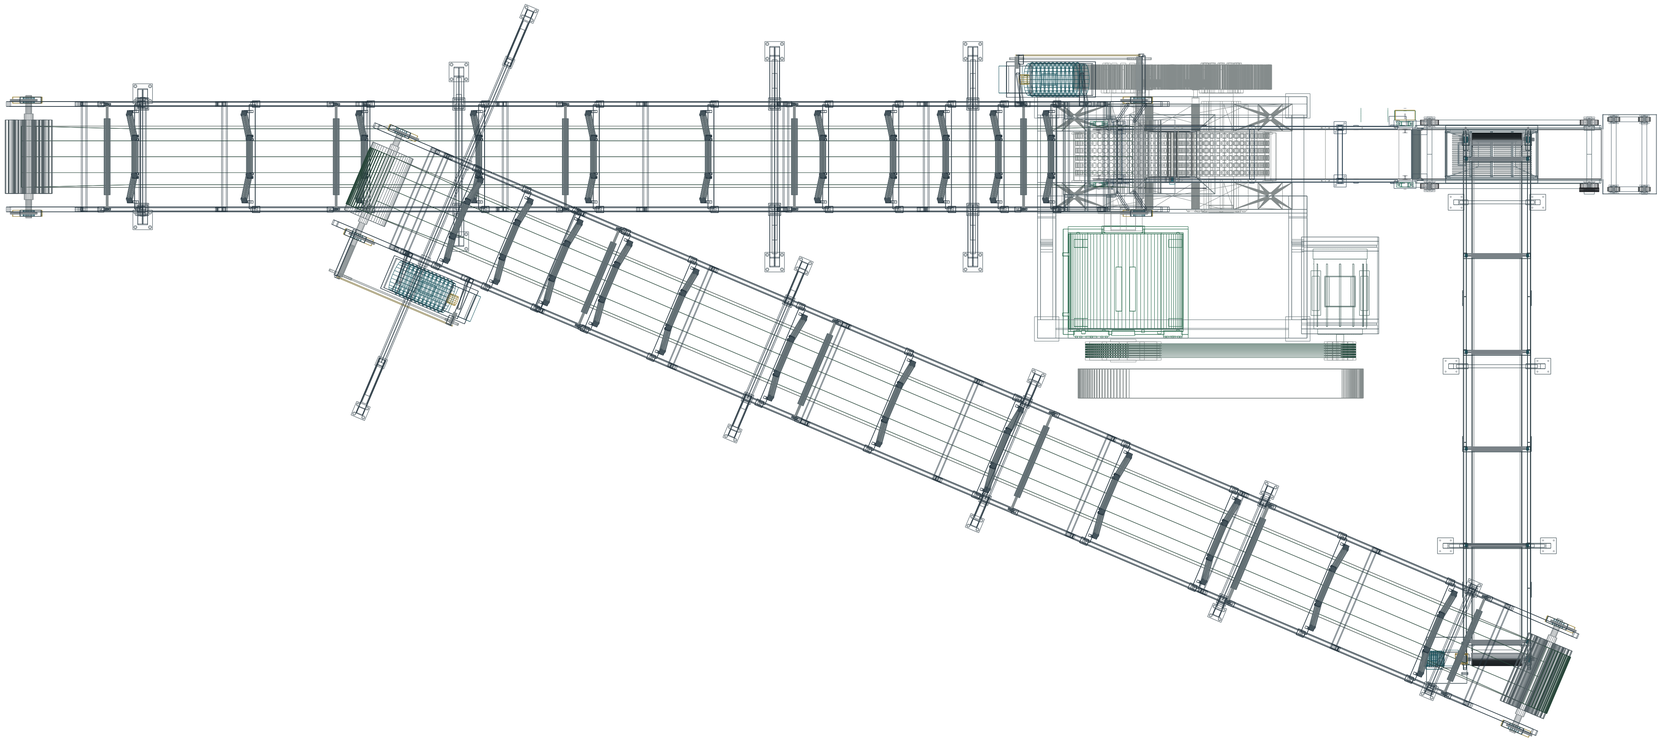

ALZADO LONGITUDINAL / 1:25

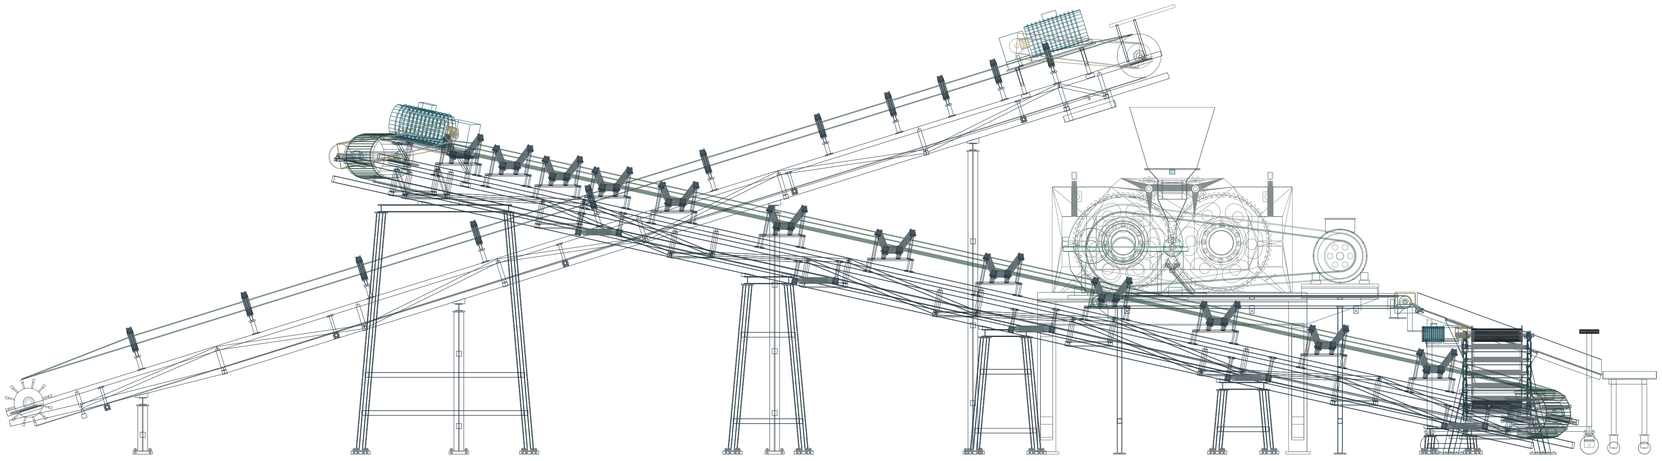

Cinta	Ancho banda / estructura	Entre ejes	Pendiente	Ejes desde piso
C09	400 / 550	4,278.1	7.657°	400.0 > 970.0
C10	500 / 900	10,475.0	11.565°	330.0 > 2,430.0

Retorno derecho: C09 transversal y C10 diagonal. Entregas directas sobre C10 y C02.

TRANSFERENCIAS Y OPERACIÓN / REFERENCIAS DE MONTAJE

R31 / Medidas en mm / Formato A1 horizontal

Encuentro	Referencia geométrica
Salida dosificador / C01	1,775.0 > 1,576.4 / descenso 198.6 mm
Captación / C09	70.4 mm de descenso
C09 / C10	404.8 mm de descenso
C10 / C02	1,111.4 mm de descenso
Bajante	20° / recorrido 1600 mm / panel 800 x 400 x 6 mm
C01 y C02	9495 mm entre ejes, longitudes conservadas

RECETA SOBRE CARBÓN NUEVO

Carbón de referencia: 15.000 t/h. Aglomerante: 450.0 kg/h. Agua: 10.0 L/min.

Los finos recuperados vuelven a C02 sin dosificación automática adicional de agua ni aglomerante.

ARRANQUE DEL RETORNO

Con C02 disponible: arrancar C10 y después C09. Una parada del retorno bloquea la alimentación que genera nuevos finos.


La simulación muestra una fracción ilustrativa de finos cruzando las ranuras y regresando a la prensa. No representa un rendimiento de separación ni una capacidad de producción medida.

Se conservan las alternativas anteriores; los valores de esta carpeta corresponden a la geometría R31.

SECADOR / TRANSPORTADORES PROPIOS


R31 / Medidas en mm / Formato A1 horizontal

C03 · CARGA DE MALLA INOXIDABLE / ALZADO 1:20

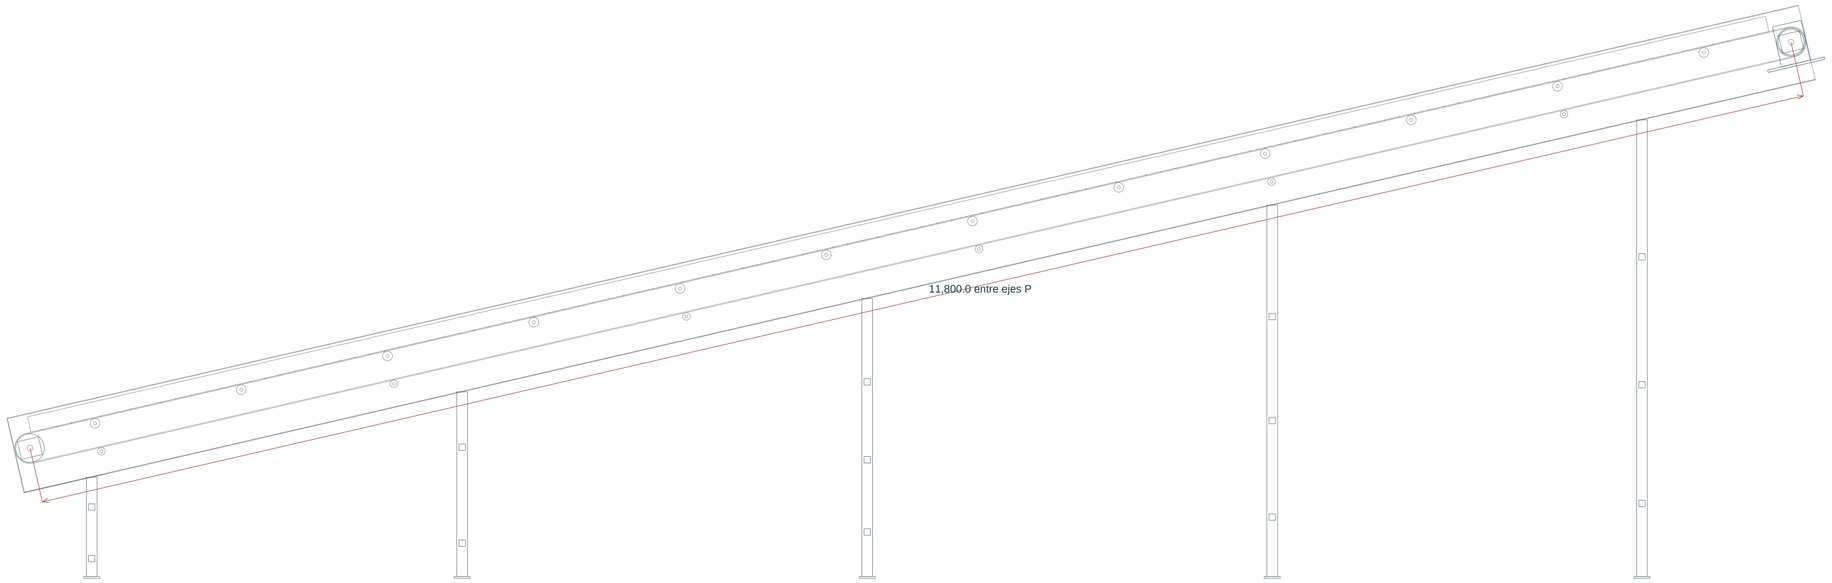

Envolvente nominal de ficha: 12 000 × 3 000 × 500 mm. Malla útil de 2 500 mm.

C04 · DESCARGA LONGITUDINAL / ALZADO 1:15

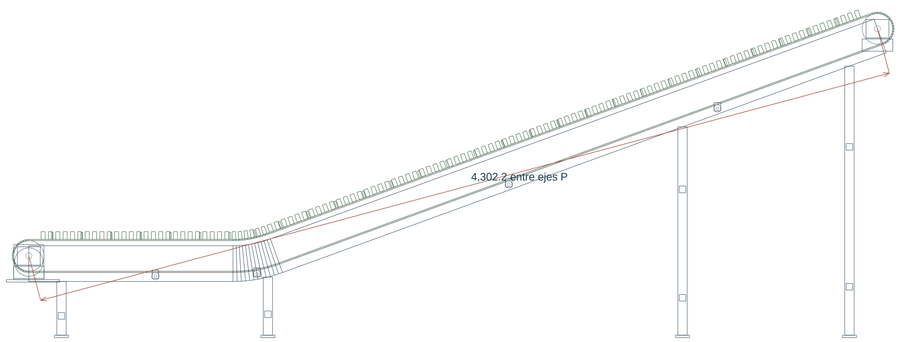

Envolvente nominal de ficha: 4 500 × 500 × 400 mm.

Desarrollo entre ejes: 4,350.0 mm. Banda útil: 450 mm.

Recepción horizontal y tramo inclinado a 20.0° P.

Caída del labio a la banda: 48.0 mm. Holgura a perfiles: 6.0 mm P.

Canal convergente para la salida del secador. Abertura de paso por comprobar.


SESUVECA

PLANTA BRIQUETADORA


APOYOS DE CINTA / VISTAS TRANSVERSALES

R31 / Medidas en mm / Formato A1 horizontal


C02 / PÓRTICO REPRESENTATIVO / 1:10

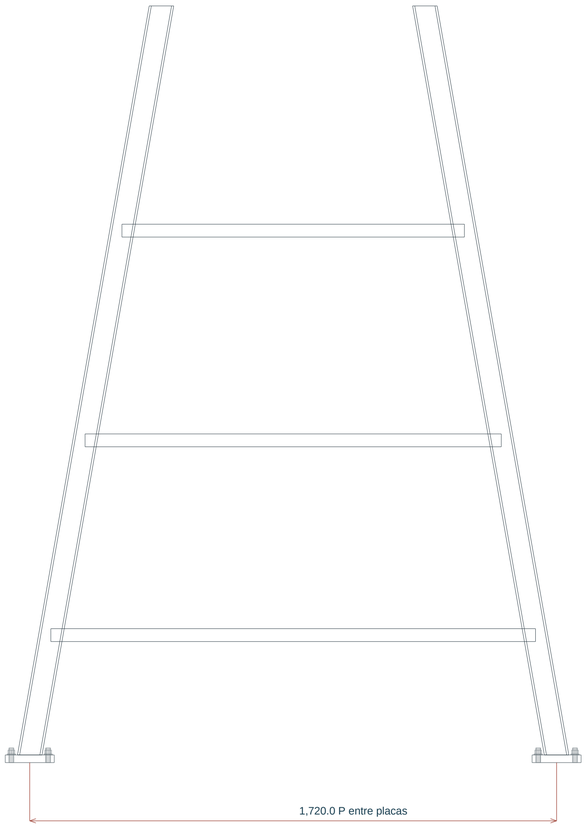

C10 / PÓRTICO REPRESENTATIVO / 1:20

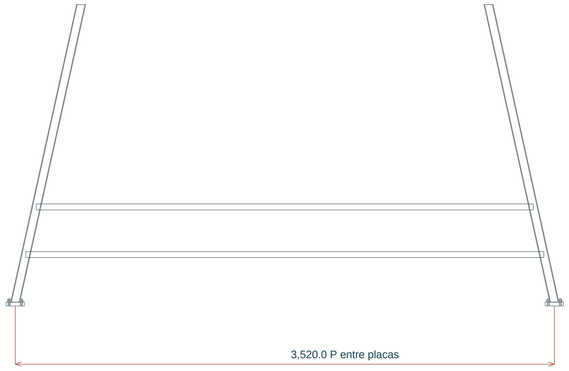

C04 / PÓRTICO REPRESENTATIVO / 1:10

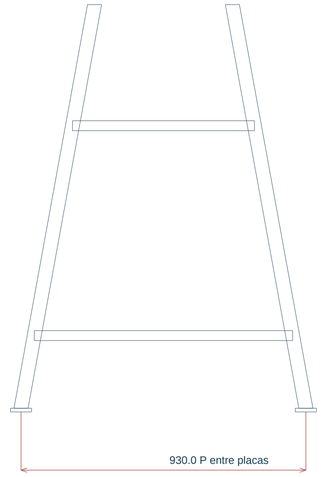

Dos patas abiertas por pórtico. Travesaños horizontales y placas de anclaje al nivel del piso.

Los pórticos especiales mantienen los asientos del bastidor. La altura de los travesaños deja libre el paso de los mecanismos.

Apoyos representados como propuesta geométrica. Secciones y anclajes sujetos a dimensionamiento.