
SESUVECA / PLANTA BRIQUETADORA


DISPOSICION Y ALTURAS

R32 / mm / A1 horizontal

VISTA LATERAL / 1:100

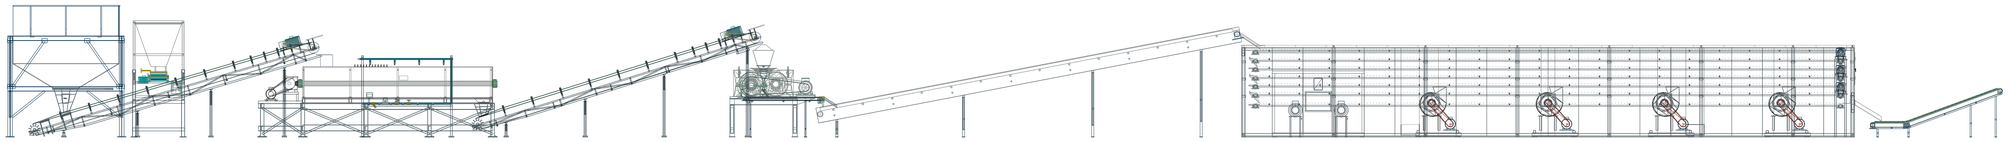

VISTA SUPERIOR / 1:100

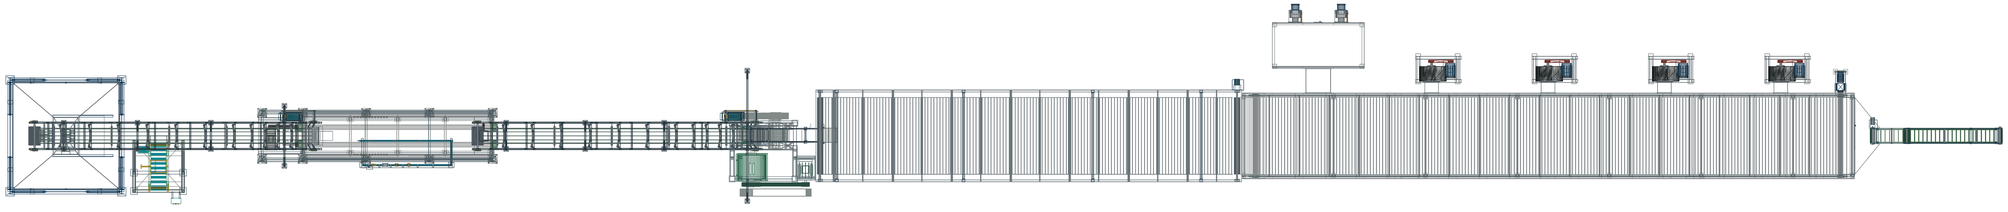

CINTA	ENTRE EJES	PENDIENTE	COLA Z	CABEZA Z
C01	9495.0	16.395°	240.0	2920.0
C02	9495.0	17.341°	420.0	3250.0
C05	2500.0	0.000°	1241.0	1241.0
C03	13858.0	10.856°	750.0	3360.0
C04	4302.2	14.983°	400.0	1512.3


Instalacion con accesos 67492.1 mm P. Limite 75000 mm.

SESUVECA / PLANTA BRIQUETADORA


TRANSFERENCIAS DE MATERIAL

R32 / mm / A1 horizontal

ENTRADA DE MEZCLADORA / 1:35

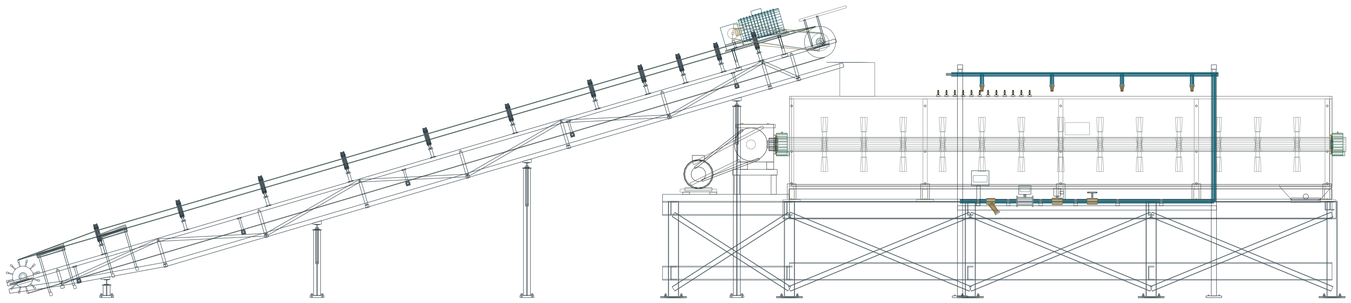

COLECTORA C05 / C03 / 1:10

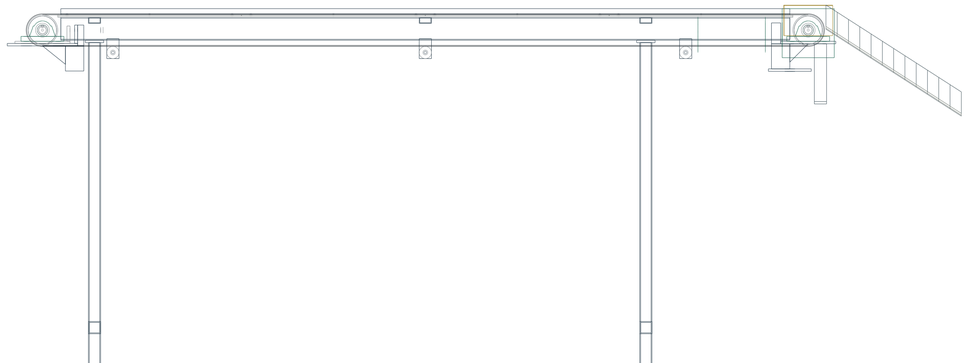

C01-mix / origen +2685.0 / receptor +2300.0 / desnivel 385.0 mm P

mix-C02 / origen +1085.0 / receptor +691.2 / desnivel 393.8 mm P

C02-briq / origen +3015.0 / receptor +2830.0 / desnivel 185.0 mm P

C05-C03 / origen +1267.5 / receptor +957.3 / desnivel 310.2 mm P

C03-dry / origen +3368.7 / receptor +2850.0 / desnivel 518.7 mm P

dry-C04 / origen +529.0 / receptor +481.0 / desnivel 48.0 mm P


C05-C03 / captura a 14.5 mm del desprendimiento / labio 12.0 mm sobre banda P.

SESUVECA / PLANTA BRIQUETADORA


APOYOS VERTICALES

R32 / mm / A1 horizontal


C01 / APOYO TRANSVERSAL / 1:20

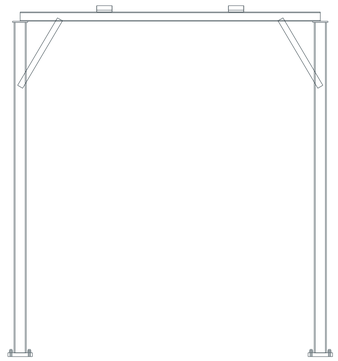

C02 / APOYO TRANSVERSAL / 1:20

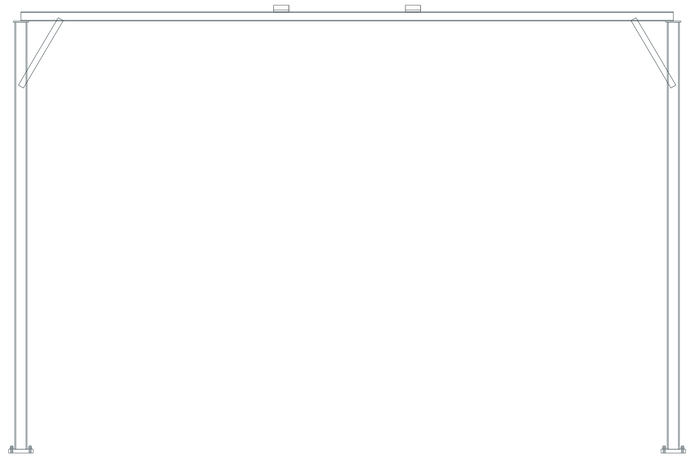

C03 / APOYO TRANSVERSAL / 1:20

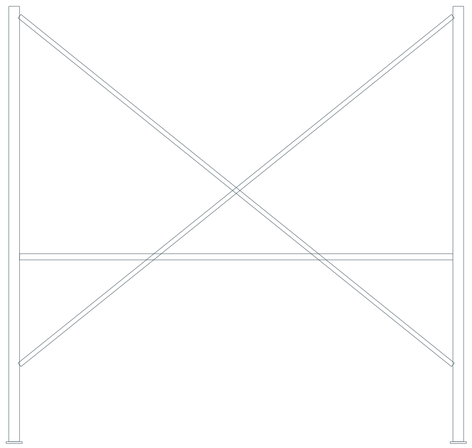

C04 / APOYO TRANSVERSAL / 1:20



Columnas paralelas a Z global. Placas apoyadas en Z=0. Cuatro caballetes arriostrados en C03.