
PLANTA BRIQUETADORA · R19


01 · RUTA PROVISIONAL CON RETIRO CONTINUO

Cuerpos, cotas y transportadores derivados de la propuesta abierta. Ambas alternativas se conservan en el proyecto JSON.

ALZADO GENERAL · 1:100

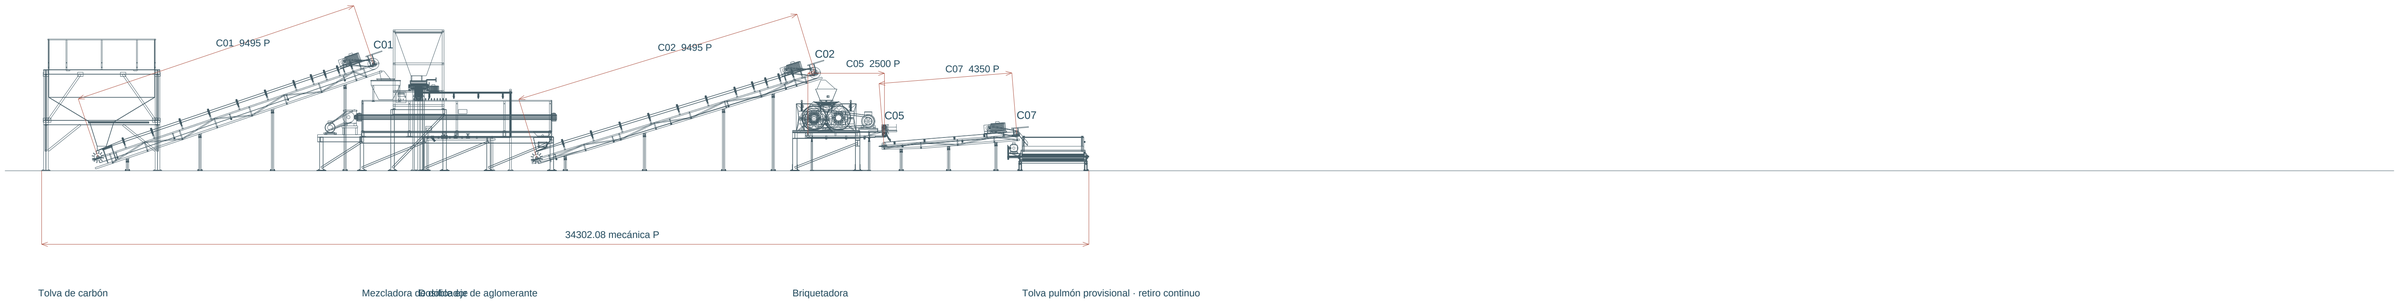

PLANTA GENERAL · 1:100 · PASILLOS Y RESERVAS P

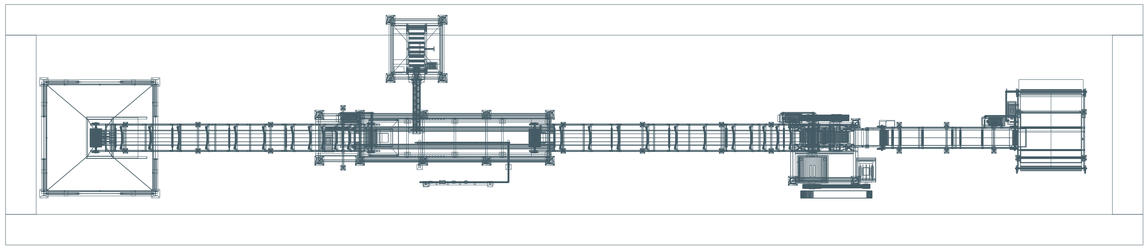

Cinta	Entre ejes mm	Exterior mm	Pendiente °	Cola Z mm	Cabeza Z mm	Banda mm
C01	9495.00	9871.20	18.67347	450.00	3490.06	500
C02	9495.00	9871.20	16.99364	420.00	3195.06	500
C05	2500.00	2680.00	0.00000	1182.00	1182.00	500
C07	4350.00	4500.00	4.61499	850.00	1200.00	500

Envolvente mecánica 34.302 m · con accesos 37.136 m · límite 75 m.

Suma cintas externas activas 25.840 m. B08 y bandas internas de equipos se contabilizan aparte.


Tolva provisional de poca profundidad: recepción continua, fondo móvil y salida transversal. Sin almacenamiento por horas.

PLANTA BRIQUETADORA · R19


02 · ALTERNATIVA CON SECADOR DE MALLAS

Cuerpos, cotas y transportadores derivados de la propuesta abierta. Ambas alternativas se conservan en el proyecto JSON.

ALZADO GENERAL · 1:100

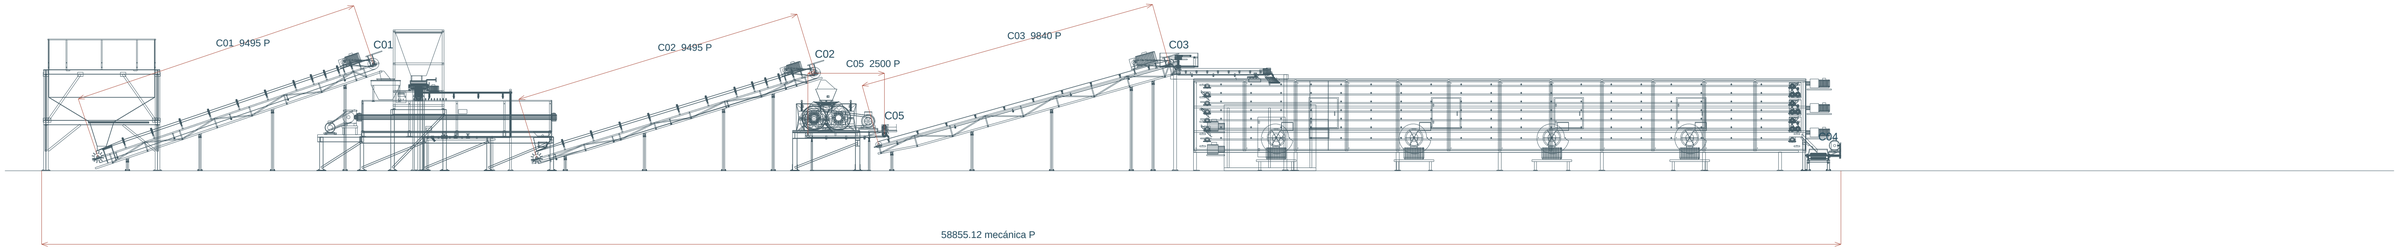

PLANTA GENERAL · 1:100 · PASILLOS Y RESERVAS P

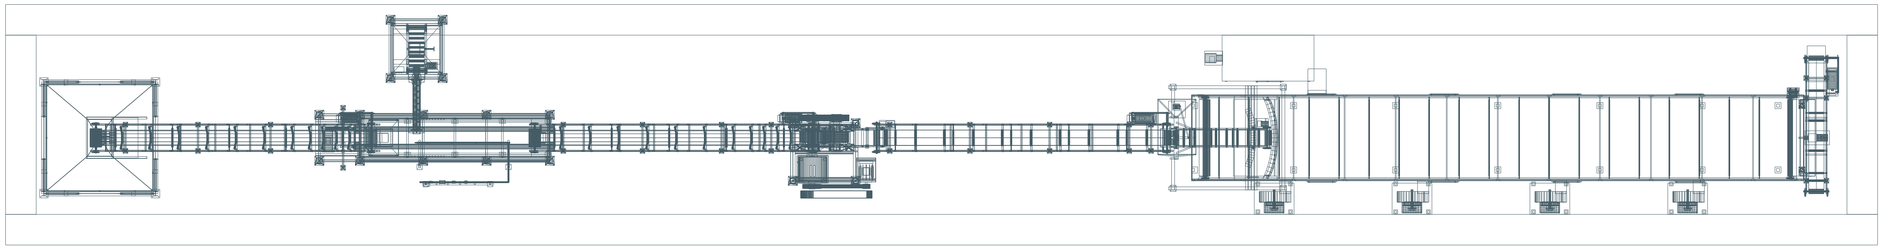

Cinta	Entre ejes mm	Exterior mm	Pendiente °	Cola Z mm	Cabeza Z mm	Banda mm
C01	9495.00	9871.20	18.67347	450.00	3490.06	500
C02	9495.00	9871.20	16.99364	420.00	3195.06	500
C05	2500.00	2680.00	0.00000	1182.00	1182.00	500
C03	9840.00	12000.00	15.62315	850.00	3500.00	500
C04	4350.00	4500.00	0.00000	500.00	500.00	500

Envolvente mecánica 58.855 m · con accesos 61.117 m · límite 75 m.

Suma cintas externas activas 35.680 m. B08 y bandas internas de equipos se contabilizan aparte.


Secador 20000 × 2800 × 3000 mm apoyado al piso. Vídeo: referencia de acabado y mecanismos visibles; no fuente dimensional.

PLANTA BRIQUETADORA · R19


03 · TOLVA PROVISIONAL Y FONDO MÓVIL B08

Recepción con retiro continuo confirmado por el usuario · conjunto nuevo P · volumen geométrico, sin capacidad productiva certificada.


ALZADO LOCAL · 1:10

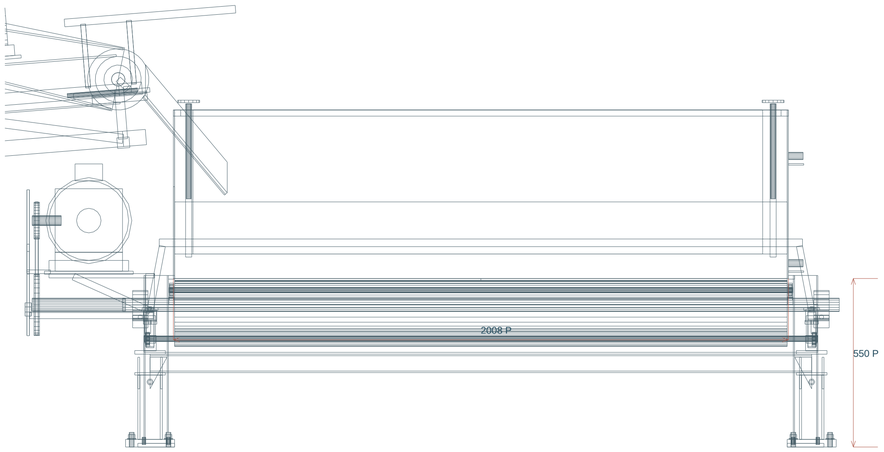

PLANTA LOCAL · 1:10

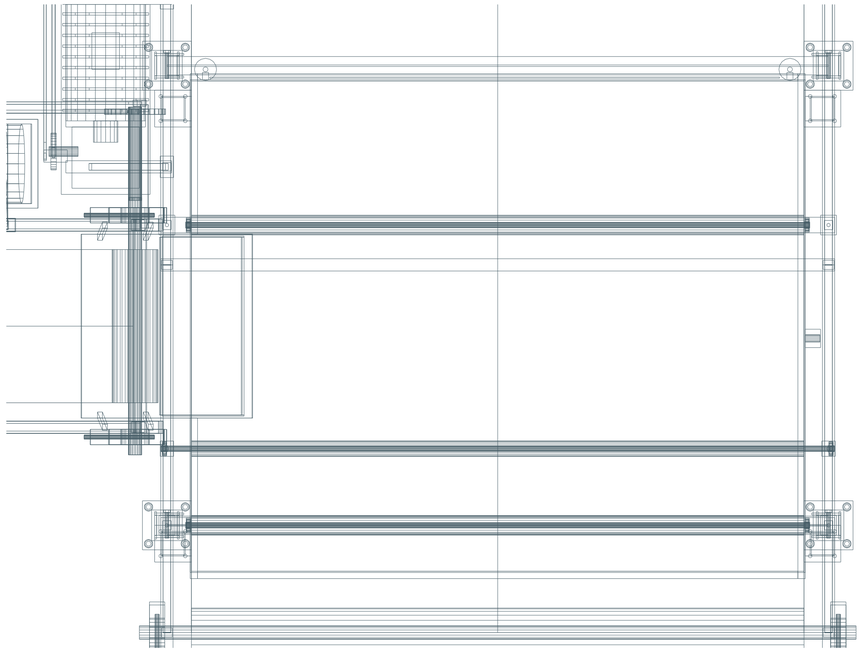

FRENTE DE RECEPCIÓN · 1:10

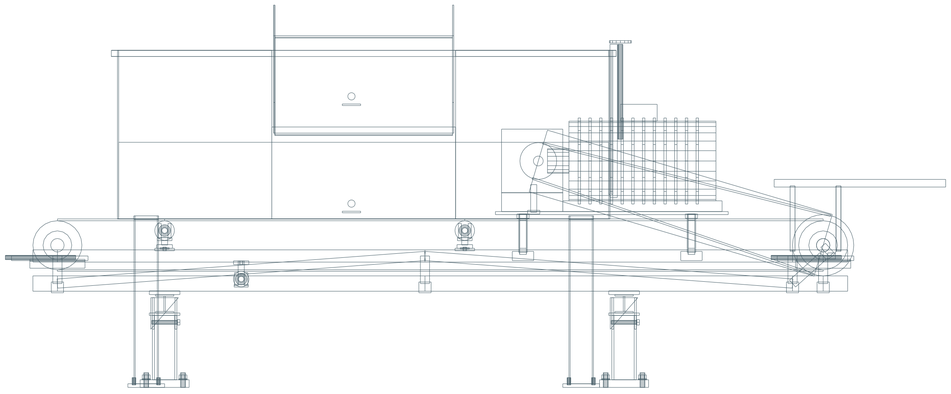

Parámetro	Geometría R19 P
Hueco útil	2000 × 1600 mm
Envolvente de carcasa	2008 × 1608 × 1100 mm
Altura máxima representada	1248.00 mm NPT
Fondo móvil / cama	550 / 800.00 mm NPT
Cama nominal / máxima	250 / 400 mm
Volumen de cama actual	0.80 m³
Guía UHMWPE / respaldo	8 mm / acero 4 mm
Entrada y salida de guía	59.64 / 30 mm libres


Guillotina de salida regulable · sensores L y HH · accionamiento y bastidor propios · retirada transversal Y+.

La posición representada de la guía acompaña la cama de estudio; ajuste P antes de montaje. No se supone regulación automática.

PLANTA BRIQUETADORA · R19

DETALLE · C05-C07 · SUPERFICIES Y GUÍA REVESTIDA

Diferencia total entre bandas separada del vuelo inicial y del remate final. Desprendimiento ilustrativo 85° R/P.

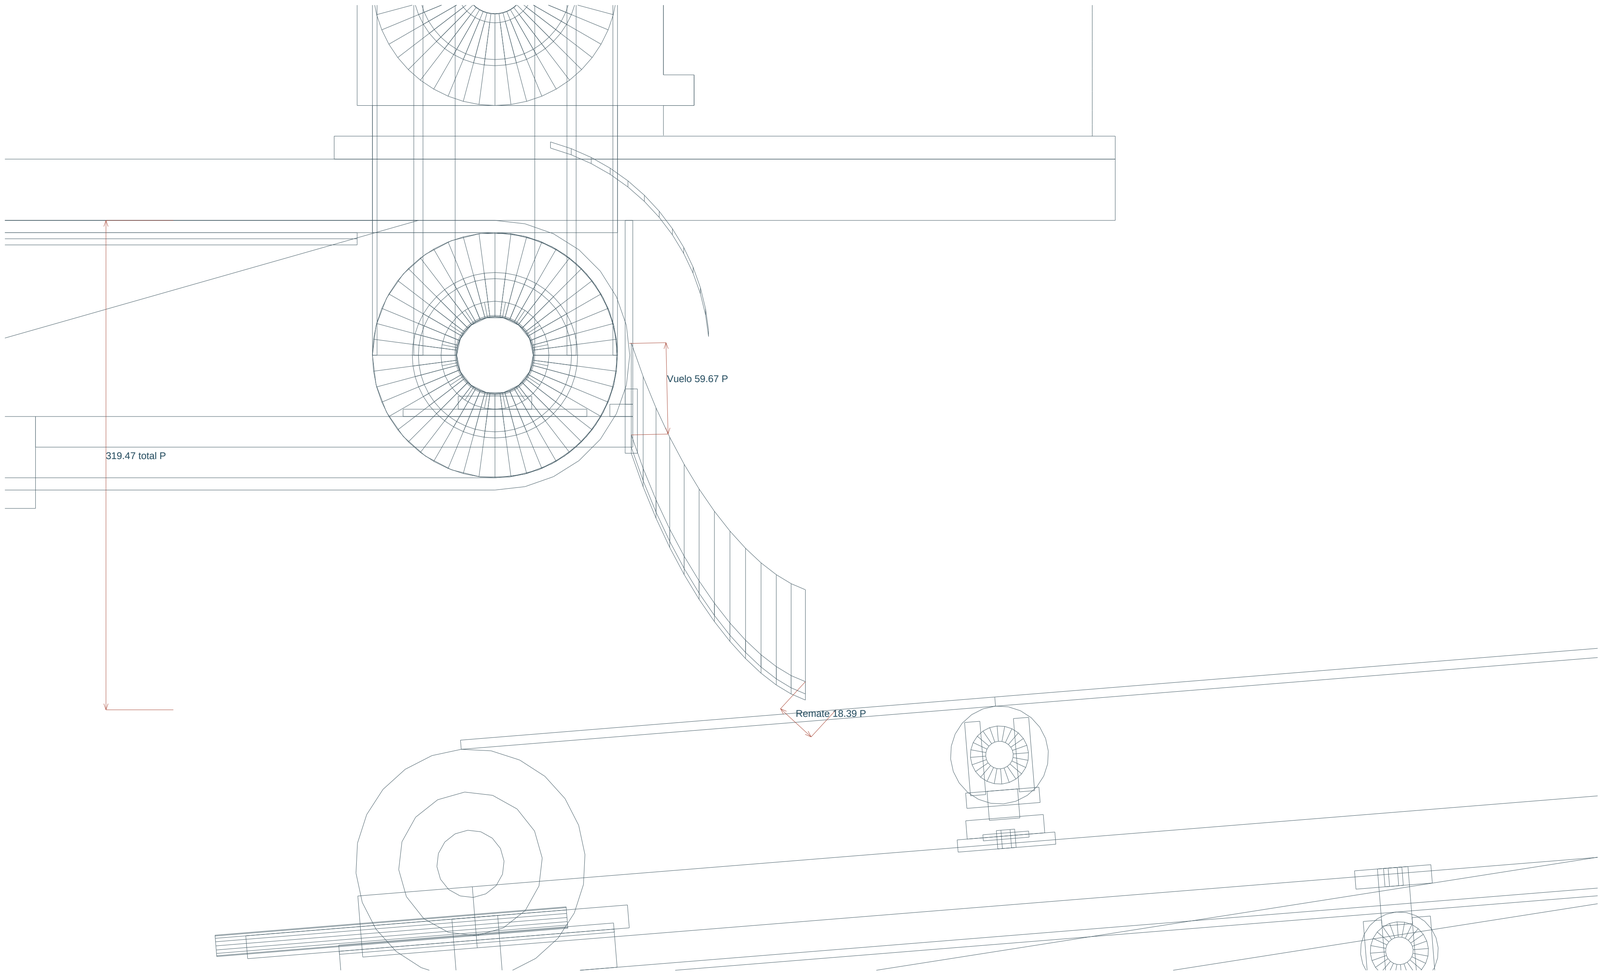


Dato desde NPT	mm / propuesta P
Superficie emisora	1270.00
Superficie receptora	950.53
Desnivel total entre bandas	319.47
Vuelo inicial vertical	59.67
Remate vertical final	18.39
Ancho útil de guía	480
Revestimiento / chapa	UHMWPE 8 / acero 4

Guía, boca receptora y soportes calculados en las coordenadas del modelo. No se deforman componentes rígidos.

La guía acompaña el descenso; no se interpreta todo el desnivel como caída libre.

Los vuelos representados no garantizan integridad de briquetas ni sustituyen la puesta a punto.


PLANTA DEL ENCUENTRO · 1:2

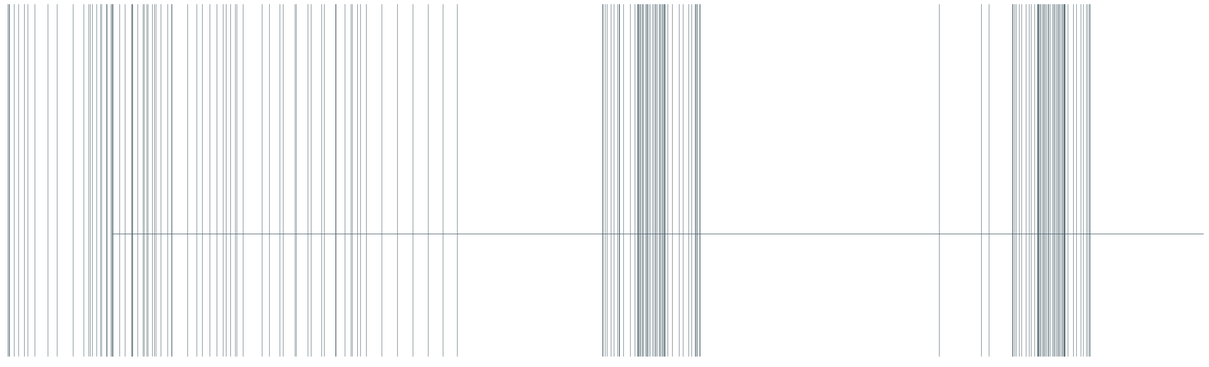

PLANTA BRIQUETADORA · R19

DETALLE · C05-C03 · SUPERFICIES Y GUÍA REVESTIDA

Diferencia total entre bandas separada del vuelo inicial y del remate final. Desprendimiento ilustrativo 85° R/P.

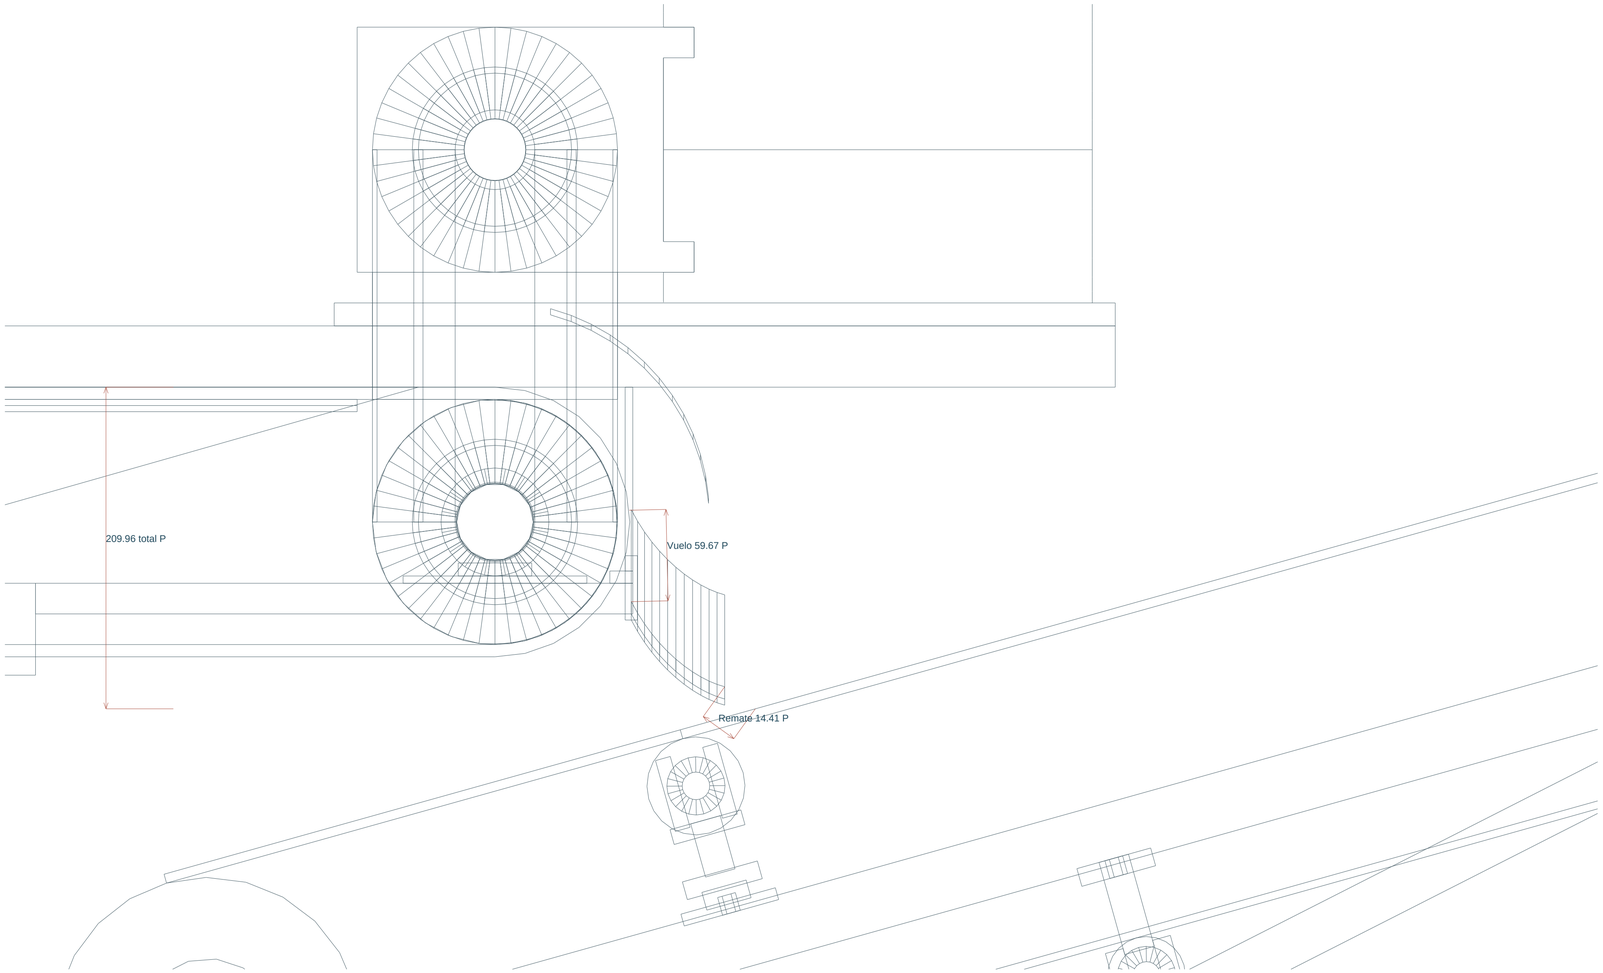


Dato desde NPT	mm / propuesta P
Superficie emisora	1270.00
Superficie receptora	1060.04
Desnivel total entre bandas	209.96
Vuelo inicial vertical	59.67
Remate vertical final	14.41
Ancho útil de guía	480
Revestimiento / chapa	UHMWPE 8 / acero 4

Guía, boca receptora y soportes calculados en las coordenadas del modelo. No se deforman componentes rígidos.

La guía acompaña el descenso; no se interpreta todo el desnivel como caída libre.

Los vuelos representados no garantizan integridad de briquetas ni sustituyen la puesta a punto.


PLANTA DEL ENCUENTRO · 1:2

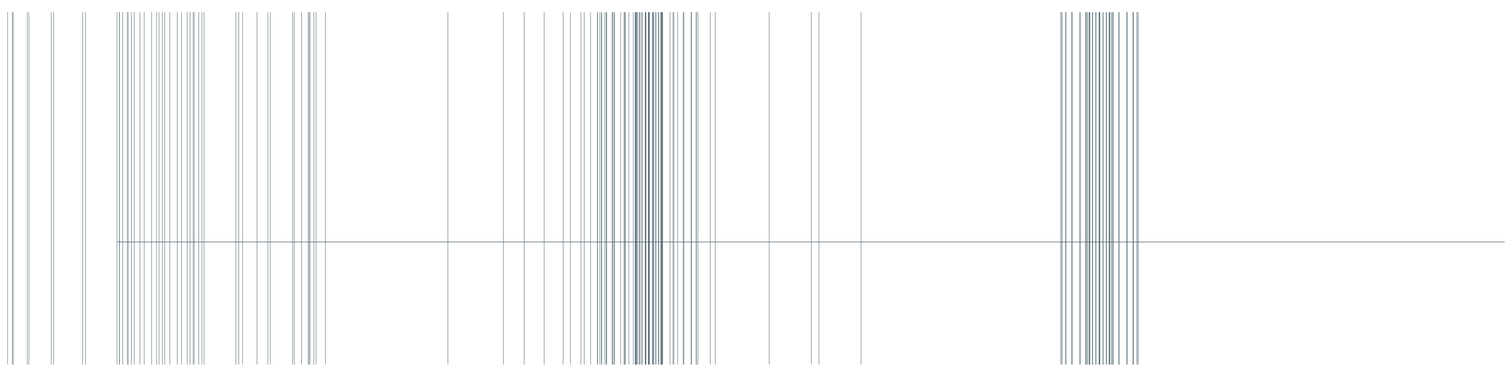

PLANTA BRIQUETADORA · R19

DETALLE · C03-traverse · SUPERFICIES Y GUÍA REVESTIDA

Diferencia total entre bandas separada del vuelo inicial y del remate final. Desprendimiento ilustrativo 85° R/P.

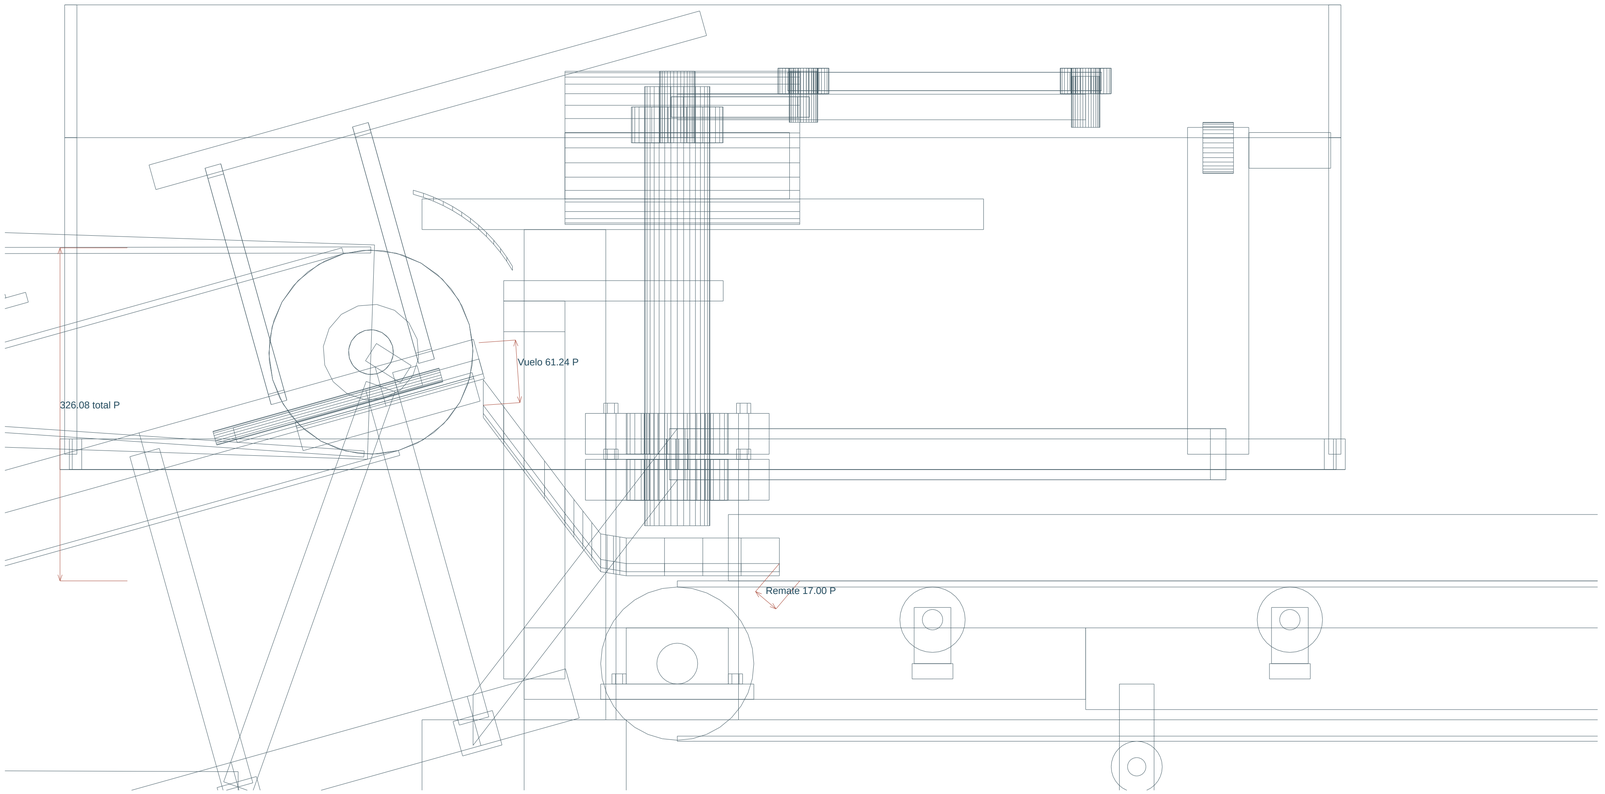


Dato desde NPT	mm / propuesta P
Superficie emisora	3602.08
Superficie receptora	3276.00
Desnivel total entre bandas	326.08
Vuelo inicial vertical	61.24
Remate vertical final	17.00
Ancho útil de guía	140 × 2 canales
Revestimiento / chapa	UHMWPE 8 / acero 4

Guía, boca receptora y soportes calculados en las coordenadas del modelo. No se deforman componentes rígidos.

La guía acompaña el descenso; no se interpreta todo el desnivel como caída libre.

Los vuelos representados no garantizan integridad de briquetas ni sustituyen la puesta a punto.

PLANTA DEL ENCUENTRO · 1:3

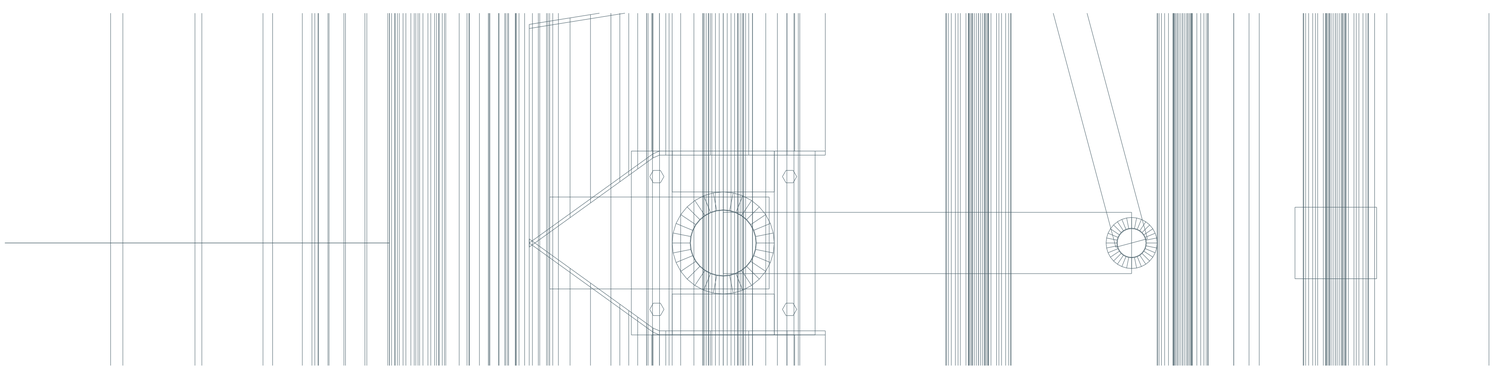


PLANTA BRIQUETADORA · R19


07 · REPARTIDOR Y ENTRADA AL PRIMER NIVEL

Cinta oscilante B500 · recepción dividida alrededor del pivote · cuchara móvil y apron fijo de recepción P.

ALZADO · 1:10

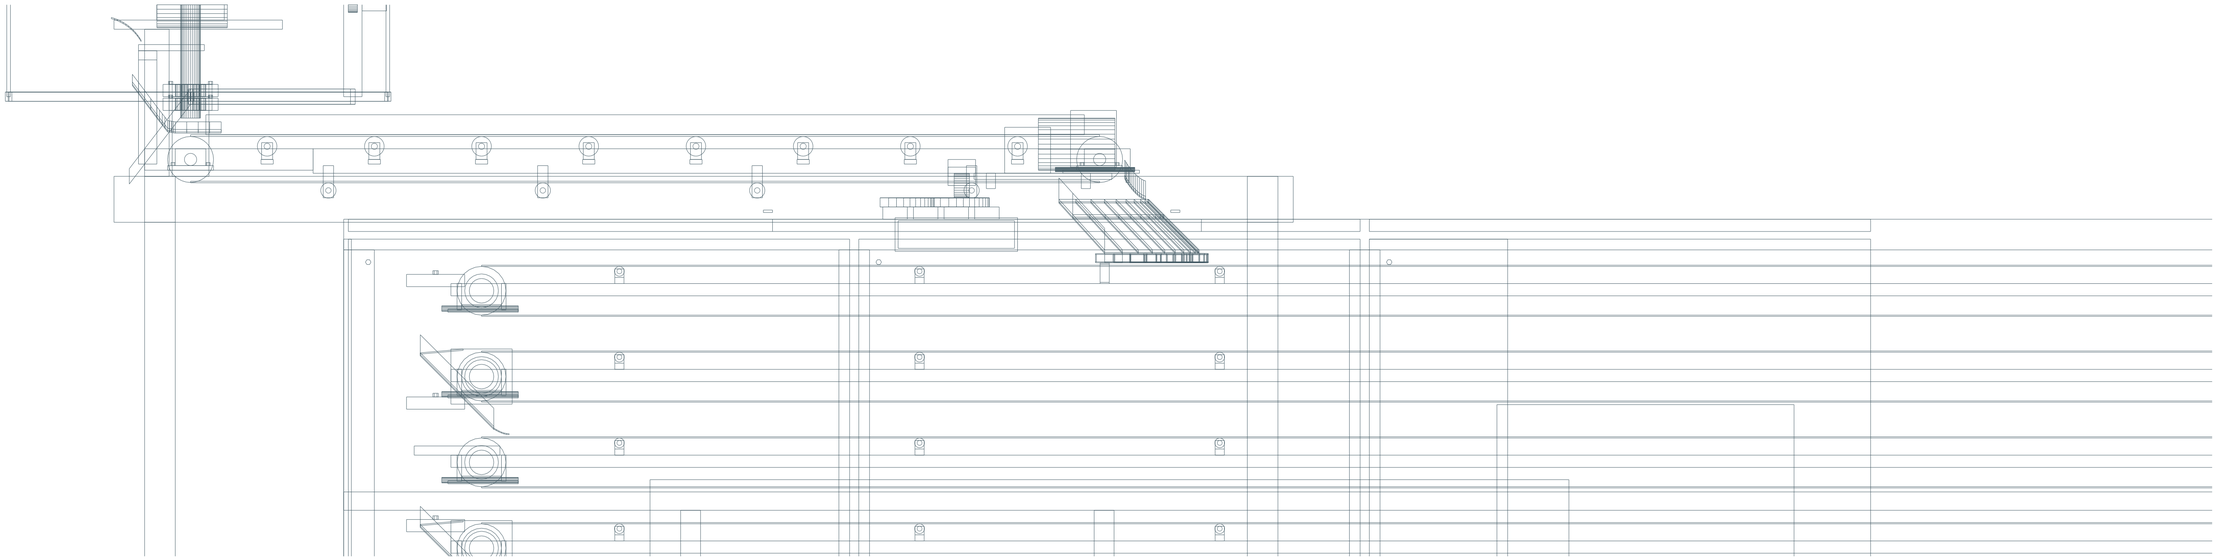

PLANTA · 1:10 · BARRIDO ±20°

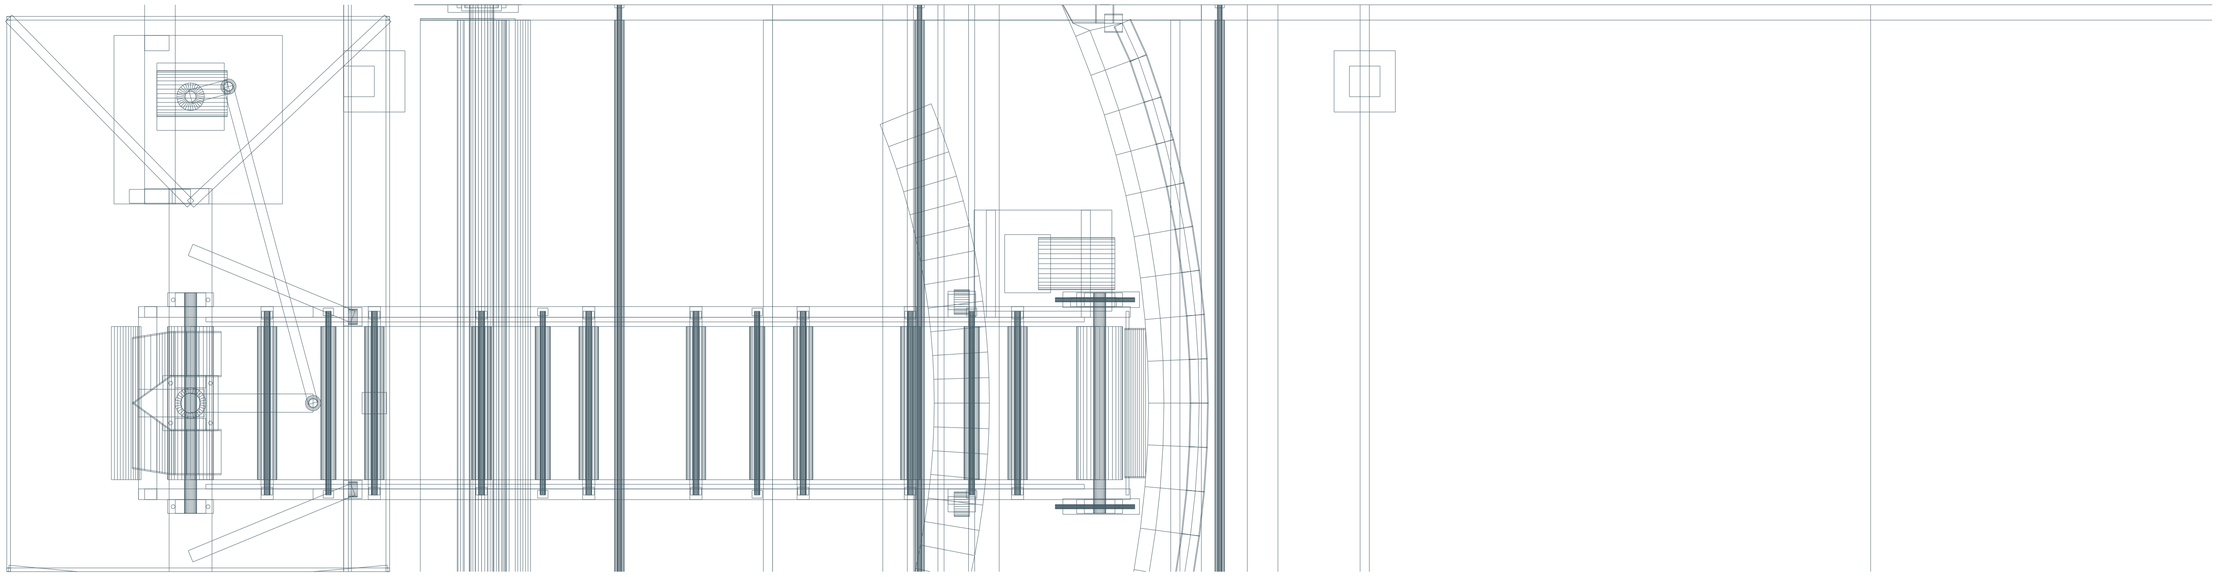

Desprendimiento a cuchara: 59.06 mm P. Cuchara!' apron: 10 mm. Apron!' L1: 50 mm.

El video aporta paneles aislantes, malla y elementos de guía visibles. Se conservan ancho útil 2500 mm y seis niveles; paso útil 280 mm.

PLANTA BRIQUETADORA · R19

08 · RESUMEN DE CAMBIOS Y CONDICIONES DE USO

R18 preservada · proyecto v2 · modos independientes y reversibles · consulta del dossier con ambas rutas.

Elemento	R18	R19
Ruta provisional	No incluida	C05 ↔ C07 ↔ pulmón B08
Colectora de prensa	C05 a +1270 mm de superficie	Conservada a +1270 mm
Transferencias de banda	Desniveles sin guía completa	Guías curvas revestidas y remates próximos
C07 provisional	No incluida	4350 mm entre ejes / 4.61499°
Tolva provisional	No incluida	Hueco 2 × 1,6 m / cama nominal 0,25 m
Retirada	Ruta al futuro secador	Continua, con fondo móvil B08
Secador	20 × 2,8 × 3 m / al piso	Dimensiones conservadas; acabado del video
Tolva / prensa / secador	Alturas fijas	Alturas fijas conservadas
Animación	Recorrido del secador	Ruta activa y superficies guiadas
Persistencia	Propuestas y revisiones anteriores	Conservadas, R19 se abre como referencia nueva

La alternativa provisional no representa almacenamiento prolongado ni capacidad de curado de briquetas.

La cama y los vuelos son geometría P/R. Velocidades de animación ilustrativas: no simulación productiva.

Caudal, potencia final del fondo móvil, carga bajo tolva y resistencia de las briquetas no se declaran validados.

Se conservan las cantidades y clasificaciones OEM; nuevas piezas P se separan en BOM por modo.

DXF incluye cotas DIMENSION nativas desde caras, centros y superficies reales; DWG se genera desde ese DXF.

Las revisiones anteriores y los borradores no se sobrescriben. El proyecto JSON contiene ambas alternativas.