
# PLANTA BRIQUETADORA · SECADOR R20


## 01 · CARCASA OEM CERRADA, EQUIPO AL PISO Y AUXILIARES

Reconstrucción desde ficha y video del equipo. Medidas en mm. O documentado / P propuesto / R reconstruido.


VISTA LATERAL · 1:50 · INTERIOR OCULTO

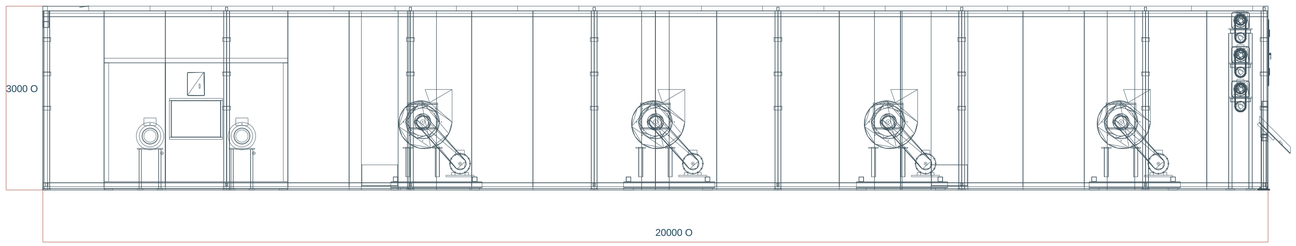


FRENTE DE ENTRADA · 1:20

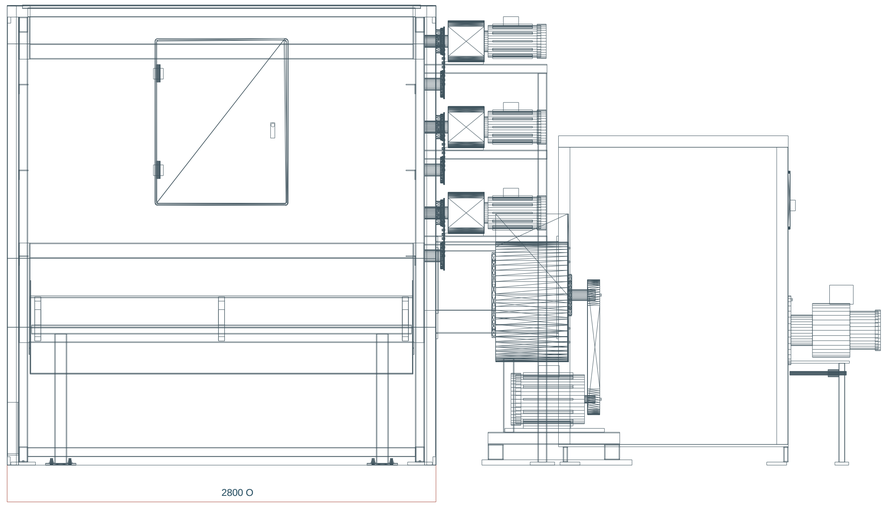


PLANTA · 1:50 · VENTILADORES Y CALENTADOR LATERALES

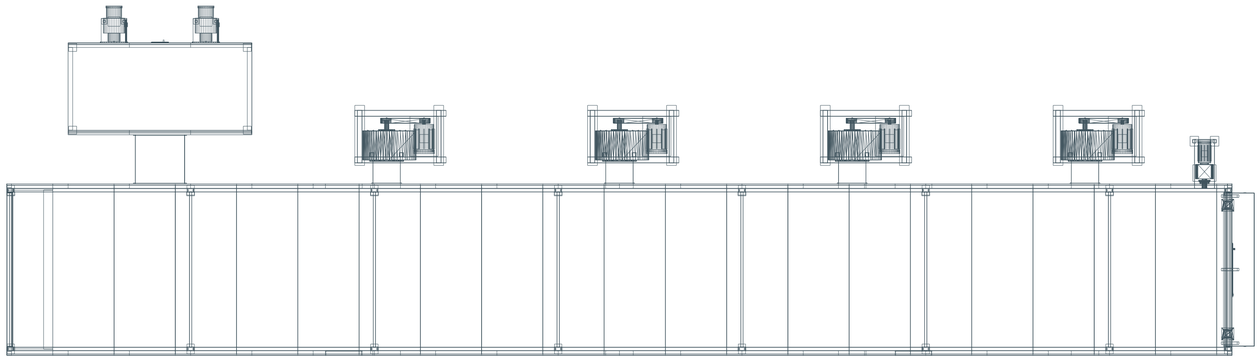

| Dato de ficha | Valor documentado O |
|---|---|
| Cuerpo | 20000 ×2800 ×3000 |
| Transporte | 6 niveles / útil2500 |
| Aislamiento | 75mm / lana mineral |
| Ventiladores | 4 ×15kW / soplado lateral |
| Accionamientos | 3 ×2,2kW |
| Calentador | 3000 ×1500 ×2150 |

Paneles lisos, juntas estrechas y dos registros bajos según foto; no se reproduce como textura permanente la película con rombos.


La carcasa se reconstruye completa. No se elevan el cuerpo ni sus patas; las cotas de bocas y apoyos de integración siguen siendo P/R.

# PLANTA BRIQUETADORA · SECADOR R20

## 02 · INTERIOR DE SEIS NIVELES Y TRANSMISIÓN EXTERIOR


Reconstrucción desde ficha y video del equipo. Medidas en mm. O documentado / P propuesto / R reconstruido.

### BANDAS, RETORNOS, EJES Y TRANSFERENCIAS · 1:50

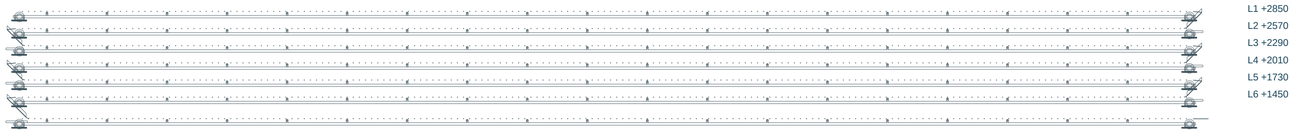


| Elemento | Ficha / reconstrucción |
|---|---|
| Banda útil | 2500mm O / inoxidable304 O |
| Malla fina | Abertura2mm O / hilo1mm O |
| Barras transversales | Paso100mm O / Ø12,7 R |
| Ejes de transporte | Ø80mm O |
| Base y pilares | RHS100×60×5 O |
| Travesaños | RHS60×40×3 O |
| Transferencias | Alternadas / paso280 y chutas P |

### EXTREMO DE BANDAS Y CADENAS · 1:10

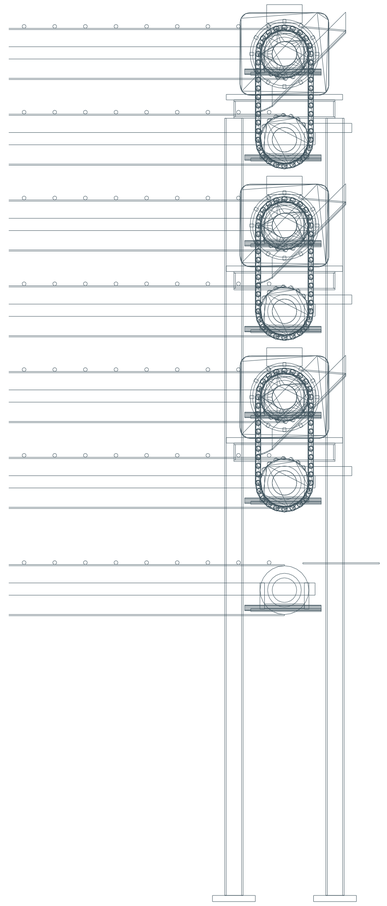

Seis pisos conservados. Paso útil280mm y recorrido alternado son la solución de integración de planta; no se atribuyen al video como cotas.

Las cadenas y motorreductores se muestran en el extremo mecánico. El ensacado del video no pertenece al secador y se excluye.


La malla se representa mediante superficie visual y detalle ampliado, evitando modelar millones de hilos.

# PLANTA BRIQUETADORA · SECADOR R20

## 03 · ALIMENTADOR PROPIO Y ACOPLE DIRECTO AL NIVEL SUPERIOR


Reconstrucción desde ficha y video del equipo. Medidas en mm. O documentado / P propuesto / R reconstruido.

ALIMENTADOR PROPIO · 1:25

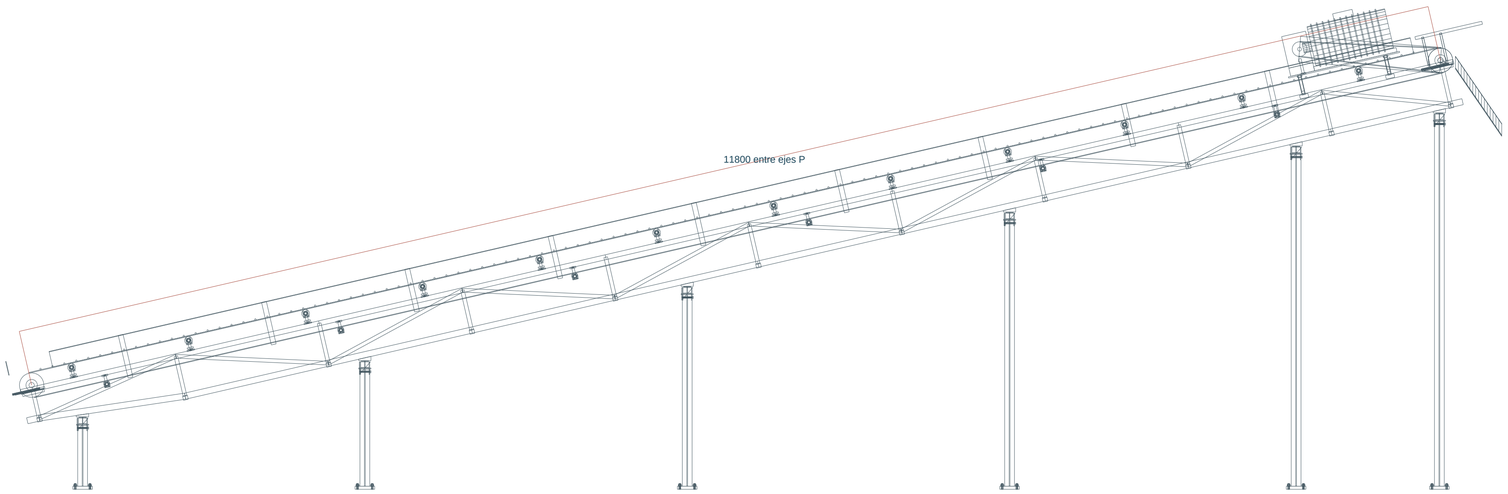


| Geometría | Valor |
|---|---|
| Longitud exterior nominal O | 12000mm |
| Ancho exterior nominal O | 3000mm |
| Espesor nominal O | 500mm |
| Ancho útil propuesto R | 2500mm |
| Entre ejes P | 11800.00mm |
| Pendiente instalada P | 12.98° |
| Ejes desde NPT P | 8 5 0 . 0 0 !' 3 5 0 0 . 0 0 m m |
| Vuelo inicial de guía P | 69.24mm |
| Remate sobre L1 P | 40mm |

ENTREGA GUIADA Y CIERRE DE TECHO · 1:5

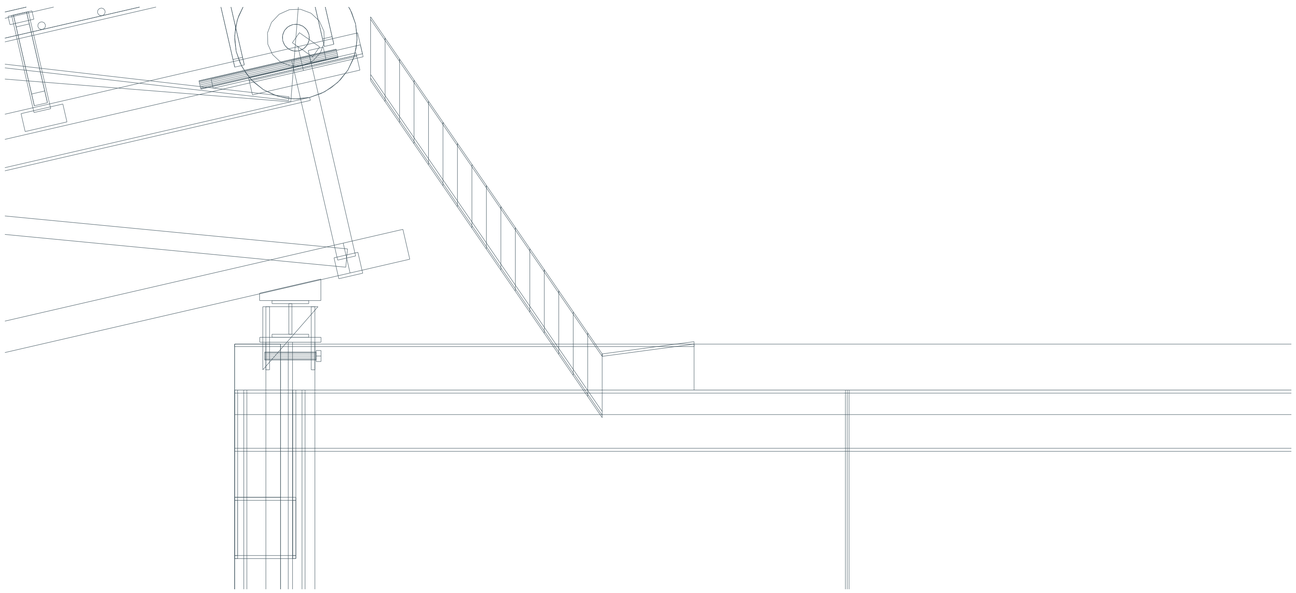

Se elimina la torre/repartidor oscilante de la reconstrucción anterior.

El acople termina sobre la superficie del nivel1, dentro de la carcasa.

El ancho útil del alimentador es R; el exterior de3m procede de la ficha.

La recepción desde C05 sigue centrada. No se afirma reparto uniforme.


La abertura de entrada y su capota se sellan por un cierre local P.

# PLANTA BRIQUETADORA · SECADOR R20


## 04 · INTEGRACIÓN EN LA PLANTA Y COMPARACIÓN

Reconstrucción desde ficha y video del equipo. Medidas en mm. O documentado / P propuesto / R reconstruido.

DISPOSICIÓN CON SECADOR · 1:100

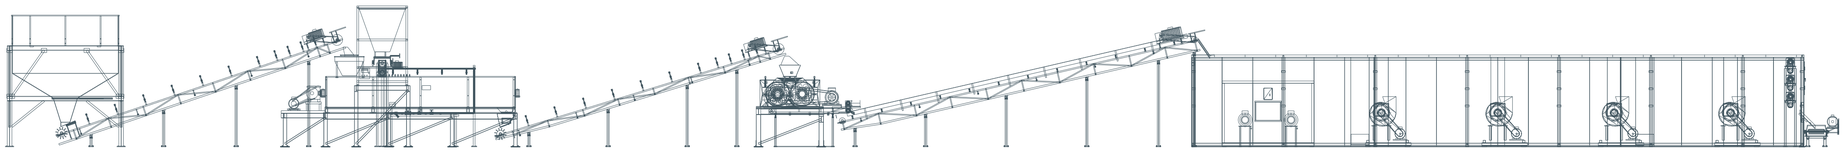

PLANTA GENERAL · 1:100

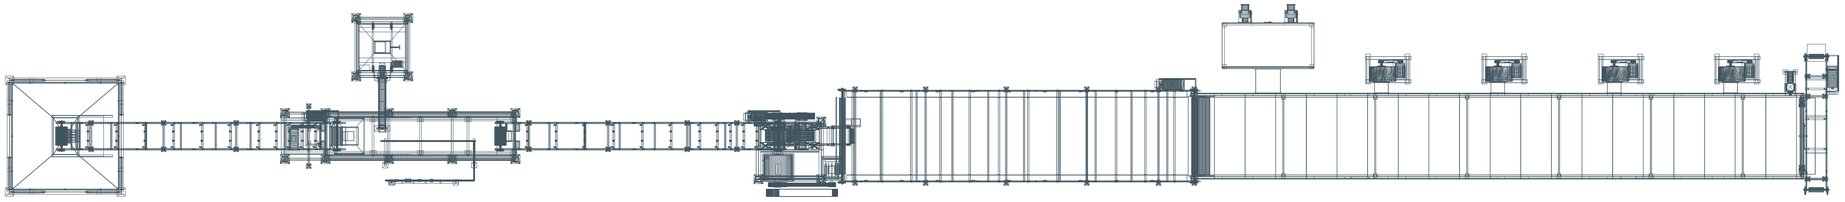

| Cinta | Entre ejes mm | Pendiente ° | Ancho útil mm | Exterior nominal mm |
|---|---|---|---|---|
| C01 | 9495.00 | 18.67 | 500.00 | 9855.00 |
| C02 | 9495.00 | 16.99 | 500.00 | 9855.00 |
| C05 | 2500.00 | 0.00 | 500.00 | 2680.00 |
| C03 | 11800.00 | 12.98 | 2500.00 | 12000.00 |
| C04 | 4350.00 | 0.00 | 500.00 | 4500.00 |

Envolvente mecánica 59.98m / con accesos 62.24m / límite75m.

Tolva, prensa y colectora próxima conservadas. Ruta provisional C07/B08 disponible; R19 y propuestas anteriores se conservan.